
**RESTAURANT
OWL'S NEST
DESIGN PROJECT**

DRAWING INDEX:

1. COVER PAGE
2. DRAWING INDEX
3. 3D VISUALIZATION
 - 3.1. FLOOR PLAN WITH CAMERAS
 - 3.2. - 3.19. 3D VISUALIZATION
4. CONSTRUCTION DRAWING
 - 4.1. FLOOR PLAN FURNITURE. VARIANT 5
 - 4.2. INSTALLATION AND REMOVAL PLAN
 - 4.3. FLOOR PLAN FLOORING
 - 4.4. FLOOR PLAN REFLECTED CEILING
 - 4.5. ELECTRIC LIGHTNING LAYOUT
 - 4.6. ELECTRIC SWITCHES LAYOUT
 - 4.7. ELECTRICAL OUTLET LAYOUT
 - 4.8. PLUMBING LAYOUT
 - 4.9. WALL FINISHES LAYOUT
 - 4.10. BASEBOARD MOLDING
 - 4.11. FINISHES LEGEND
5. ELEVATIONS DRAWING
 - 5.1. REFERENCE LAYOUT
 - 5.2. ELEVATION 1 A-G
 - 5.3. ELEVATION 1 G-A
 - 5.4. ELEVATION 2
 - 5.5. ELEVATION 3
 - 5.6. ELEVATION 4
 - 5.7. ELEVATION 5
6. SCHEMES FURNITURE, JOINERY
 - 6.1. FURNITURE, JOINERY LEGEND
 - 6.2. DOORS
 - 6.3. WINDOW TO THE KITCHEN
 - 6.4. SOFAS: SF-1; SF-2
 - 6.5. SOFAS: SF-3; B-1
 - 6.6. TABLES: T-1; T-2; T-3; T-4
 - 6.7. TABLES: T-5; T-6; T-7
 - 6.8. STATIONS: S; ST-1; ST-2
 - 6.9. BOOKCASE
 - 6.10. WINE ROOM
 - 6.11. BAR - 1
 - 6.12. BAR - 2
 - 6.13. WARDROBE AND STAIRS
 - 6.14. MIRROR AND COUNTERTOP SINK IN WC
 - 6.15. PARTITIONS IN WC
 - 6.16. SCHEME TERRACE AND PLANT POTS
7. FURNITURE, LIGHT AND PLANTS
 - 7.1. FURNITURE LAYOUT
 - 7.2. FURNITURE
 - 7.3. FURNITURE
 - 7.4. LIGHTING LAYOUT
 - 7.5.- 7.6.1 LIGHTING
 - 7.7. RESTROOM
 - 7.8.-7.9. PLANTS
- 8.-8.3. DECOR

RESTAURANT
OWL'S NEST

DRAWING TITLE:
DRAWING INDEX

DRAWN BY: KEIDUNOV IRINA

-


-

DATE: 03.21.2022

SHEET : 2

-

3D VISUALIZATION

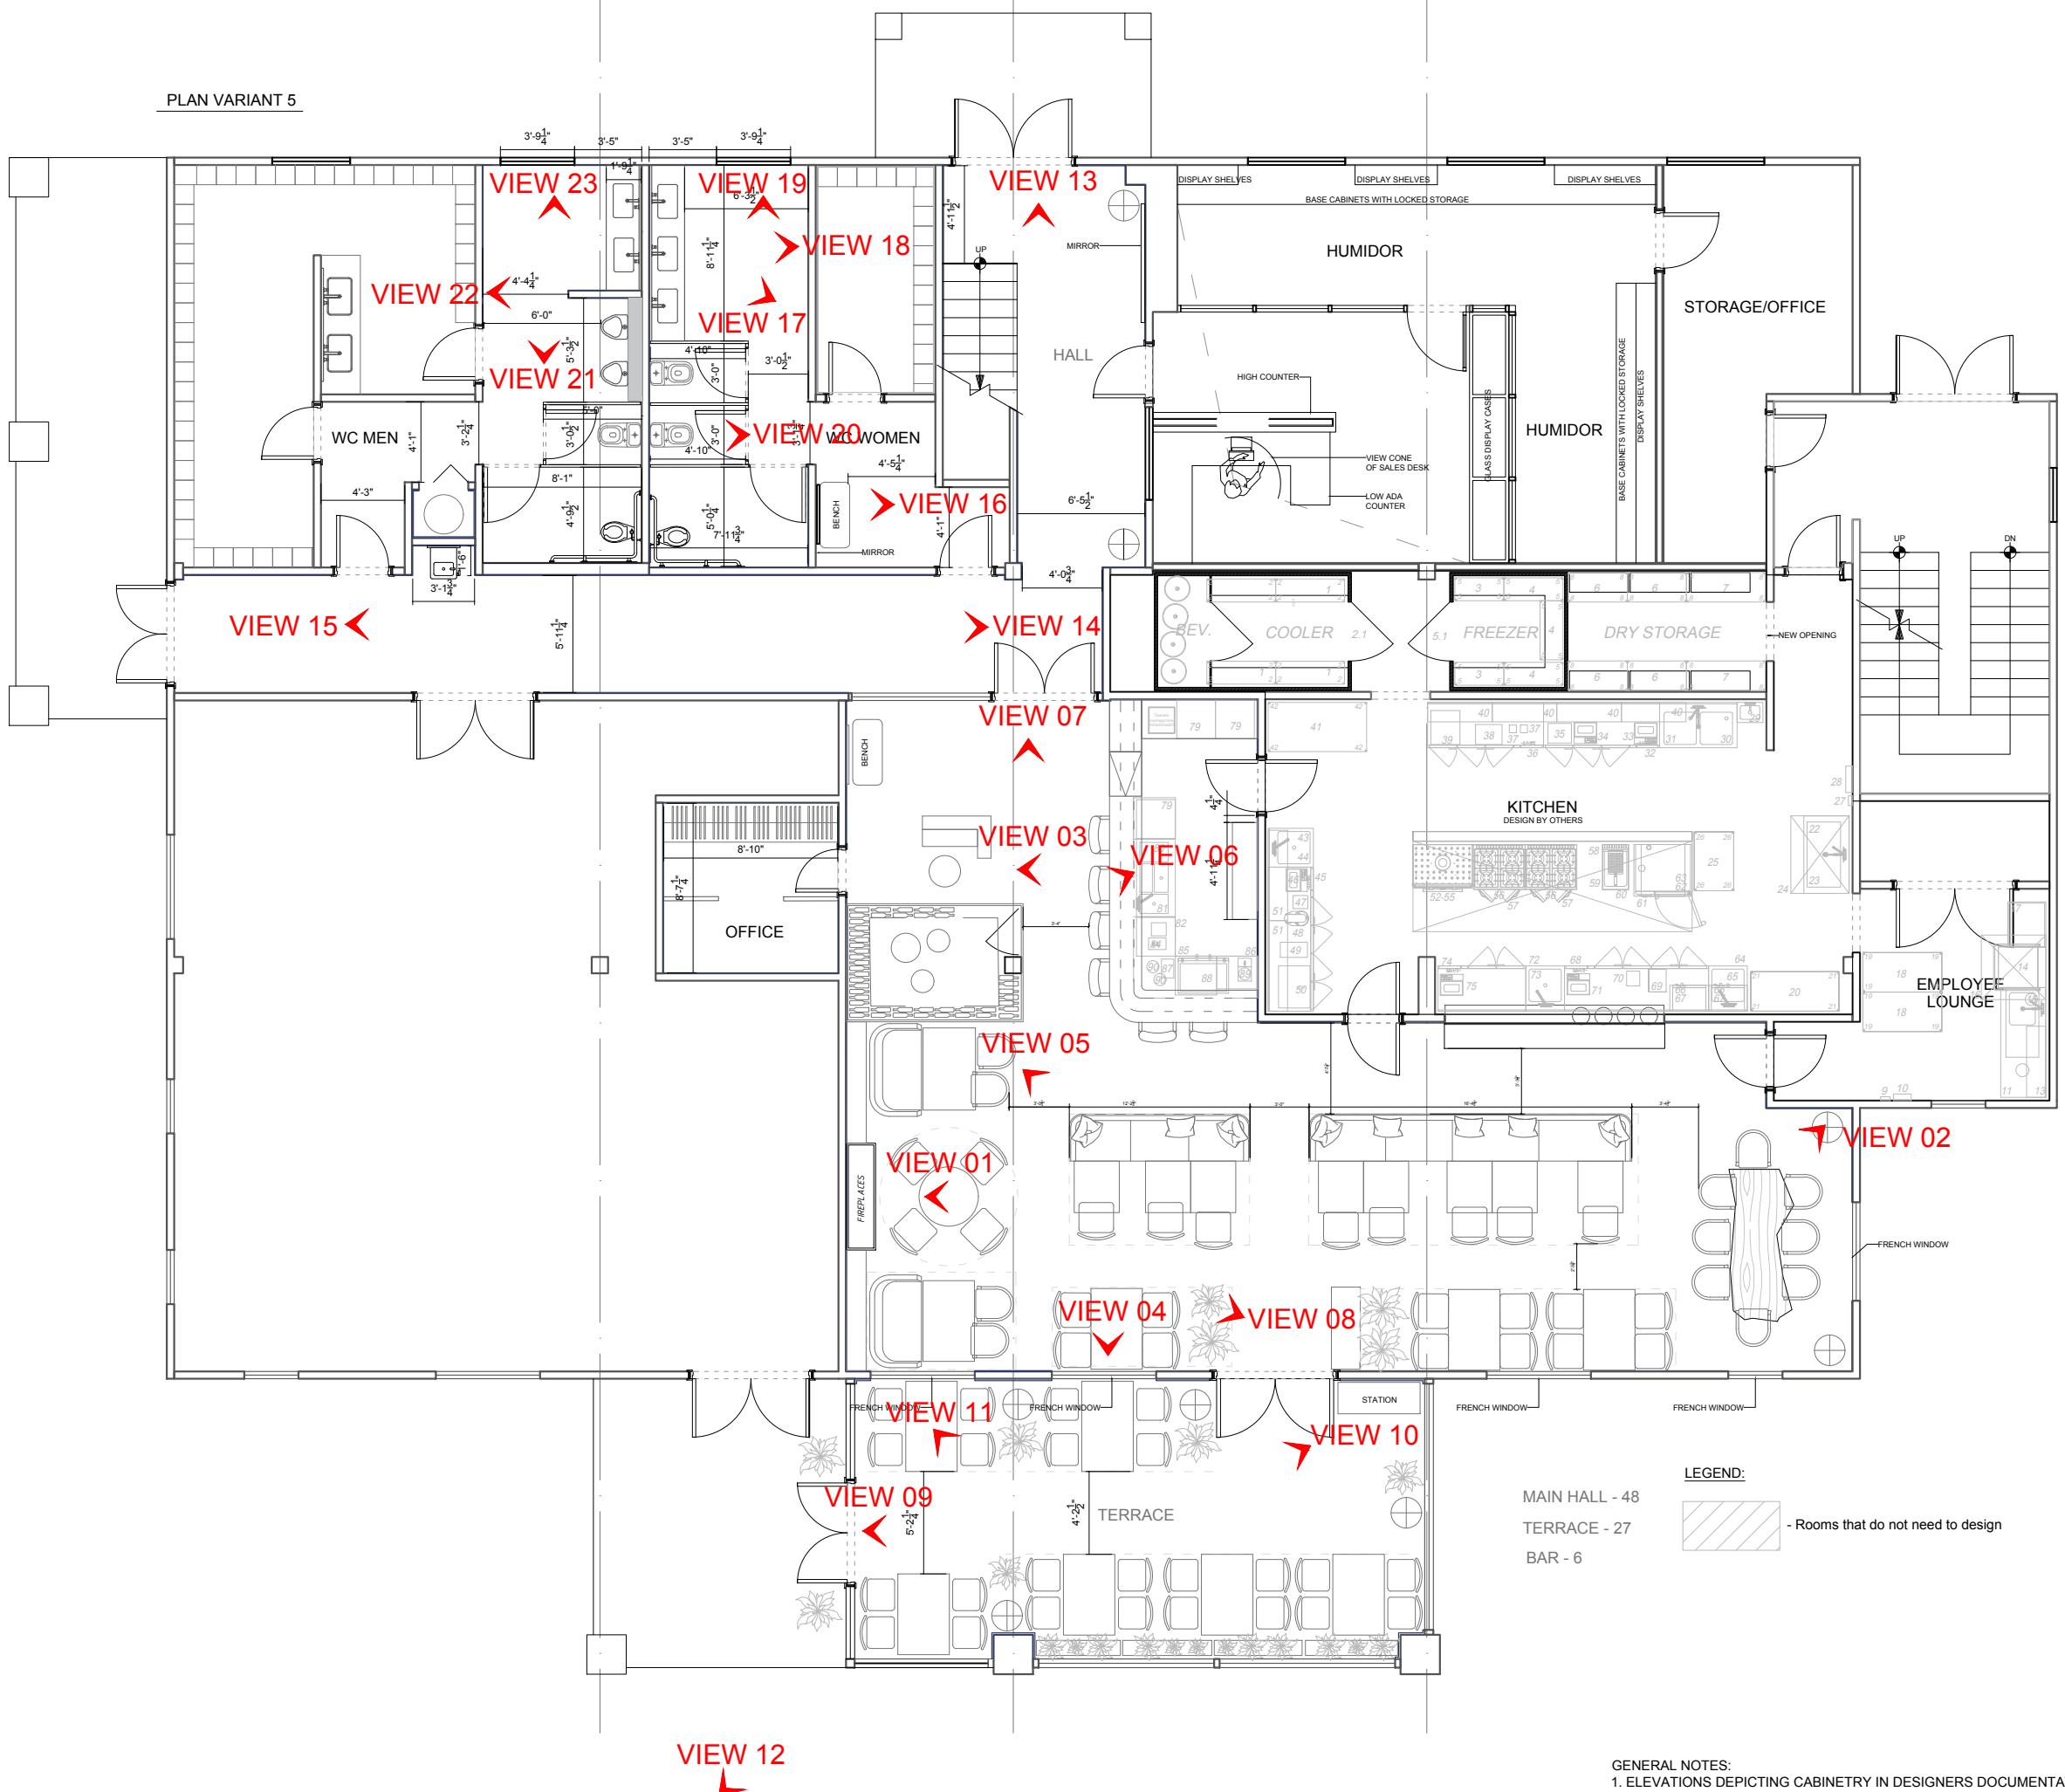

RESTAURANT OWL'S NEST

DRAWING TITLE:
**FLOOR PLAN WITH
CAMERAS**

DRAWN BY: KEIDUNOV IRINA

SCALE: 1/4"=1'-0"

DATE: 03.21.2022

SHEET : 3.1

A1

GENERAL NOTES:
1. ELEVATIONS DEPICTING CABINETRY IN DESIGNERS DOCUMENTATION IS FOR DESIGN PURPOSES ONLY.
2. DESIGNER DOES NOT ASSUME THE RESPONSIBILITY OF ANY STRUCTURAL OR FIELD DIMENSIONS/CONDITIONS.

LEGEND:
- Rooms that do not need to design



VIEW 01

RESTAURANT
OWL'S NEST

DRAWING TITLE:
3D VIZUALIZATION

DRAWN BY: KEIDUNOV IRINA

DATE: 03.21.2022

SHEET : 3.2

A1



VIEW 02

RESTAURANT
OWL'S NEST

DRAWING TITLE:
3D VIZUALIZATION

DRAWN BY: KEIDUNOV IRINA

DATE: 03.21.2022

SHEET : 3.3

A1



VIEW 03

RESTAURANT
OWL'S NEST

DRAWING TITLE:
3D VIZUALIZATION

DRAWN BY: KEIDUNOV IRINA

DATE: 03.21.2022

SHEET : 3.4

A1



VIEW 04

RESTAURANT
OWL'S NEST

DRAWING TITLE:
3D VIZUALIZATION

DRAWN BY: KEIDUNOV IRINA

DATE: 03.21.2022

SHEET : 3.5

A1



VIEW 05

RESTAURANT
OWL'S NEST

DRAWING TITLE:
3D VIZUALIZATION

DRAWN BY: KEIDUNOV IRINA

DATE: 03.21.2022

SHEET : 3.6

A1



VIEW 06

RESTAURANT
OWL'S NEST

DRAWING TITLE:
3D VIZUALIZATION

DRAWN BY: KEIDUNOV IRINA

DATE: 03.21.2022

SHEET : 3.7

A1



VIEW 07

RESTAURANT
OWL'S NEST

DRAWING TITLE:
3D VIZUALIZATION

DRAWN BY: KEIDUNOV IRINA

DATE: 03.21.2022

SHEET : 3.8

A1



VIEW 08

RESTAURANT
OWL'S NEST

DRAWING TITLE:
3D VIZUALIZATION

DRAWN BY: KEIDUNOV IRINA

DATE: 03.21.2022

SHEET : 3.9

A1



RESTAURANT
OWL'S NEST

DRAWING TITLE:
3D VIZUALIZATION

DRAWN BY: KEIDUNOV IRINA

DATE: 03.21.2022

SHEET : 3.10



RESTAURANT
OWL'S NEST

DRAWING TITLE:
3D VIZUALIZATION

DRAWN BY: KEIDUNOV IRINA

DATE: 03.21.2022

SHEET : 3.11

A1



VIEW 11

RESTAURANT
OWL'S NEST

DRAWING TITLE:
3D VIZUALIZATION

DRAWN BY: KEIDUNOV IRINA

DATE: 03.21.2022

SHEET : 3.12

VIEW 12



RESTAURANT
OWL'S NEST


DRAWING TITLE:
3D VIZUALIZATION

DRAWN BY: KEIDUNOV IRINA

DATE: 03.21.2022

SHEET : 3.13

A1

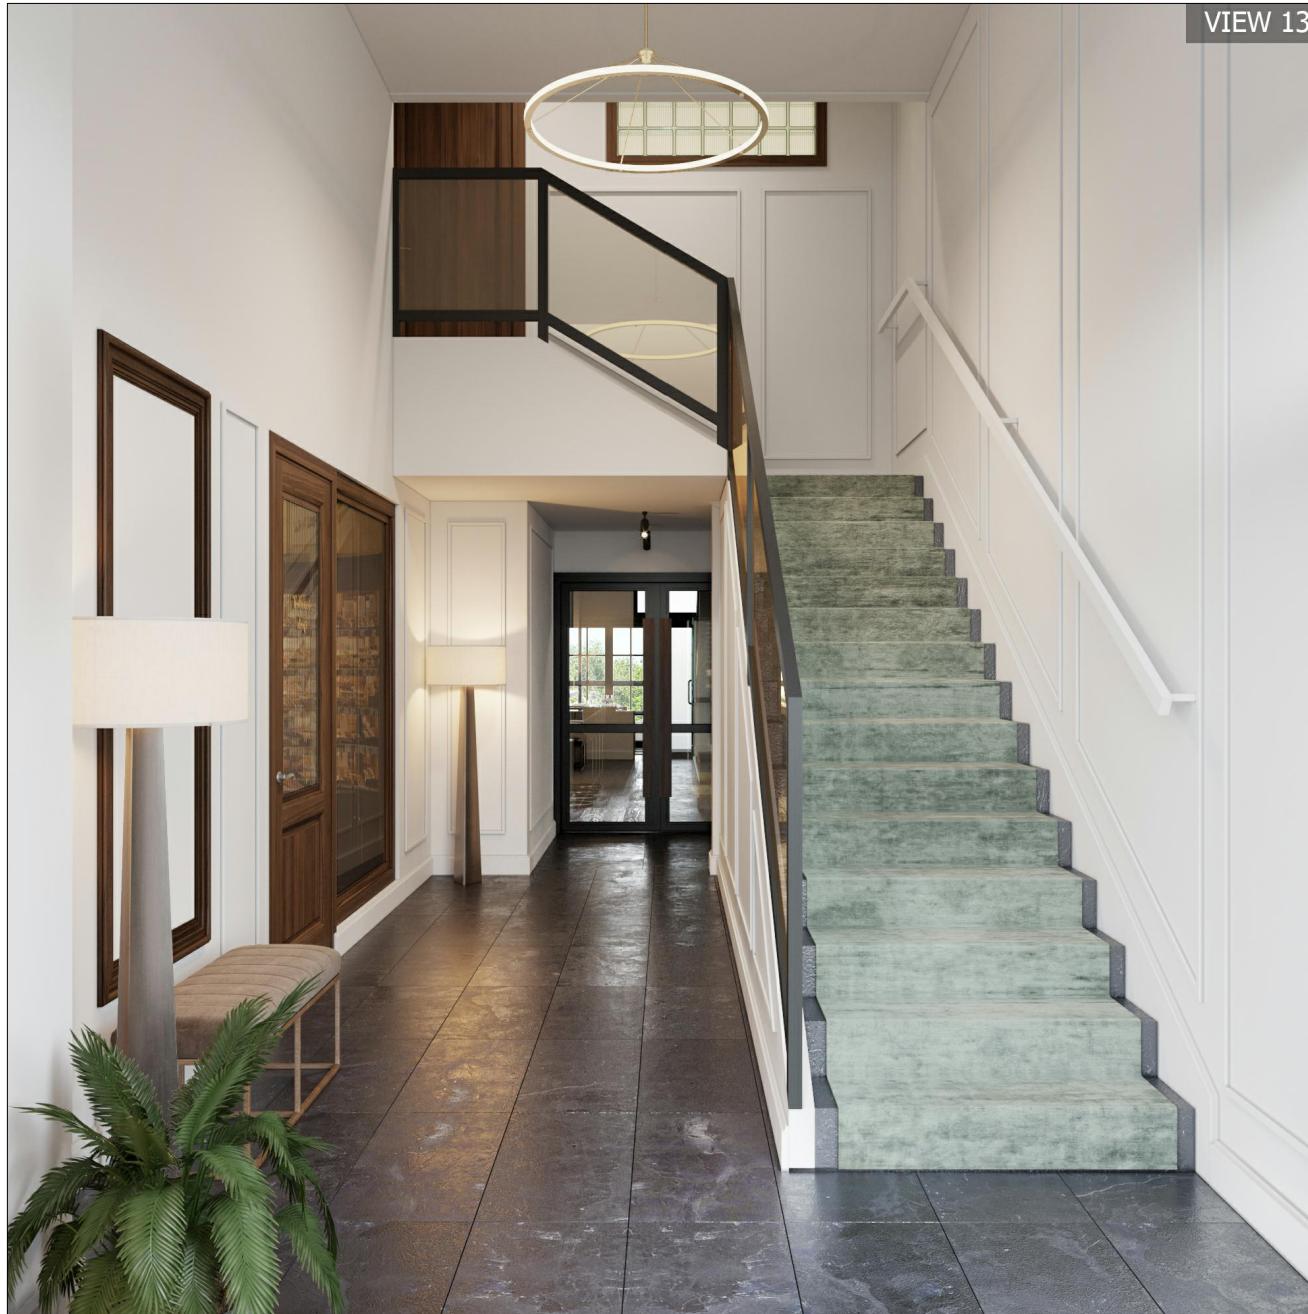

RESTAURANT
OWL'S NEST

DRAWING TITLE:
3D VIZUALIZATION

DRAWN BY: KEIDUNOV IRINA

DATE: 03.21.2022

SHEET : 3.14



RESTAURANT
OWL'S NEST

DRAWING TITLE:
3D VIZUALIZATION


DRAWN BY: KEIDUNOV IRINA

DATE: 03.21.2022

SHEET : 3.15



VIEW 17

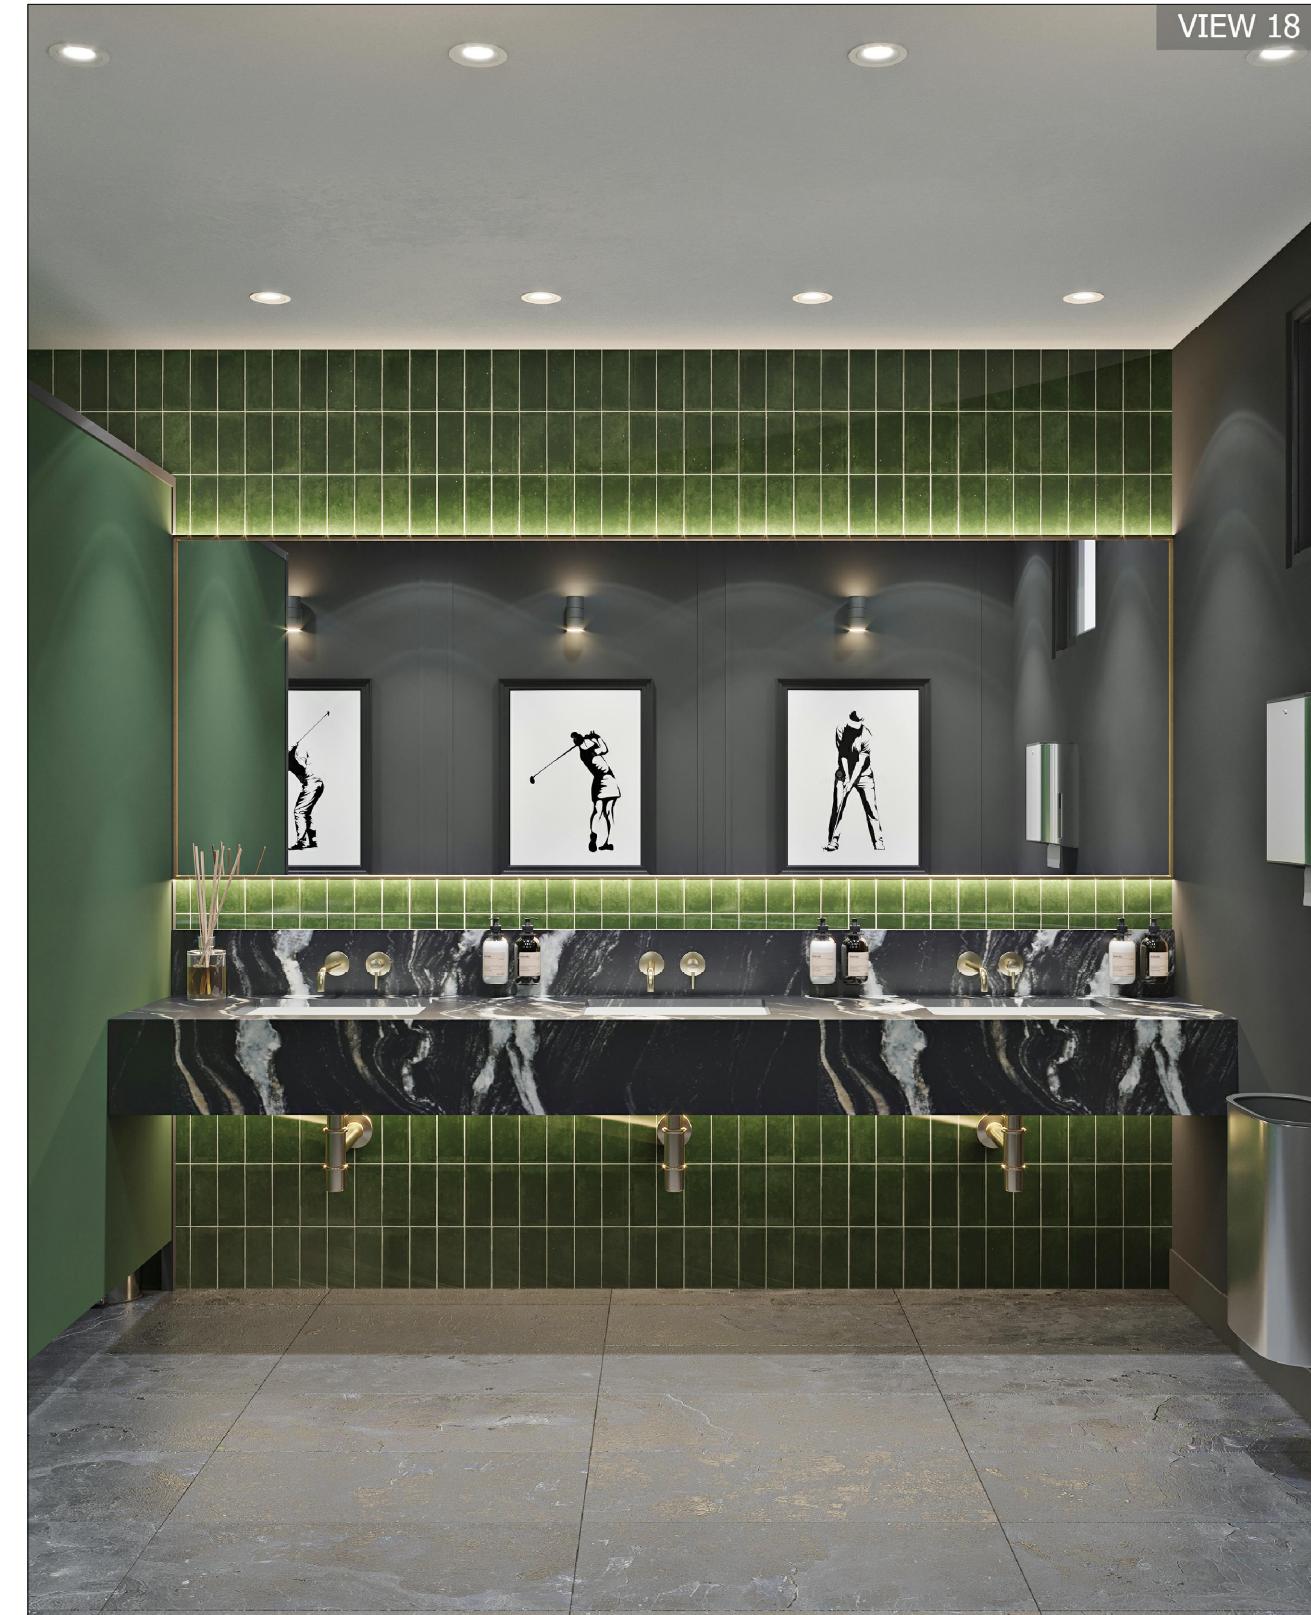

VIEW 18

RESTAURANT
OWL'S NEST

DRAWING TITLE:
3D VIZUALIZATION

DRAWN BY: KEIDUNOV IRINA

DATE: 03.21.2022

SHEET : 3.16

A1



RESTAURANT
OWL'S NEST

DRAWING TITLE:
3D VIZUALIZATION

DRAWN BY: KEIDUNOV IRINA

DATE: 03.21.2022

SHEET : 3.17

A1



RESTAURANT
OWL'S NEST

DRAWING TITLE:
3D VIZUALIZATION

DRAWN BY: KEIDUNOV IRINA

DATE: 03.21.2022

SHEET : 3.18

A1



RESTAURANT
OWL'S NEST

DRAWING TITLE:
3D VIZUALIZATION


DRAWN BY: KEIDUNOV IRINA

DATE: 03.21.2022

SHEET : 3.19

A1

CONSTRUCTION DRAWING

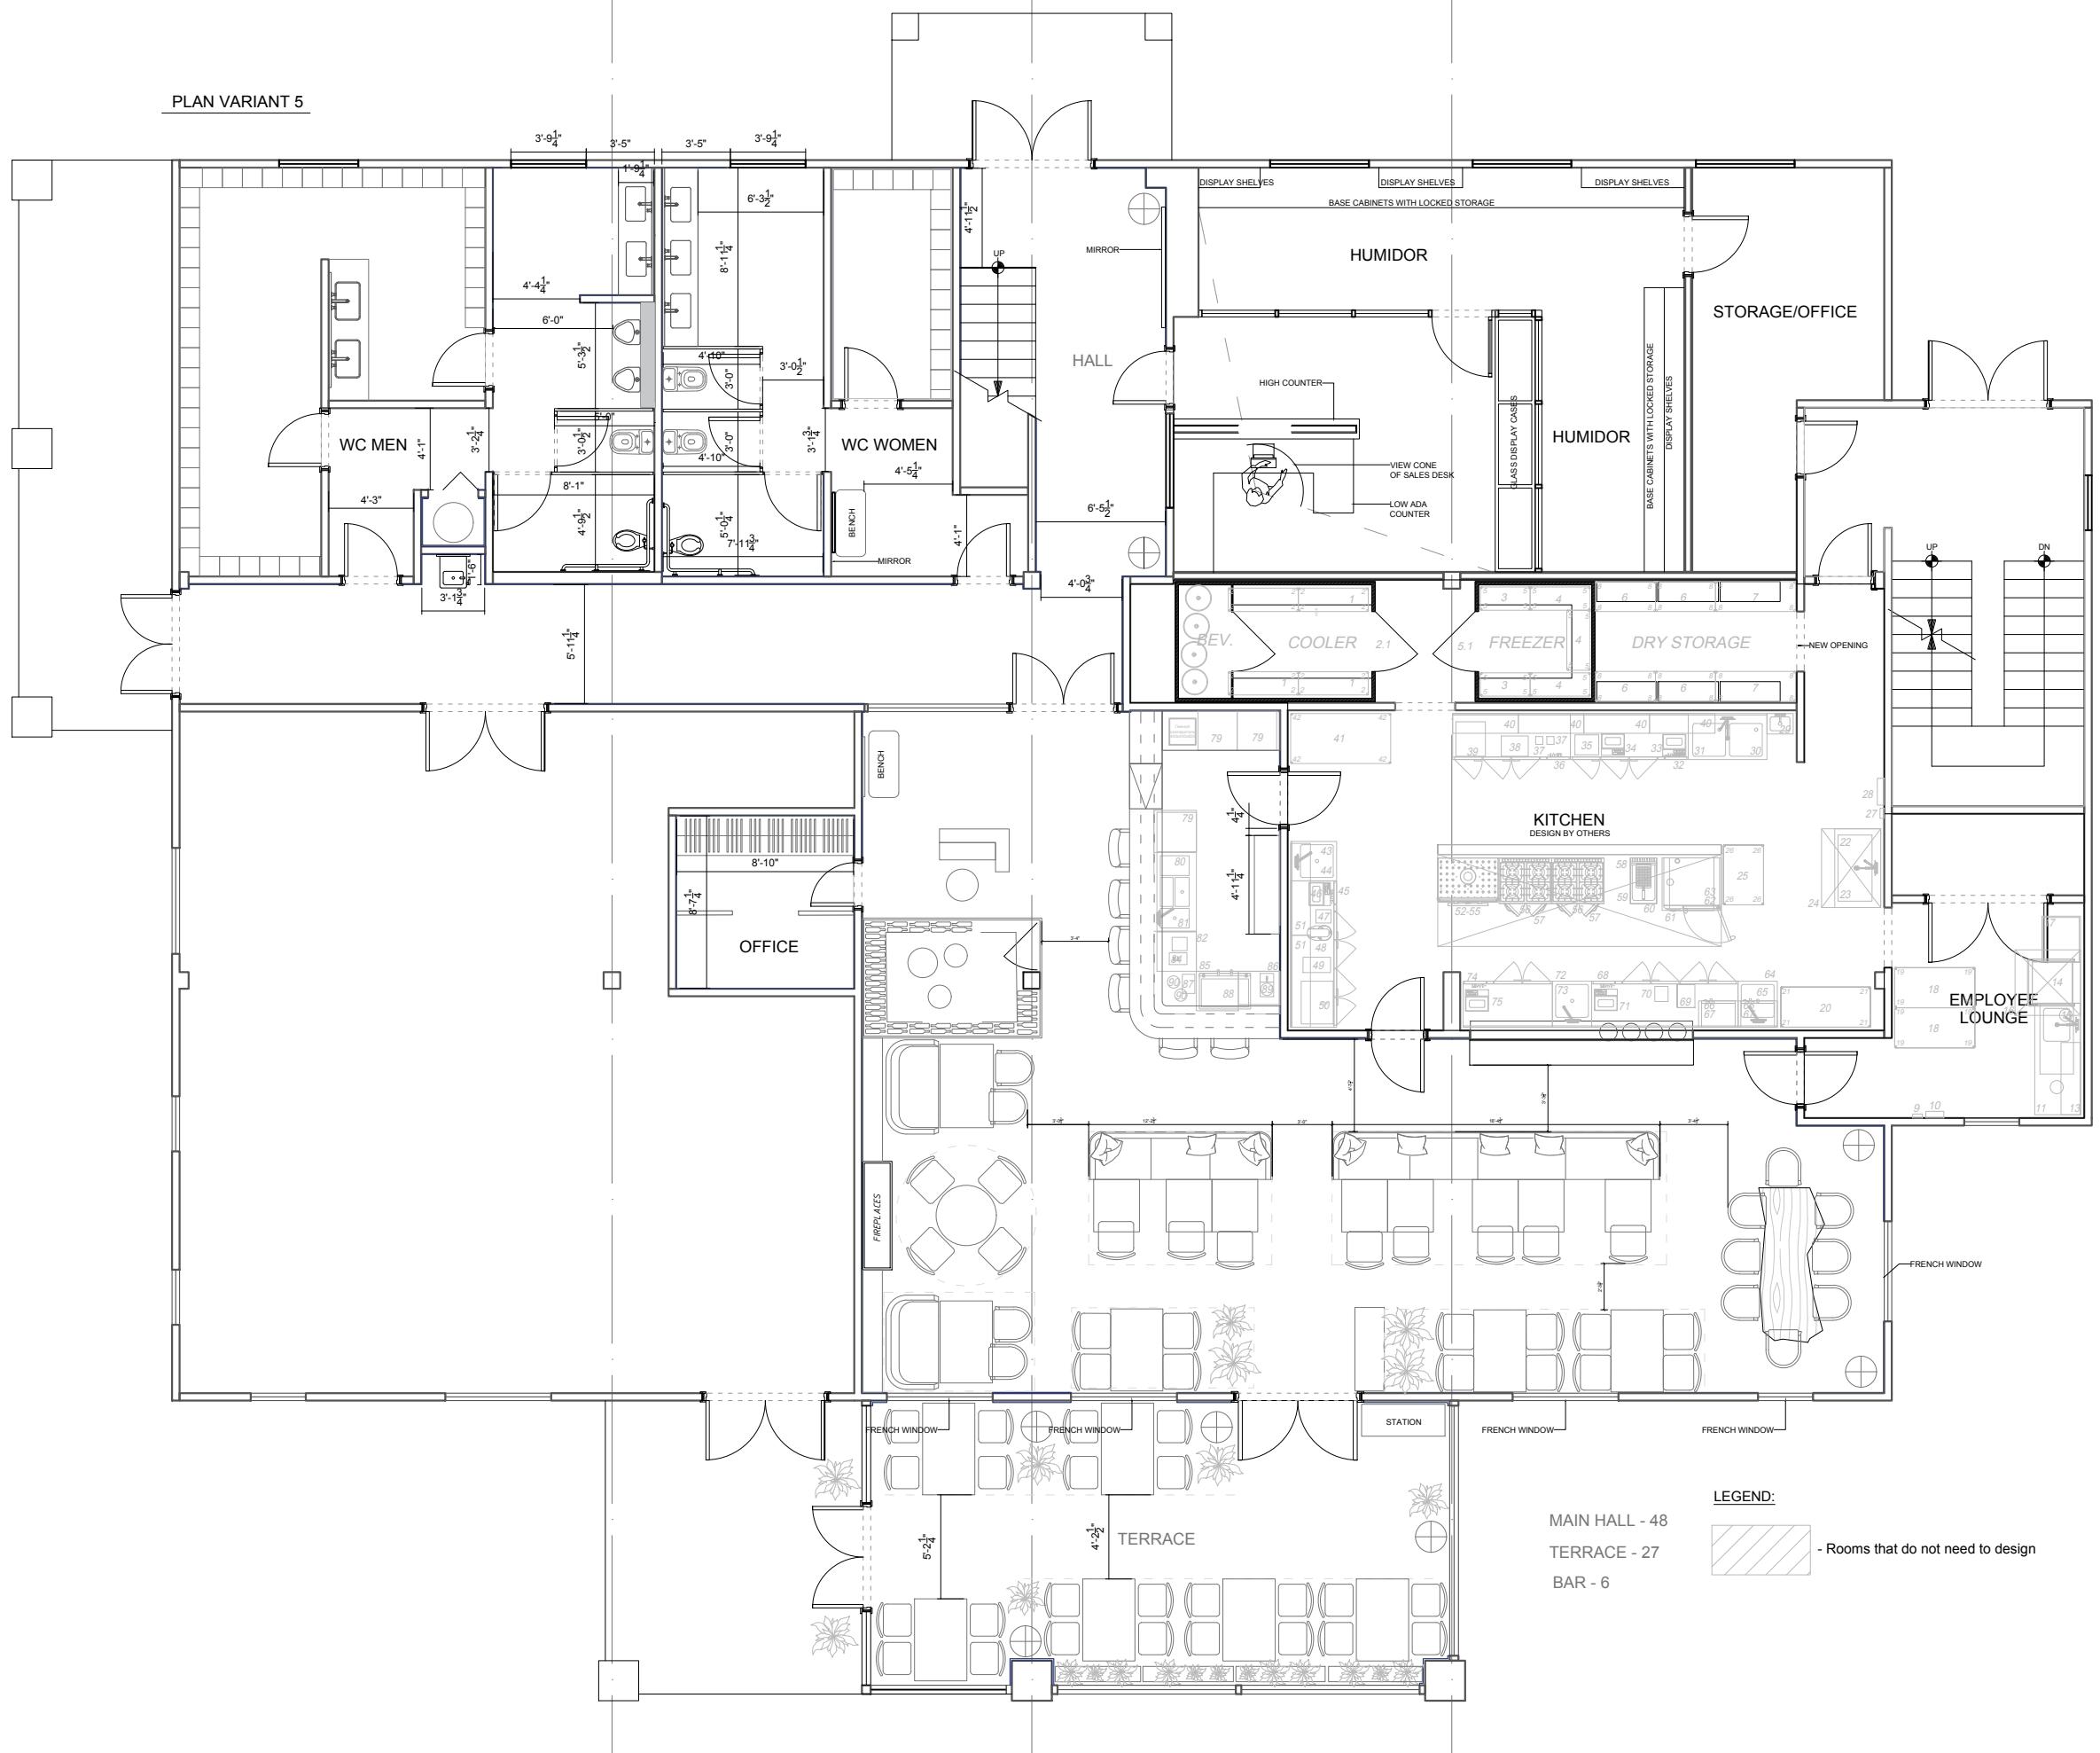

RESTAURANT OWL'S NEST

DRAWING TITLE:
FLOOR PLAN FURNITURE

DRAWN BY: KEIDUNOV IRINA

SCALE: 1/4"=1'-0"

DATE: 03.21.2022


SHEET : 4.1


A1

GENERAL NOTES:
1. ELEVATIONS DEPICTING CABINETRY IN DESIGNERS DOCUMENTATION IS FOR DESIGN PURPOSES ONLY.
2. DESIGNER DOES NOT ASSUME THE RESPONSIBILITY OF ANY STRUCTURAL OR FIELD DIMENSIONS/CONDITIONS.

LEGEND:
- Rooms that do not need to design

**RESTAURANT
OWL'S NEST**

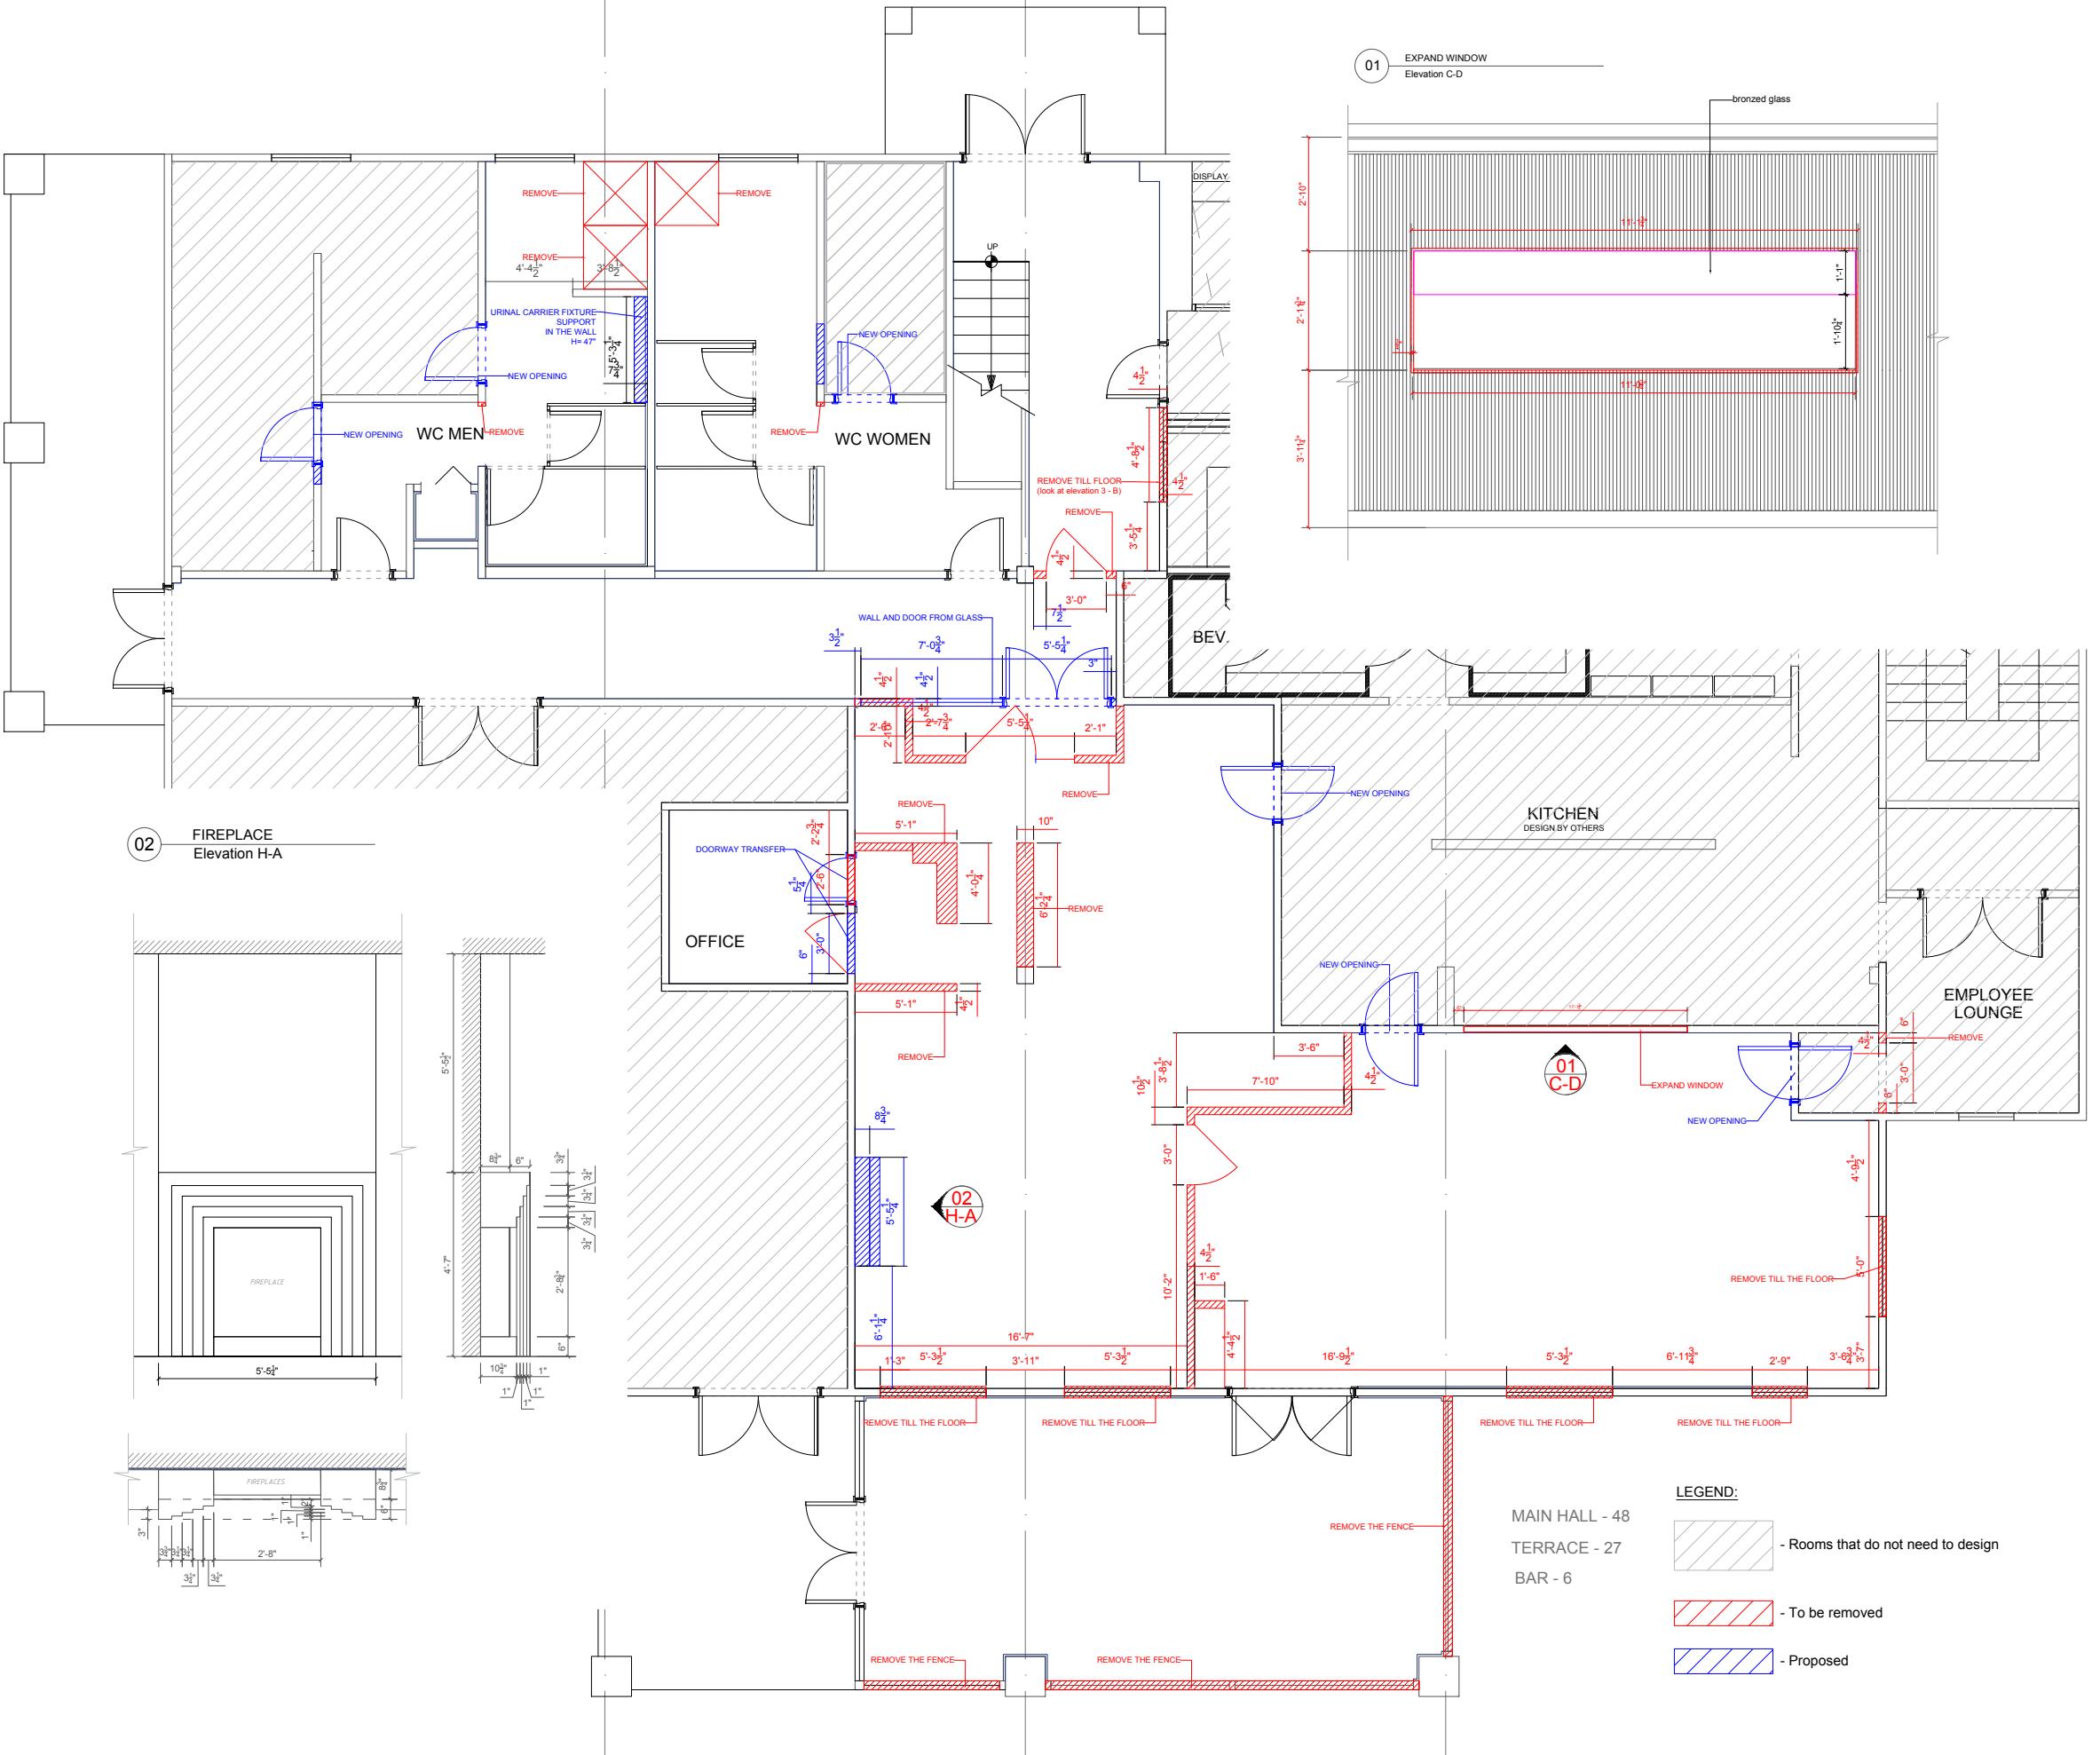

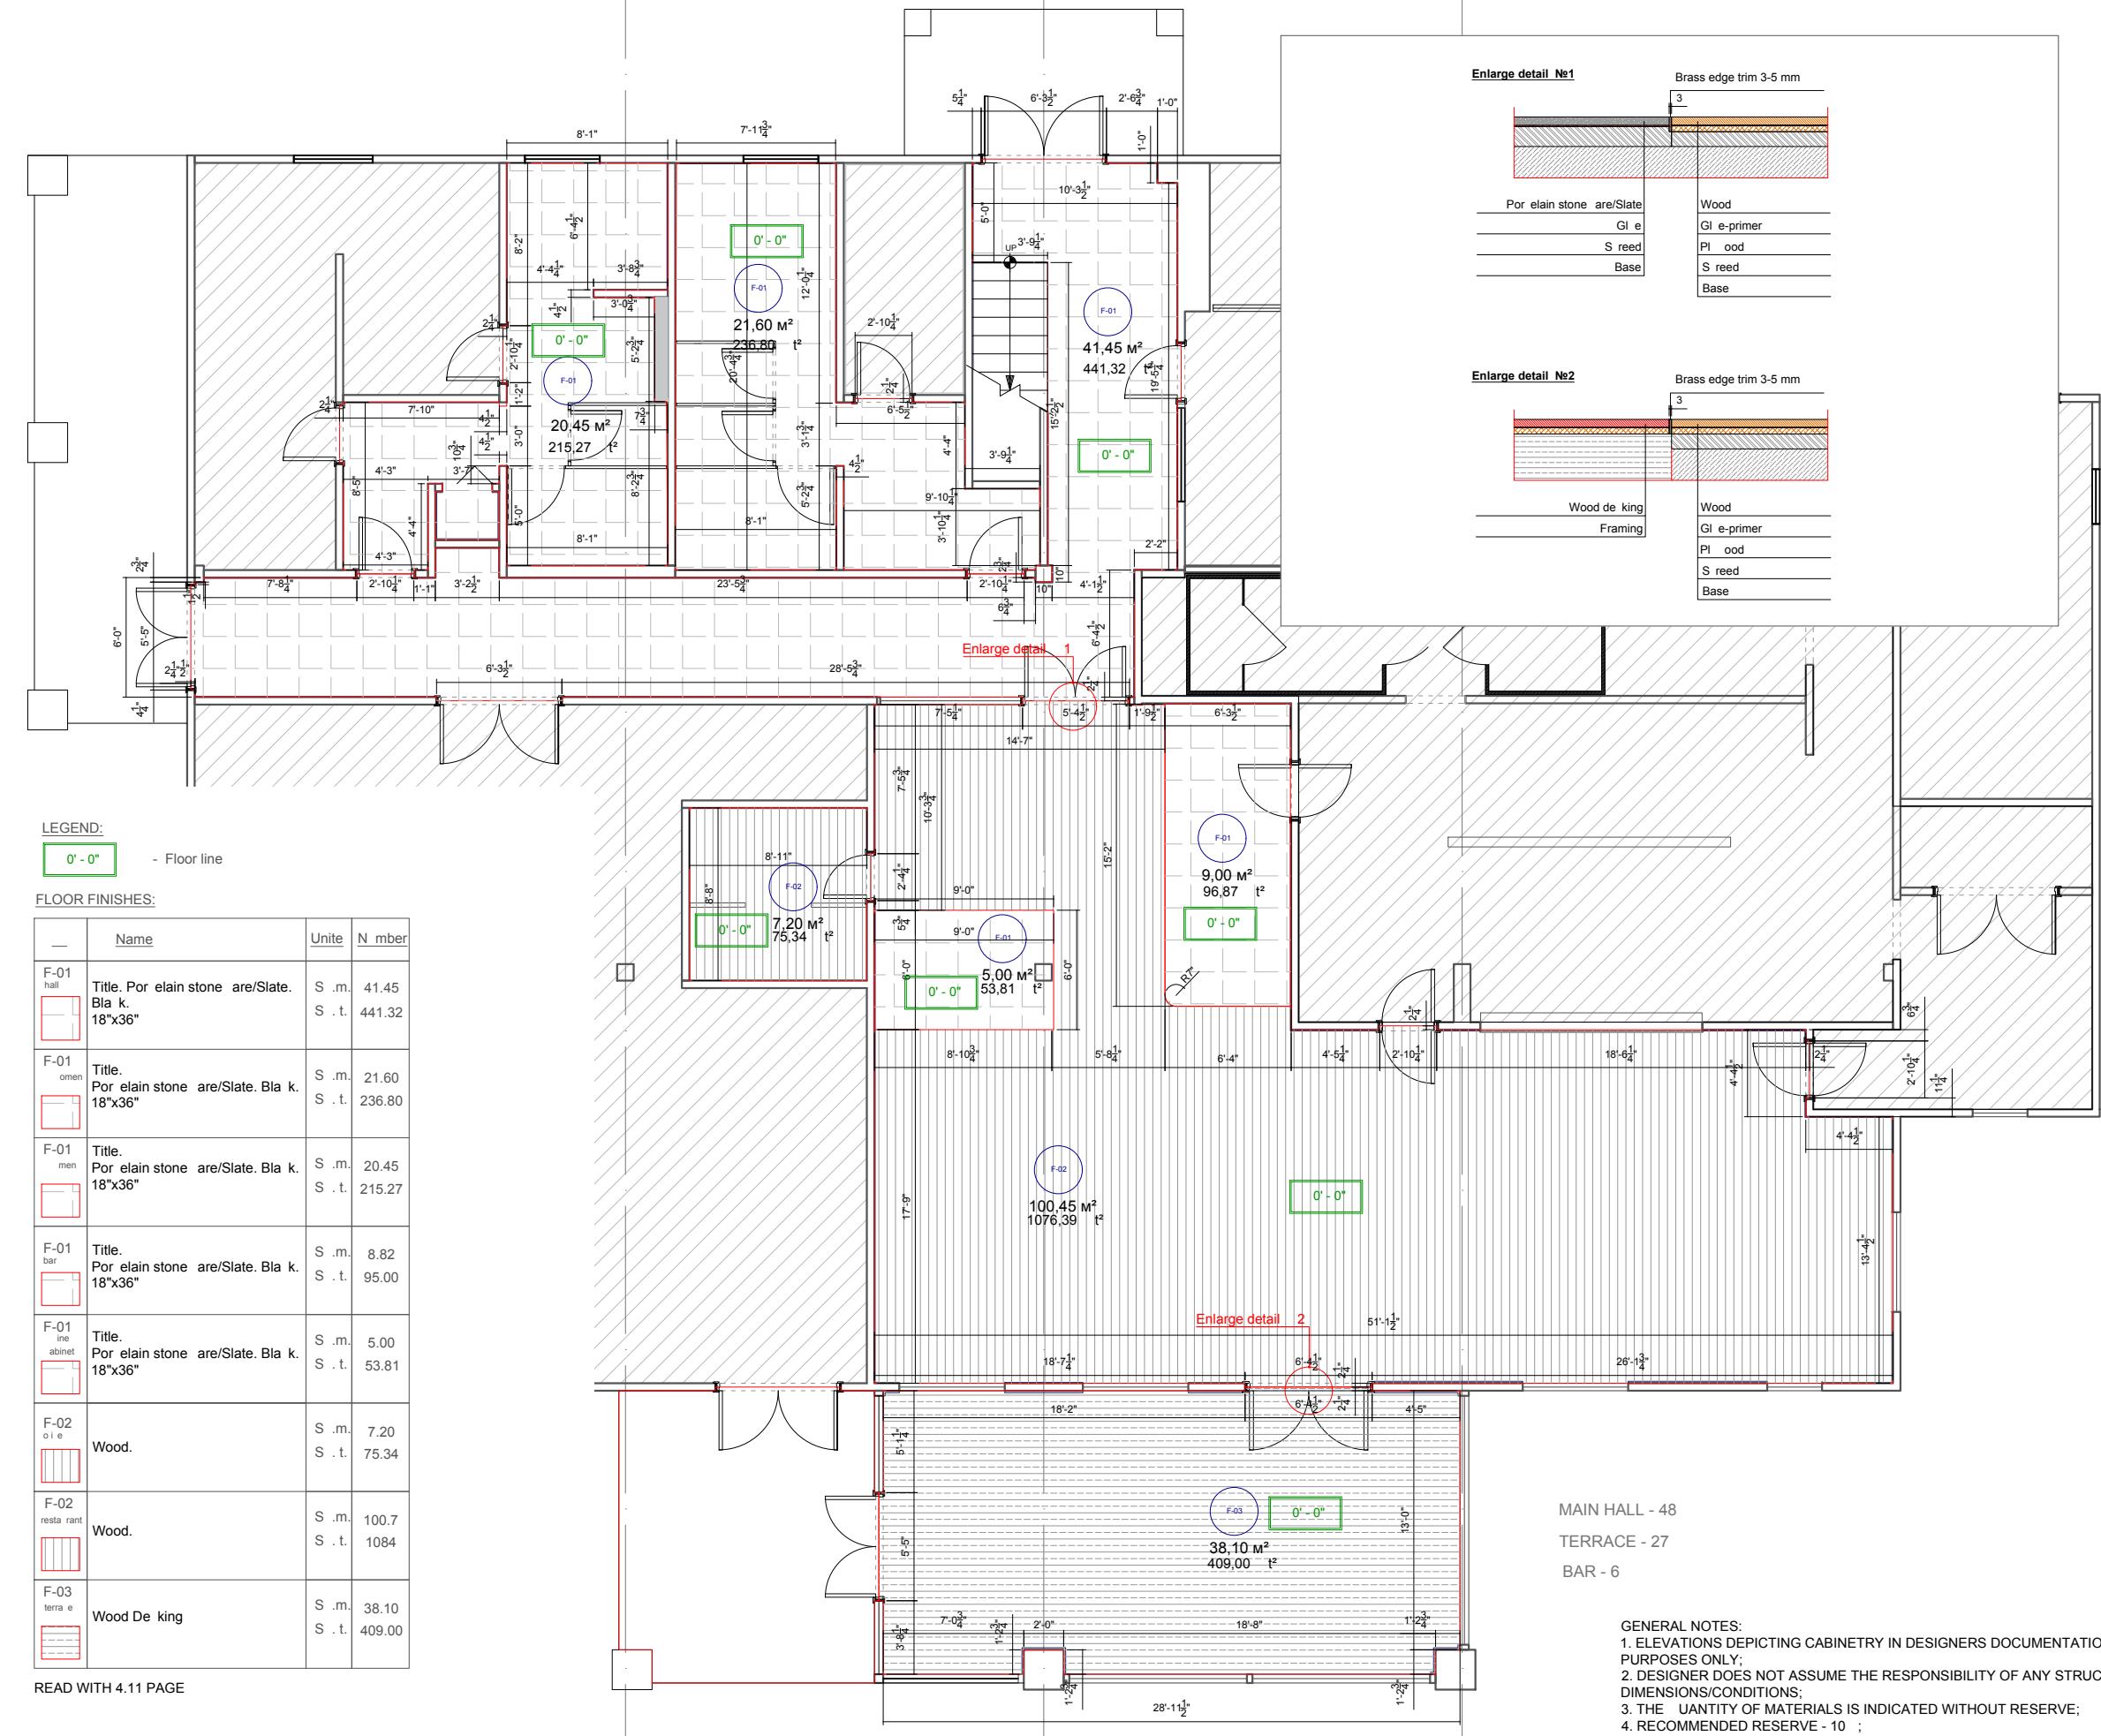

RESTAURANT OWL'S NEST

DRAWING TITLE:
FLOOR PLAN FLOORING

DRAWN BY: KEIDUNOV IRINA

SCALE: 1/4"=1'-0"


DATE: 03.21.2022

SHEET : 4.3

MAIN HALL - 48
TERRACE - 27
BAR - 6

GENERAL NOTES:

- ELEVATIONS DEPICTING CABINETRY IN DESIGNERS DOCUMENTATION IS FOR DESIGN PURPOSES ONLY;
- DESIGNER DOES NOT ASSUME THE RESPONSIBILITY OF ANY STRUCTURAL OR FIELD DIMENSIONS/CONDITIONS;
- THE UANTITY OF MATERIALS IS INDICATED WITHOUT RESERVE;
- RECOMMENDED RESERVE - 10 %;
- ABOUT FINISHES ON THE TERRACE MAKE LAST DECISION WITH CLIENT.
- On e the material or the floor is selected, e need to rea h o t the a tor to ind o t hether the have o -the-shef stair steps. I the don't have them, e need to ask them to the tiles to fit the step's size. Doing it be orehand at the a tor ill streamline work at the constr uction site.

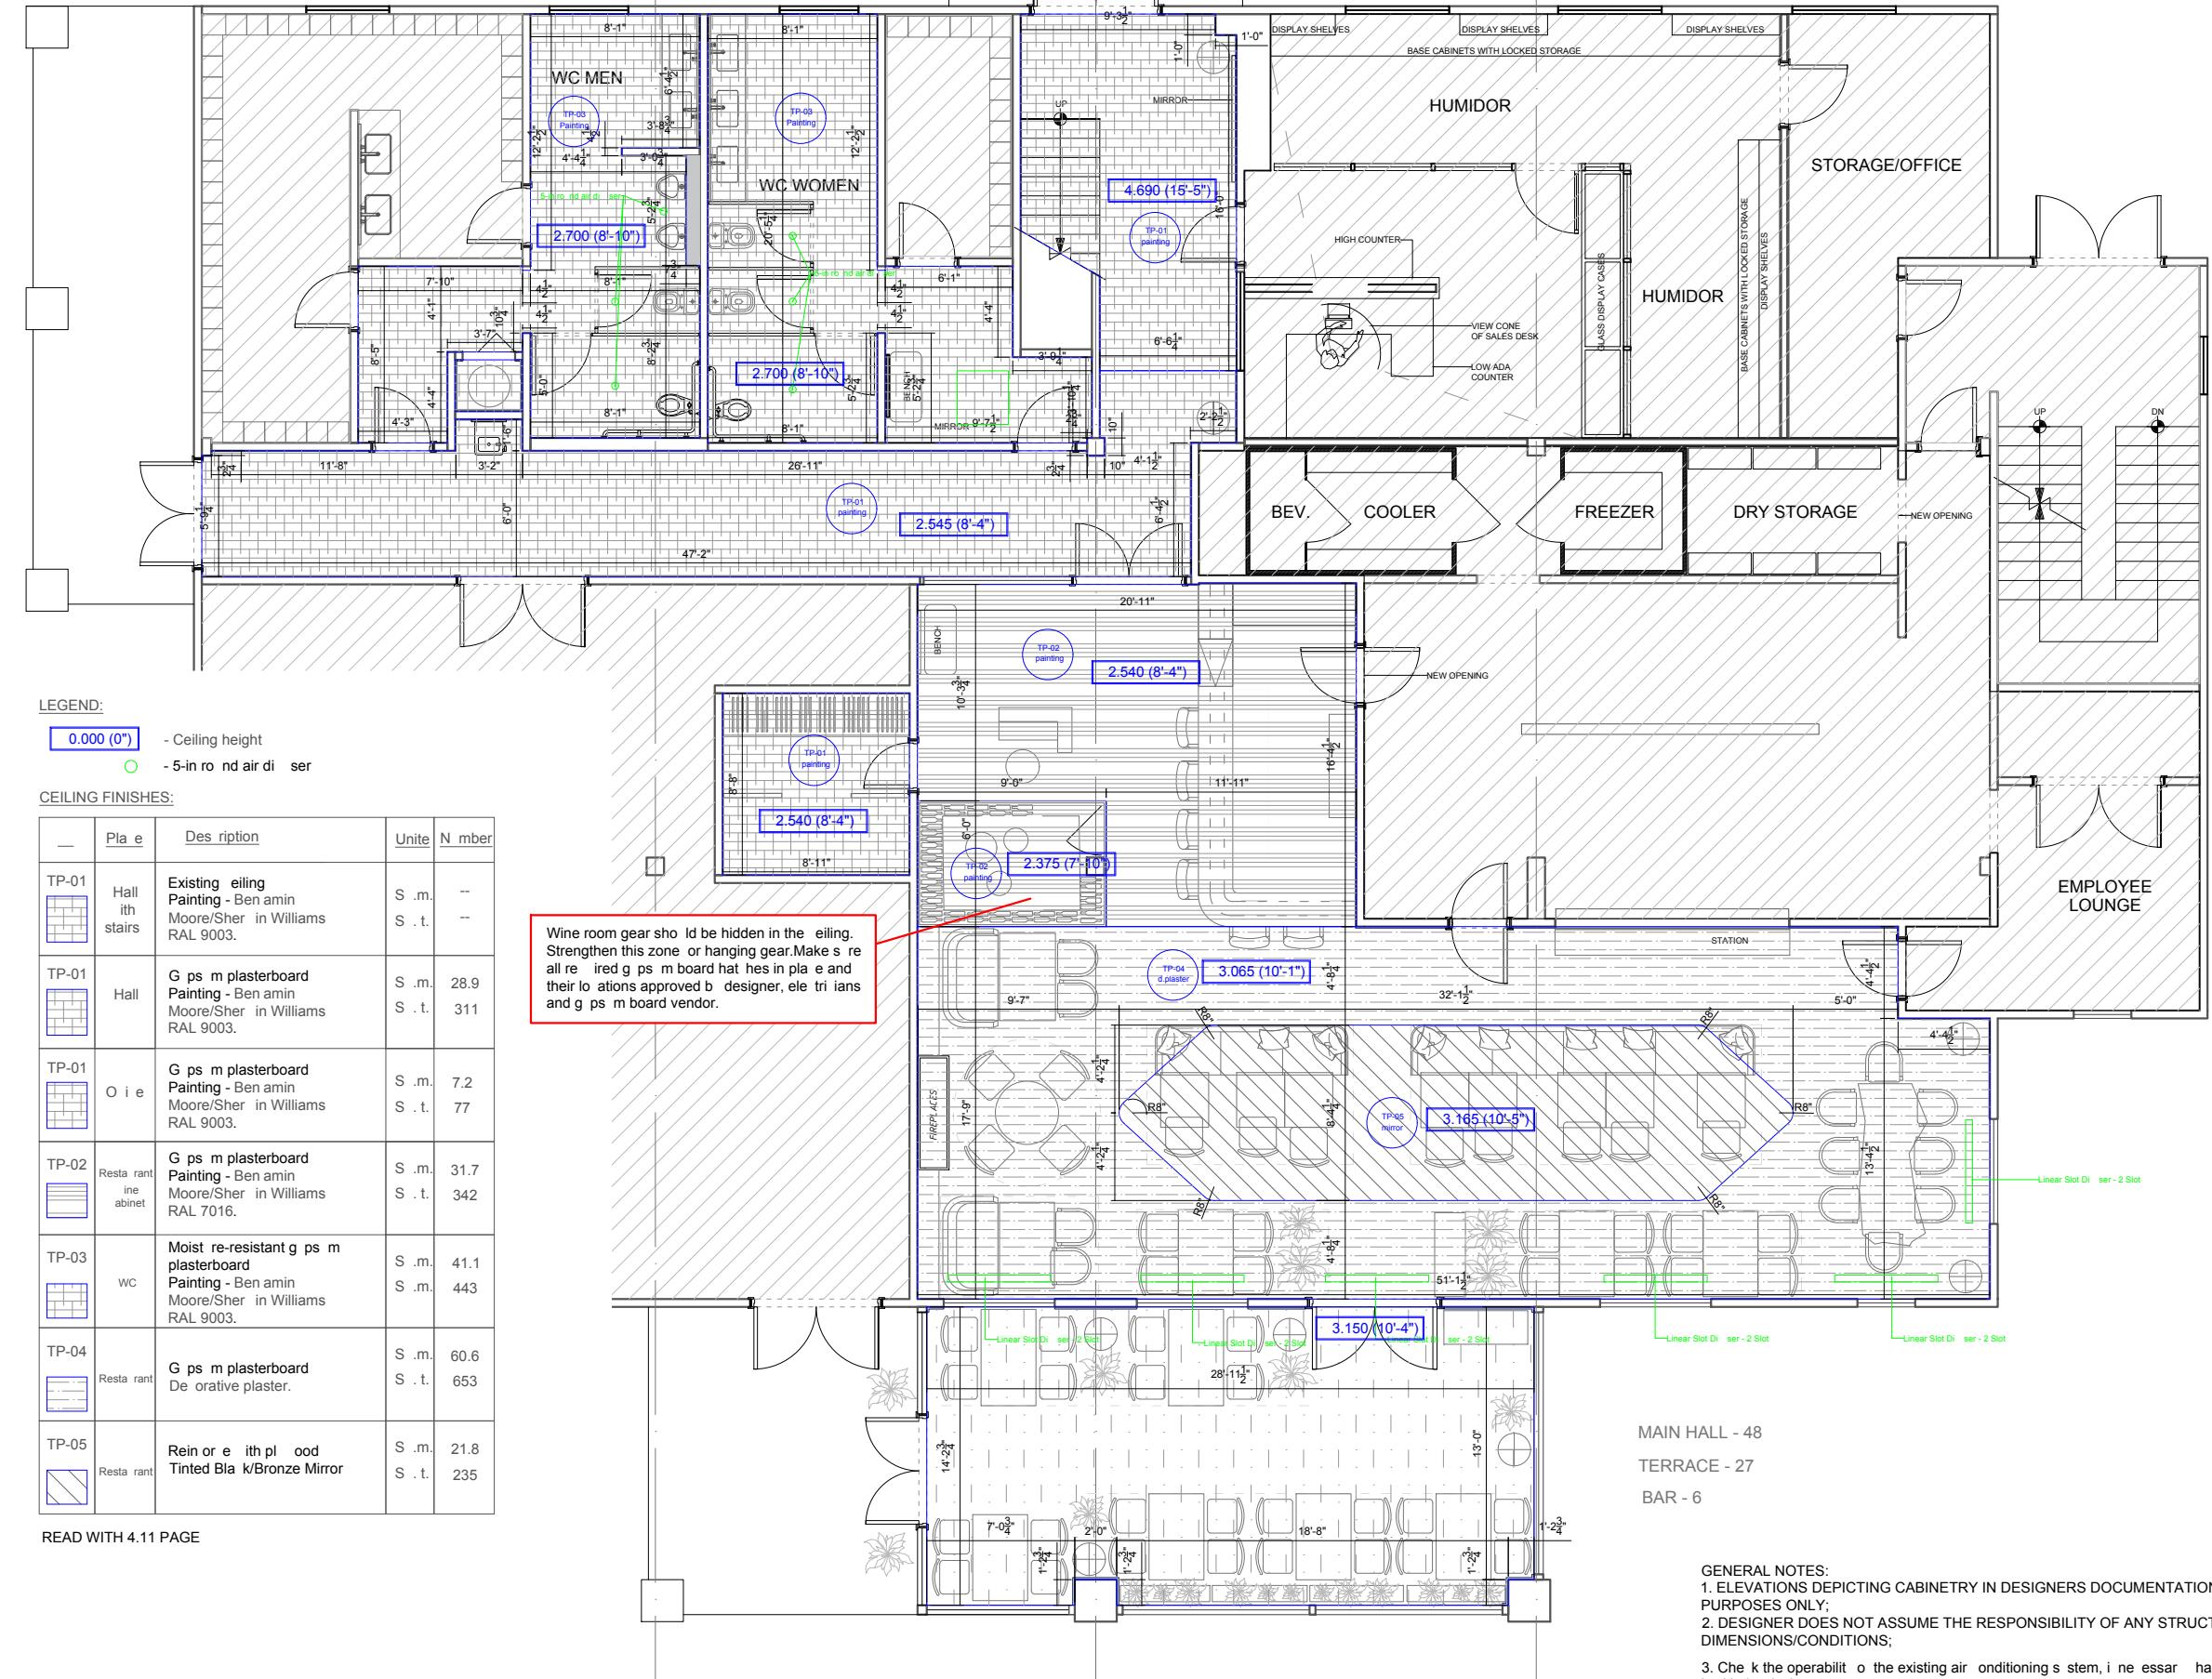

DRAWING TITLE:
**FLOOR PLAN
REFLECTED CEILING**

DRAWN BY: KEIDUNOV IRINA

SCALE: 1/4"=1'-0"

DATE: 03.21.2022

SHEET : 4.4

A1

RESTAURANT OWL'S NEST

DRAWING TITLE:
ELECTRIC LIGHTING LAYOUT


DRAWN BY: KEIDUNOV IRINA

SCALE: 1/4"=1'-0"

DATE: 03.21.2022

SHEET : 4.5

A1

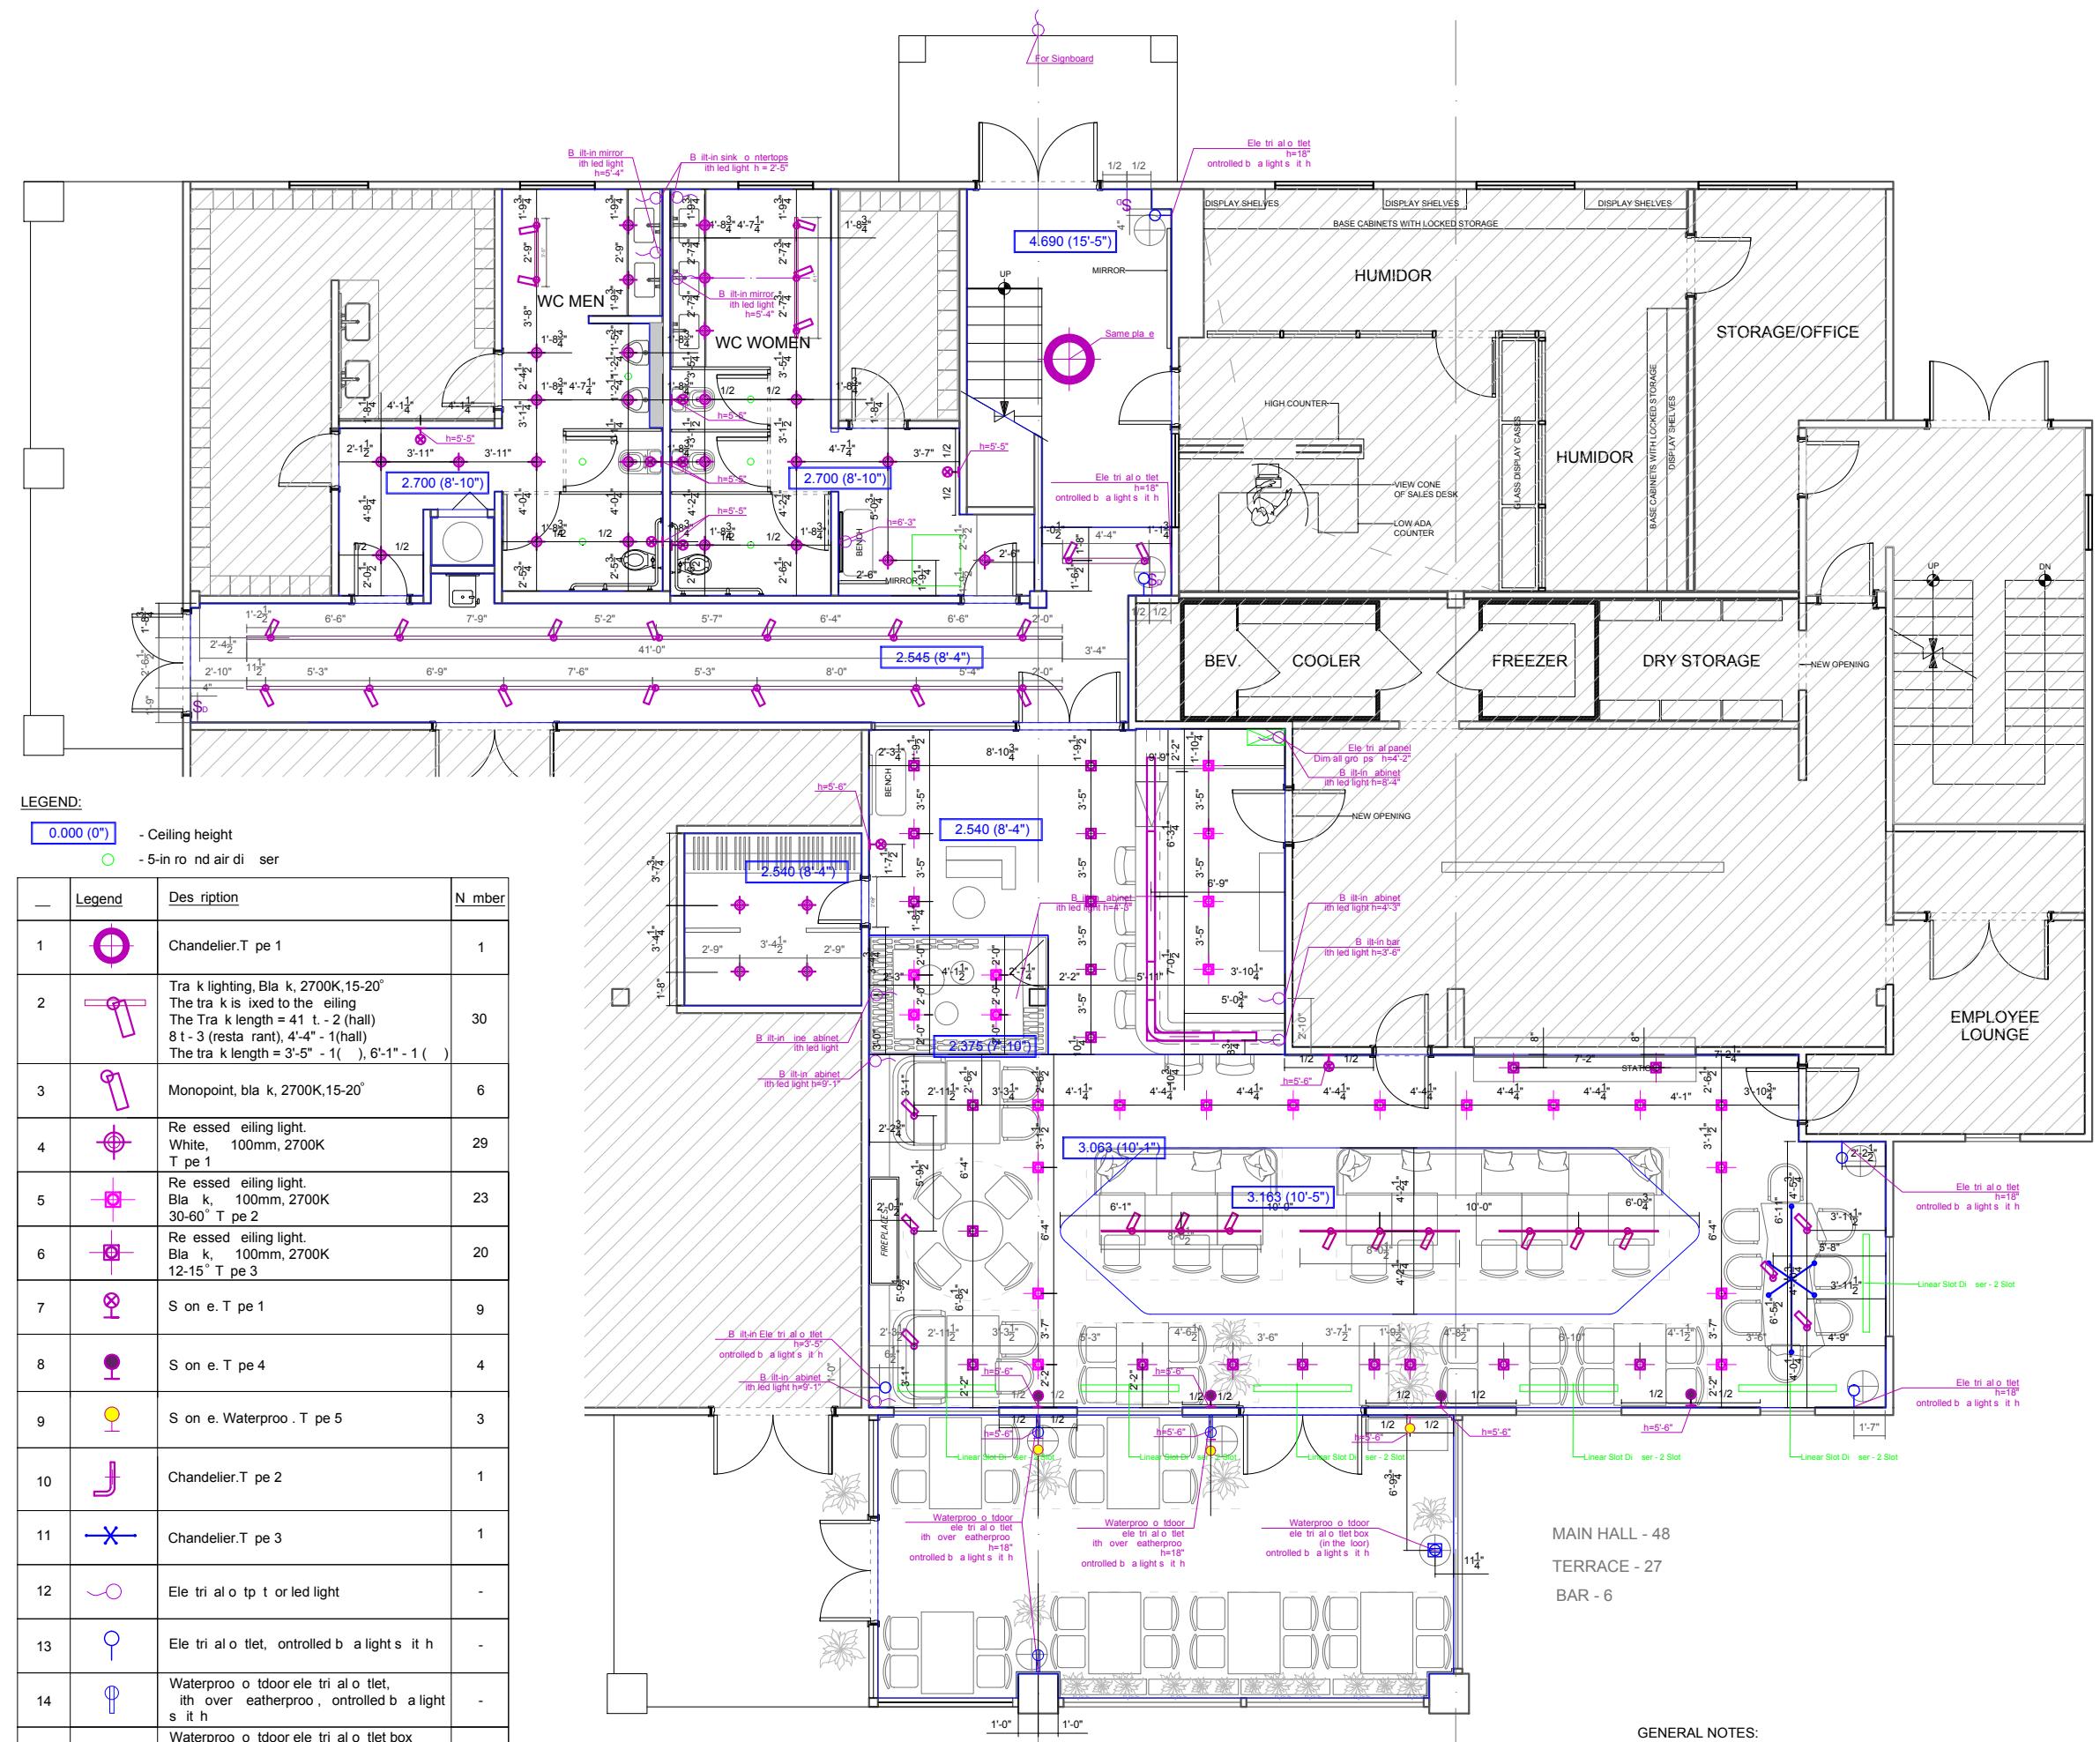

GENERAL NOTES:


1. ELEVATIONS DEPICTING CABINETRY IN DESIGNERS DOCUMENTATION IS FOR DESIGN PURPOSES ONLY;
2. DESIGNER DOES NOT ASSUME THE RESPONSIBILITY OF ANY STRUCTURAL OR FIELD DIMENSIONS/CONDITIONS;
3. All lighting groups must be dimmable;
4. All electrical outlets and switches and other visible electrical stems, cables and equipment must be black (painted black);
5. Look this page with page 10 and 11.

RESTAURANT OWL'S NEST

LEGEND:

- 0.000 (0') - Ceiling height
- 5-in round air diffuser

	Legend	Description	Number
1		Chandelier.T pe 1	1
2		Track lighting, Black, 2700K, 15-20° The track is fixed to the ceiling. The track length = 41 ft - 2 (hall) 8 ft - 3 (restaurant), 4'4" - 1(hall) The track length = 3'-5" - 1(), 6'-1" - 1()	30
3		Monopoint, black, 2700K, 15-20°	6
4		Recessed ceiling light. White, 100mm, 2700K T pe 1	29
5		Recessed ceiling light. Black, 100mm, 2700K 30-60° T pe 2	23
6		Recessed ceiling light. Black, 100mm, 2700K 12-15° T pe 3	20
7		Sconce. T pe 1	9
8		Sconce. T pe 4	4
9		Sconce. Waterproof. T pe 5	3
10		Chandelier.T pe 2	1
11		Chandelier.T pe 3	1
12		Electrical outlet with led light	-
13		Electrical outlet, controlled by a light switch	-
14		Waterproof door electrical outlet, with overatherproof, controlled by a light switch	-
15		Waterproof door electrical outlet box (in the floor) controlled by a light switch	-
16		Switch (dim)	-

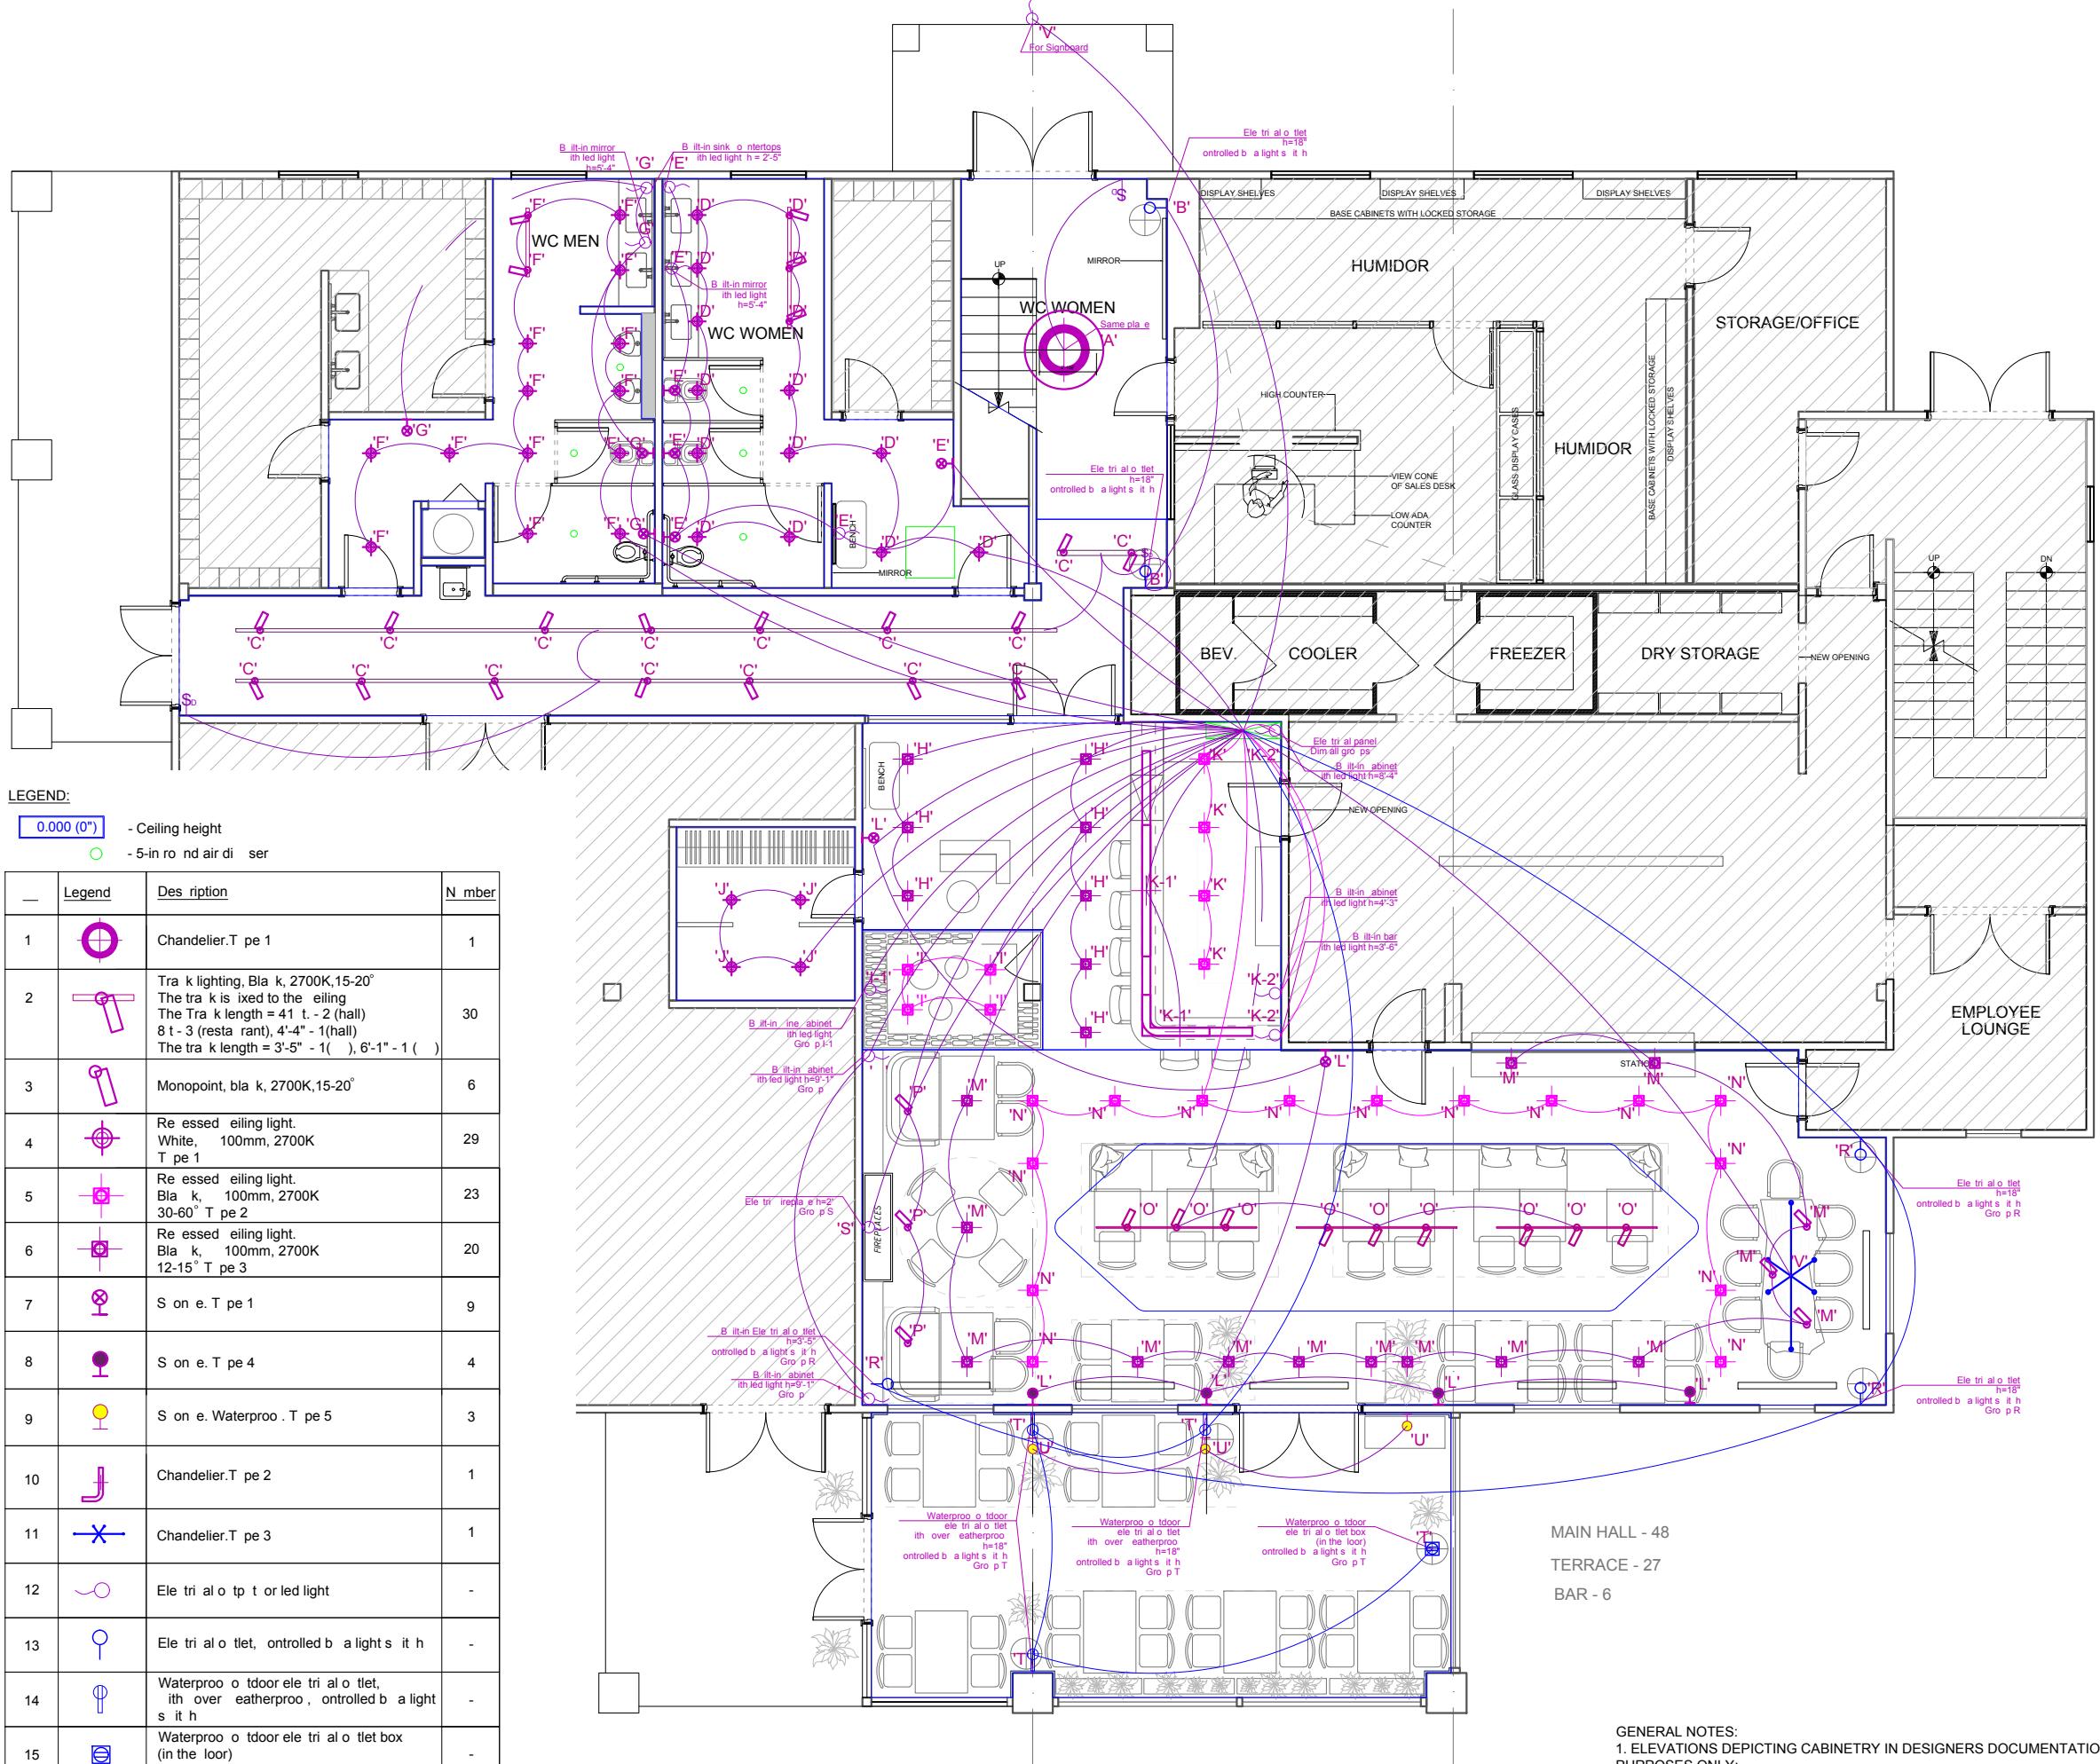

MAIN HALL - 48
TERRACE - 27
BAR - 6

GENERAL NOTES:
 1. ELEVATIONS DEPICTING CABINETRY IN DESIGNERS DOCUMENTATION IS FOR DESIGN PURPOSES ONLY;
 2. DESIGNER DOES NOT ASSUME THE RESPONSIBILITY OF ANY STRUCTURAL OR FIELD DIMENSIONS/CONDITIONS;
 3. All lightning groups must be dimmable;
 4. All electrical outlets and switches and other visible electrical stems, cables, stems and etc. must be black (painted black);
 5. Look this page with page 9 and 11.


DRAWING TITLE:
ELECTRIC SWITCHES LAYOUT

DRAWN BY: KEIDUNOV IRINA

SCALE: 1/4"=1'-0"

DATE: 03.21.2022

SHEET : 4.6

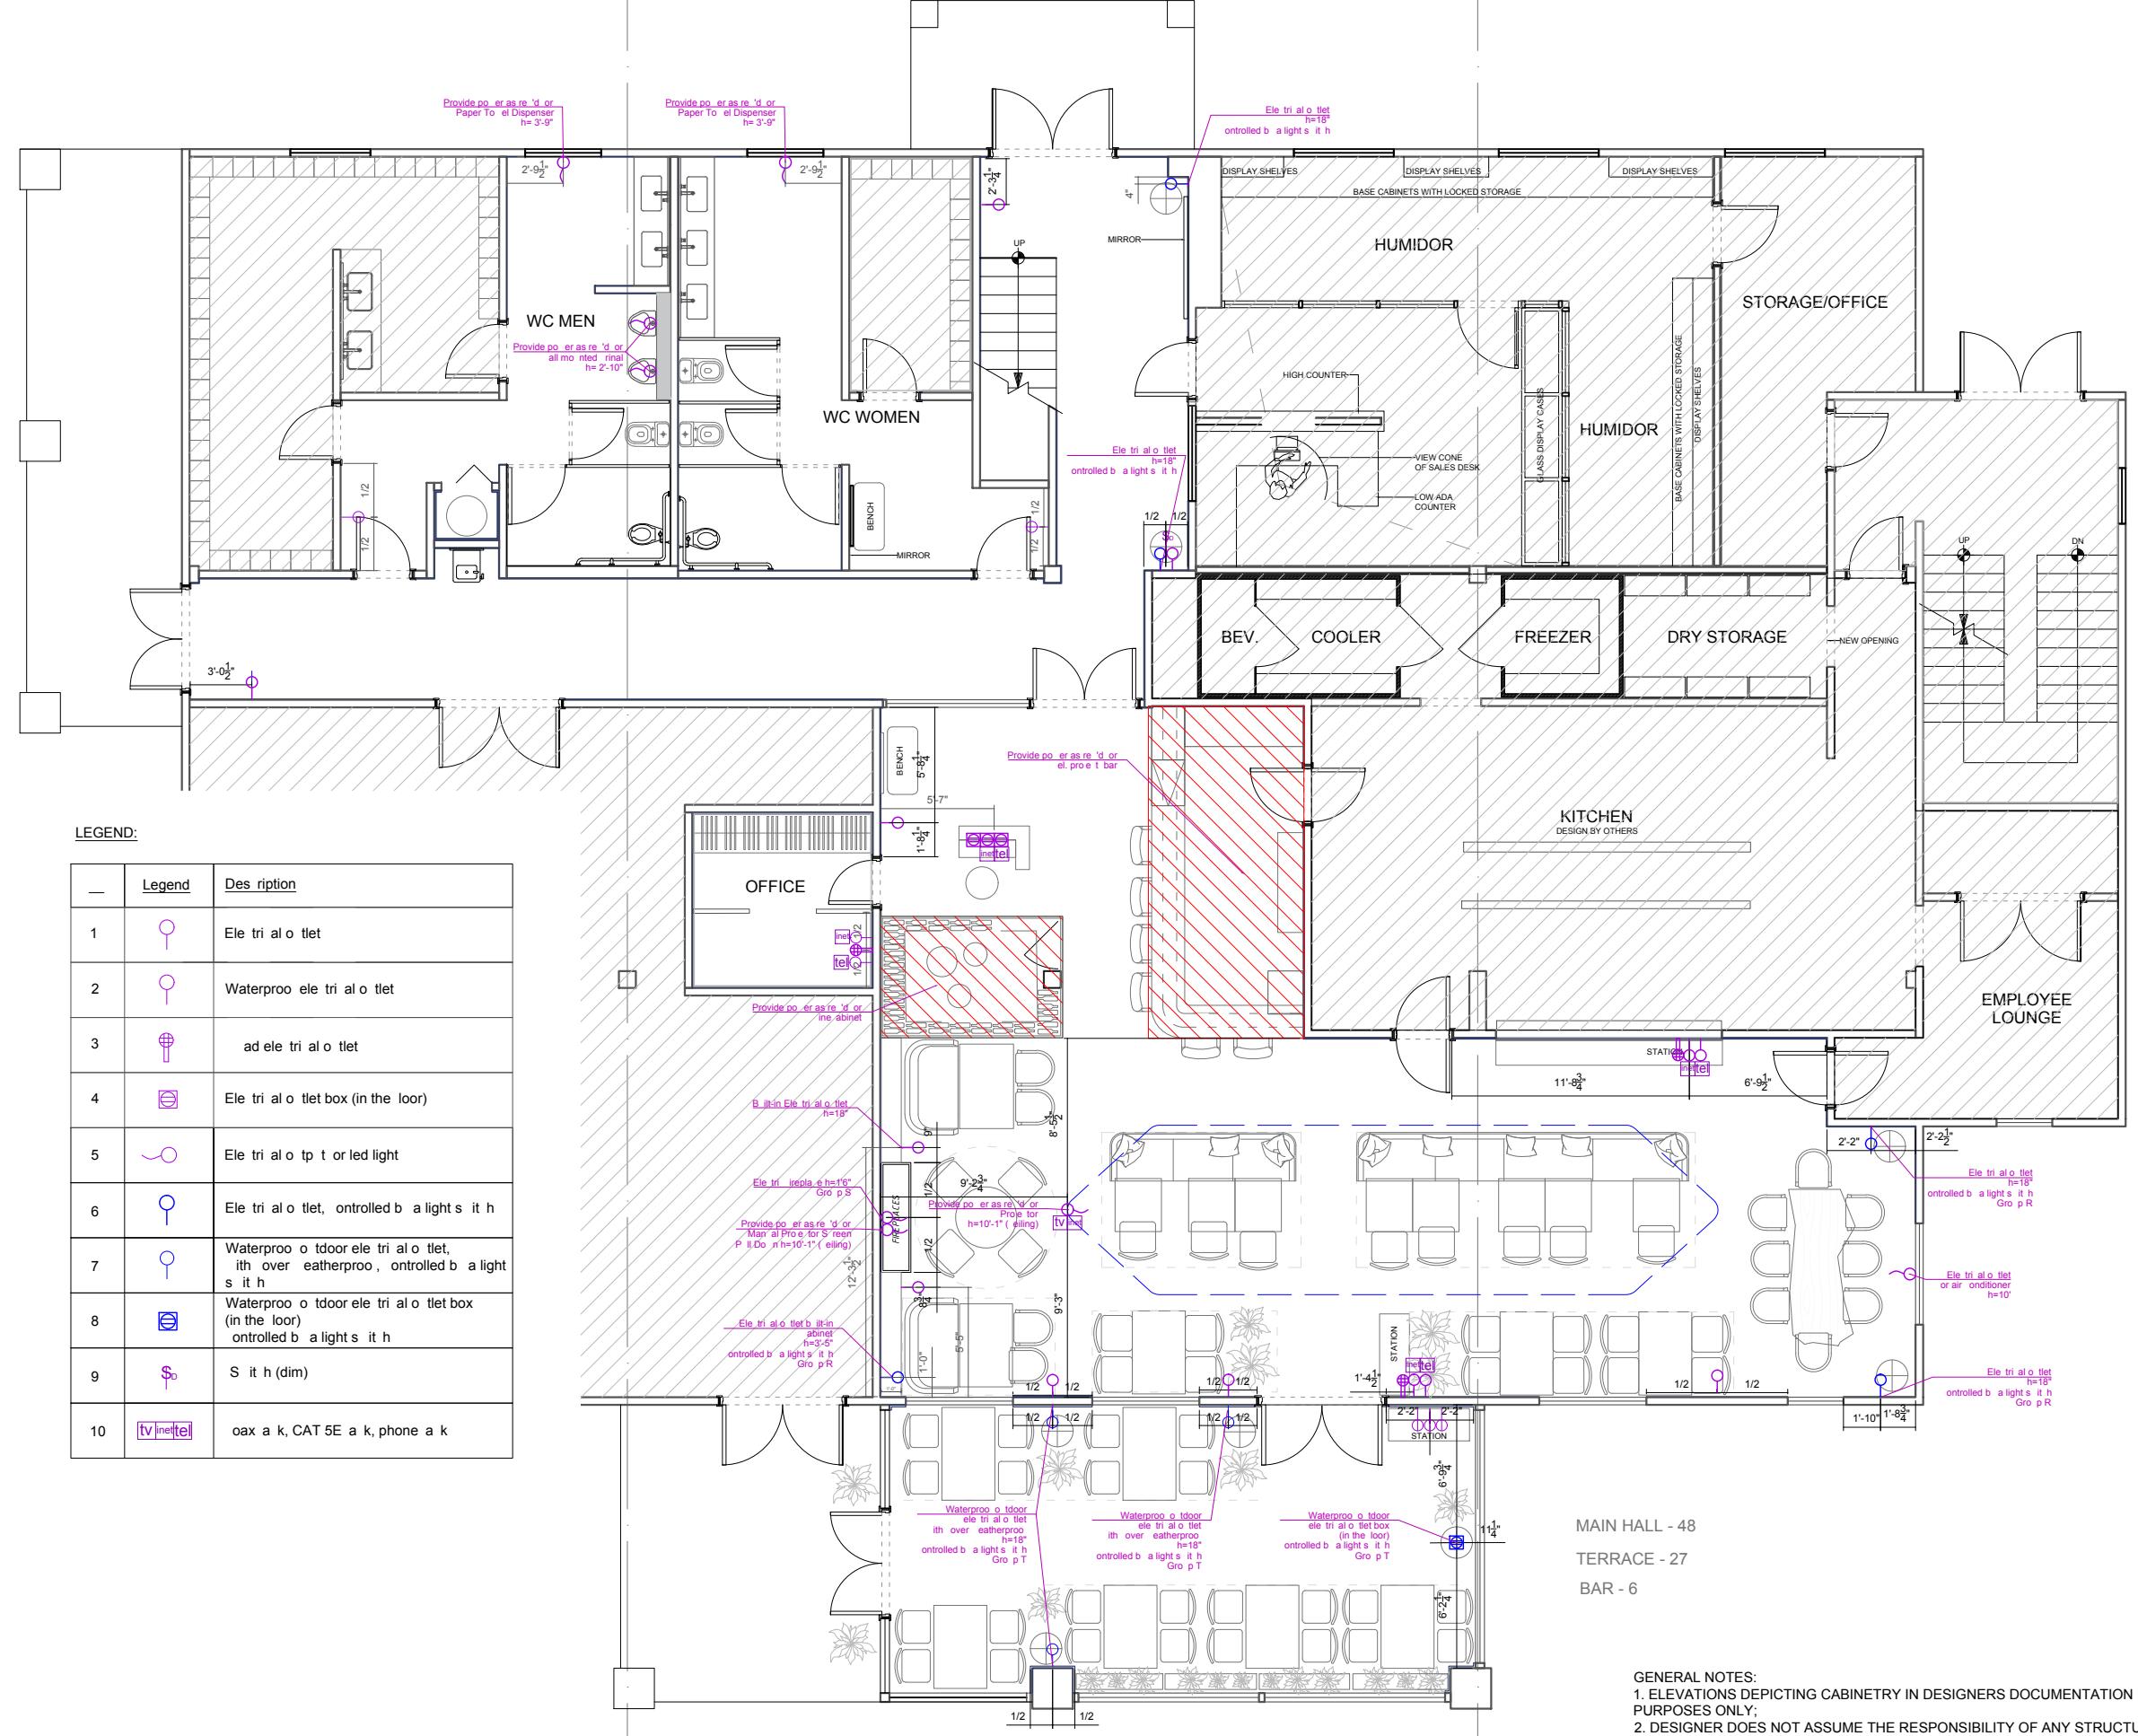

RESTAURANT
OWL'S NEST

DRAWING TITLE:
ELECTRICAL OUTLET LAYOUT

DRAWN BY: KEIDUNOV IRINA


SCALE: 1/4"=1'-0"

DATE: 03.21.2022

SHEET : 4.7

A1

RESTAURANT OWL'S NEST

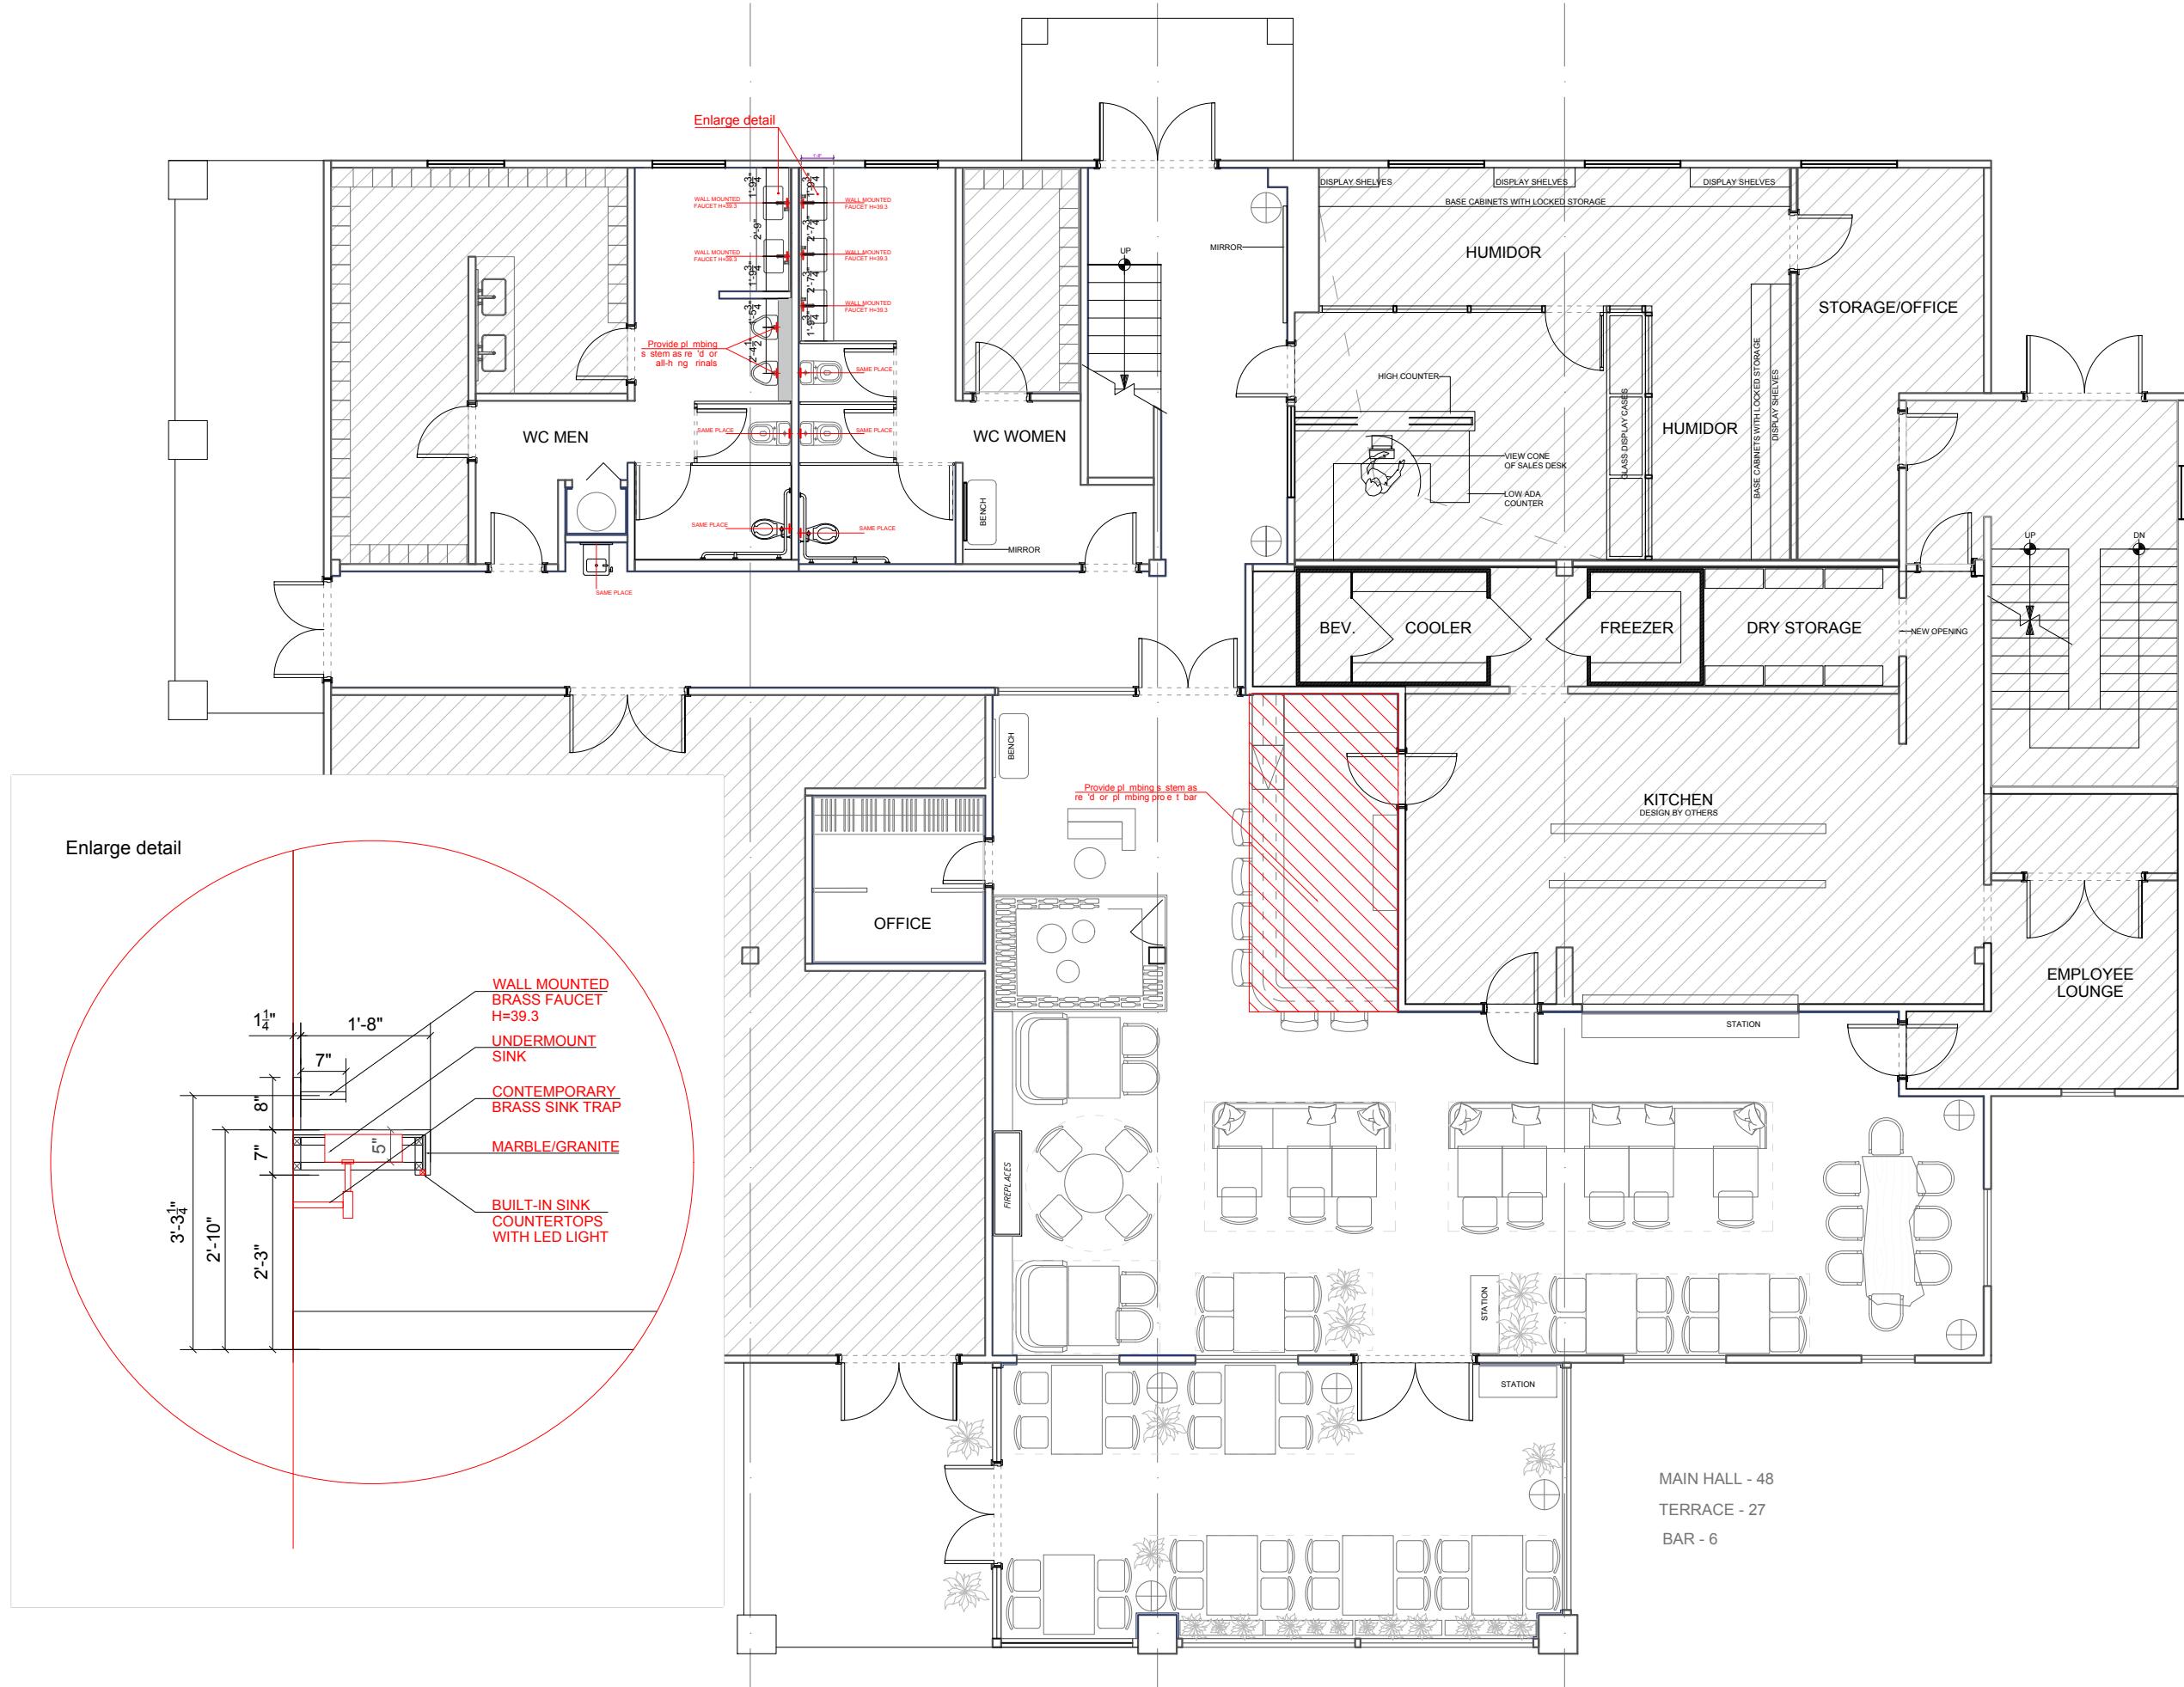

DRAWING TITLE:
PLUMBING LAYOUT


DRAWN BY: KEIDUNOV IRINA

SCALE: 1/4"=1'-0"

DATE: 03.21.2022

SHEET : 4.8

A1

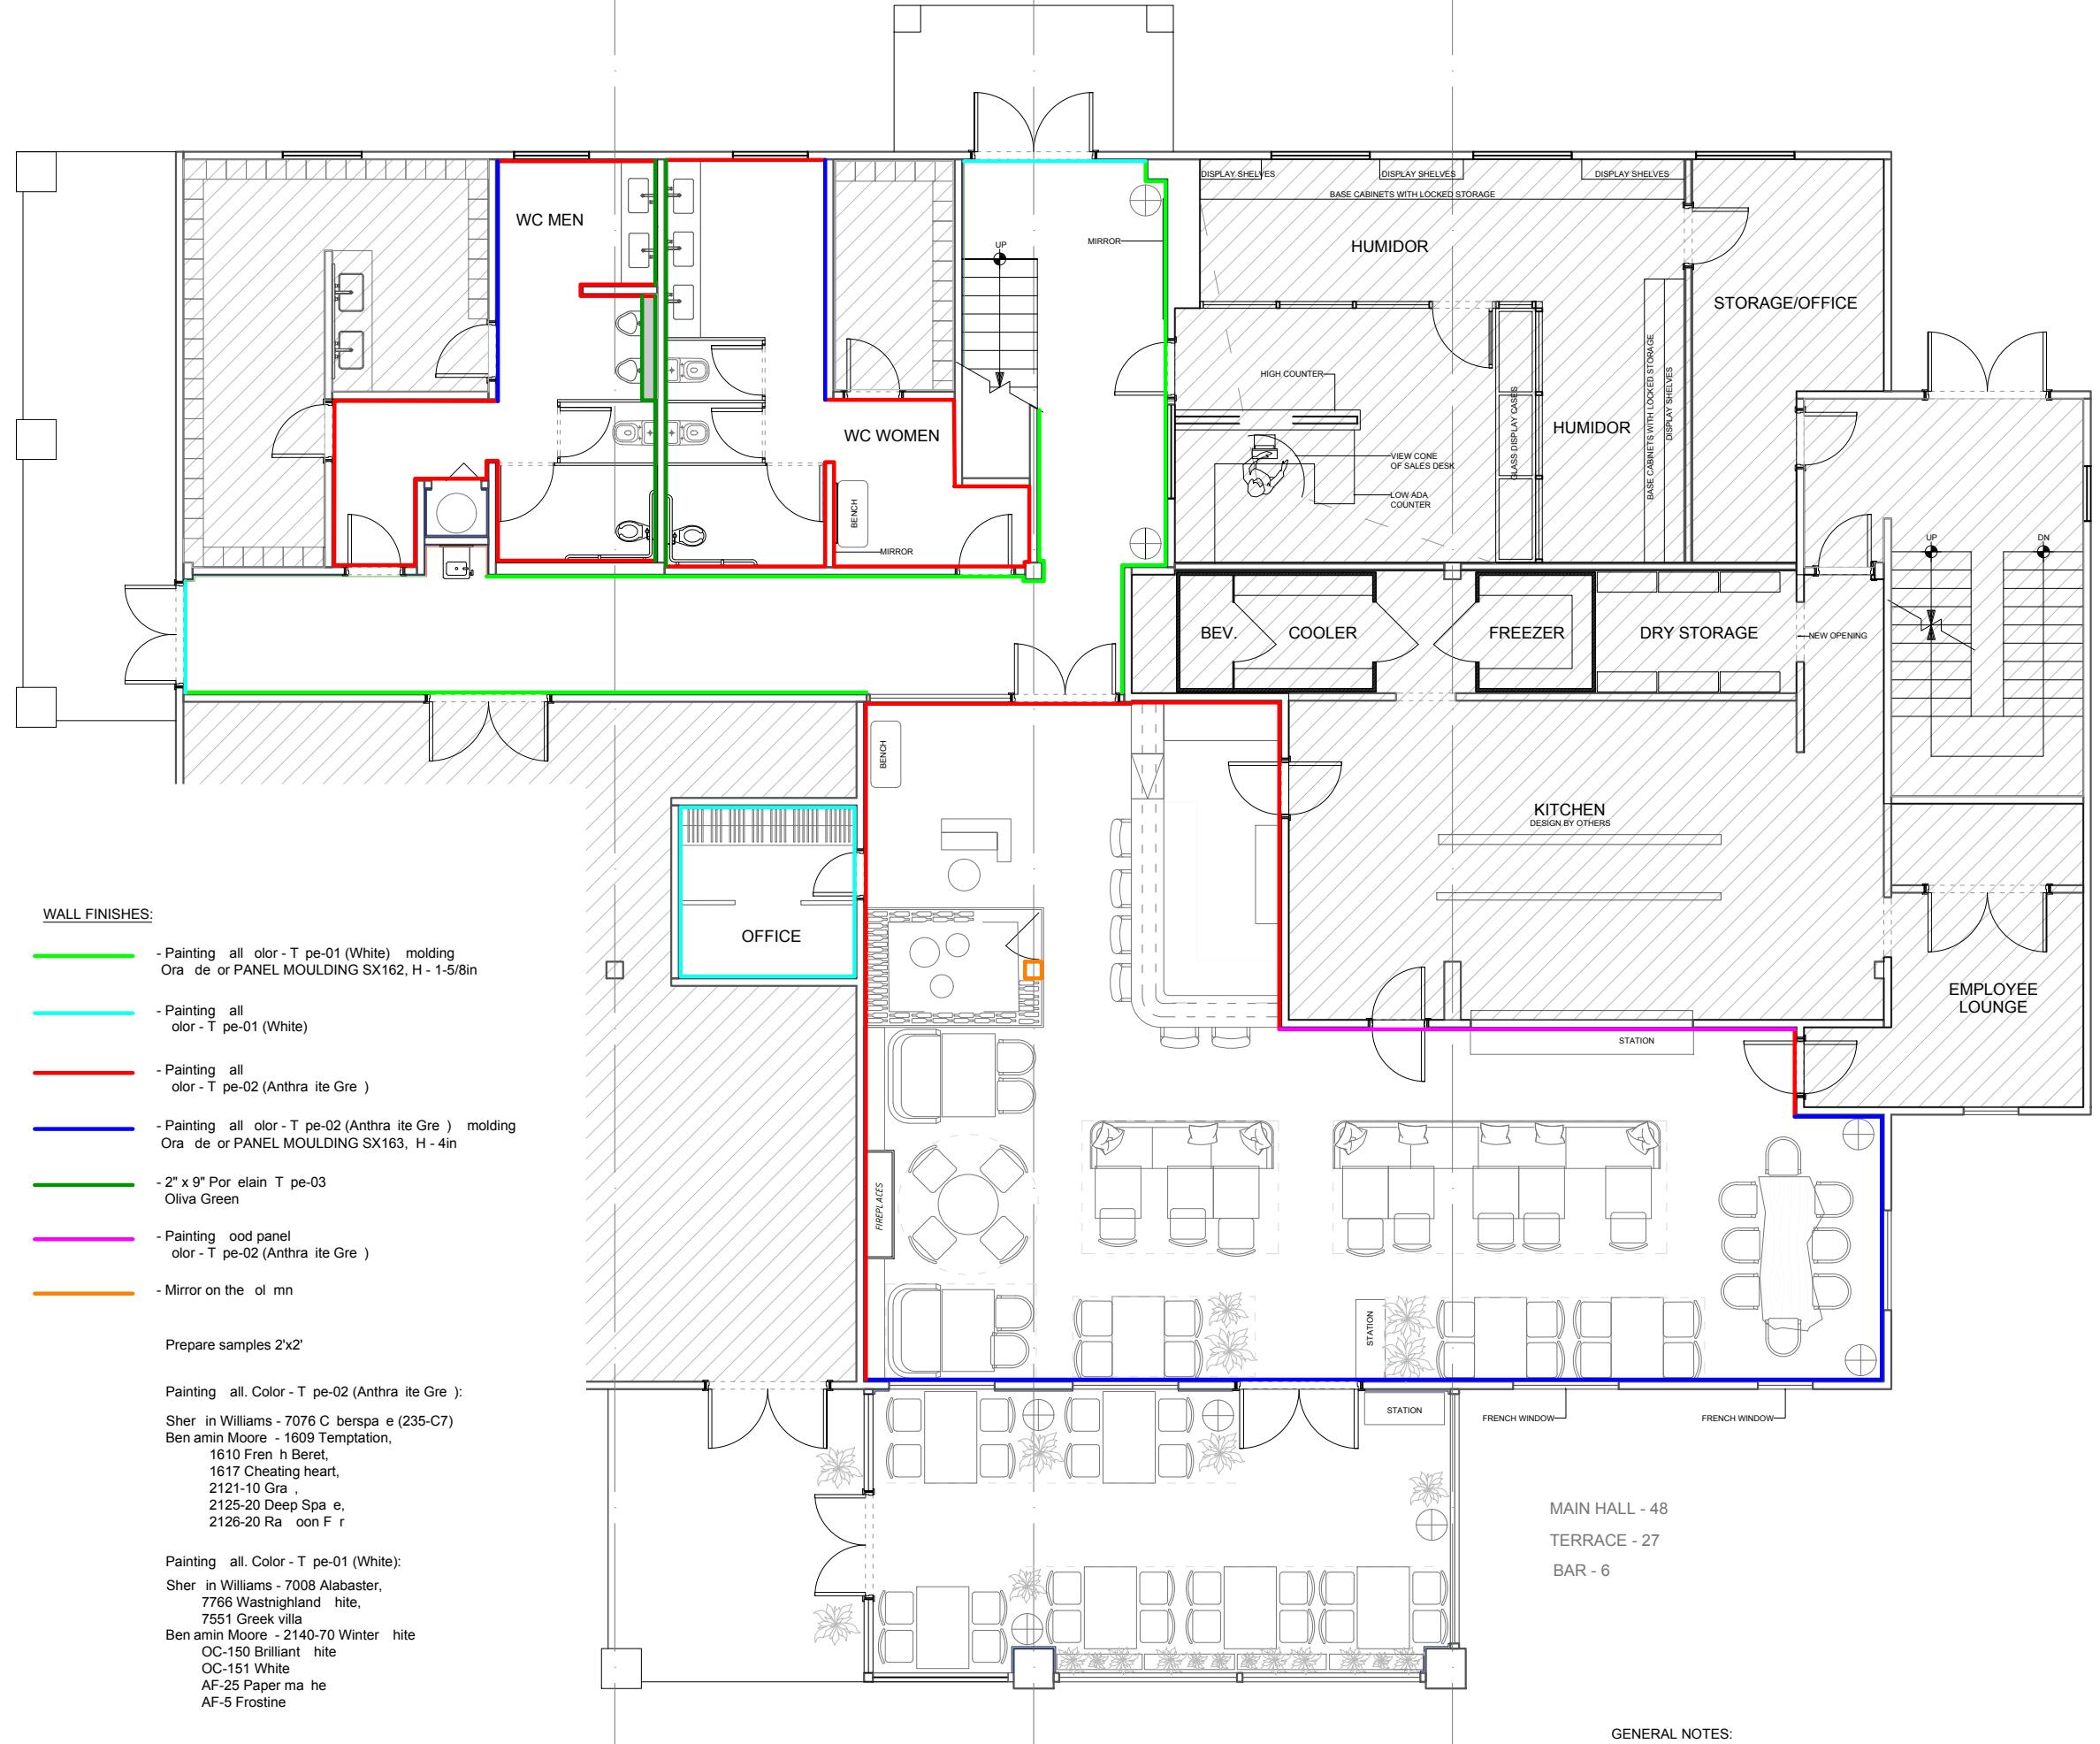

DRAWING TITLE:
WALL FINISHES LAYOUT

DRAWN BY: KEIDUNOV IRINA

SCALE: 1/4"=1'-0"

DATE: 03.21.2022

SHEET : 4.9

A1

FLOOR FINISHES:

	<u>Code</u>	<u>Pla_e</u>	<u>Des ription</u>	<u>Pi_t re</u>	<u>Unite</u>	<u>N_mber</u>
1	F-01	Hall oman men bar ine abinet	Title. Por elain stone are/Slate. Bla_k. 18"x36"		S .m. S .t.	97.5 1044.1
2	F-02	Oie Resta rant	Wood/Engineered Hard ood Flooring		S .m. S .t.	107.65 2195.8
3	F-03	Terra e	Wood De king		S .m. S .t.	38.10 409.00

WALL FINISHES:

	<u>Code</u>	<u>Pla_e</u>	<u>Des ription</u>	<u>Pi_t re</u>	<u>Unite</u>	<u>N_mber</u>
1	T pe-01	Hall Oie	Painting all (hite) (In the hall painting molding)		S .m. S .t.	148.7 1601
2	T pe-02	Resta rant WC	Painting all (Anthra cite Gre) painting molding		S .m. S .t.	220.9 2378
3	T pe-03	WC	2" x 9" Por elain - Oliva Green		S .m. S .t.	33.4 360

CEILING FINISHES:

	<u>Code</u>	<u>Pla_e</u>	<u>Des ription</u>	<u>Pi_t re</u>	<u>Unite</u>	<u>N_mber</u>
1	TP-01	Hall ith stairs Hall Oie	Existing eiling Painting - Ben amin Moore RAL 9016.		S .m. S .t.	approx. 50 approx. 542
2	TP-02	Wine abinet Resta rant	G ps m plasterboard Painting - Ben amin Moore RAL 7016.		S .m. S .t.	31.7 342
3	TP-03	WC	Moist re-resistant g ps m plasterboard Painting - Ben amin Moore RAL 9016.		S .m. S .t.	41.1 443
4	TP-04	Resta rant	G ps m plasterboard De orative plaster- Con rete.		S .m. S .t.	60.6 653
5	TP-05	Resta rant	Rein ore ith pl ood Tinted Bla_k/Bronze Mirror		S .m. S .t.	21.8 235

BASEBOARD MOLDING:

	<u>Code</u>	<u>Pla_e</u>	<u>Des ription</u>	<u>Pi_t re</u>	<u>N_mber</u>
1	_____	Hall Oie	High Impa t Pol st rene Baseboard Mo lding Ora De or SX168 Painting T pe-01 (White) 5-7/8in H x 78-3/4in Long		150' -11"
2	_____	Resta rant WC	High Impa t Pol st rene Baseboard Mo lding Ora De or SX168 Painting T pe-02 (Anthra cite Gre) 5-7/8in H x 78-3/4in Long		202' -2"

PANEL MOLDING:

	<u>Code</u>	<u>Pla_e</u>	<u>Des ription</u>	<u>Pi_t re</u>	<u>N_mber</u>
1	_____	Hall	PANEL MOULDING SX162 Ora De or High Impa t Pol st rene Baseboard Mo lding Primed White 1-5/8in H x 78in Long		approx 412'-1"
2	_____	Resta rant WC	PANEL MOULDING SX163 Ora De or High Impa t Pol st rene Baseboard Mo lding Primed White 4in H x 78in Long		approx 321'-8"

Prepare samples 2'x2'

Painting all. Color - T pe-01 (White):
Sher in Williams - 7008 Alabaster,
7766 Wastnighland hite,
7551 Greek villa
Ben amin Moore - 2140-70 Winter hite
OC-150 Brilliant hite
OC-151 White
AF-25 Paper ma he
AF-5 Frostine

Painting all. Color - T pe-02 (Anthra cite Gre):
Sher in Williams - 7076 C berspa e (235-C7)
Ben amin Moore - 1609 Temptation,
1610 Fren h Beret,
1617 Cheating heart,
2121-10 Gra ,
2125-20 Deep Spa e,
2126-20 Ra oon F r

GENERAL NOTES:
1. ELEVATIONS DEPICTING CABINERY IN DESIGNERS DOCUMENTATION IS FOR DESIGN PURPOSES ONLY;
2. DESIGNER DOES NOT ASSUME THE RESPONSIBILITY OF ANY STRUCTURAL OR FIELD DIMENSIONS/CONDITIONS;
3. All meas res provided ito room.

RESTAURANT
OWL'S NEST

DRAWING TITLE:
WALL, FLOOR,
CEILING FINISHES
LEGEND

DRAWN BY: KEIDUNOV IRINA

SCALE: 1/4"=1'-0"


DATE: 03.21.2022

SHEET : 4.11

A1

RESTAURANT OWL'S NEST

PLAN VARIANT 5

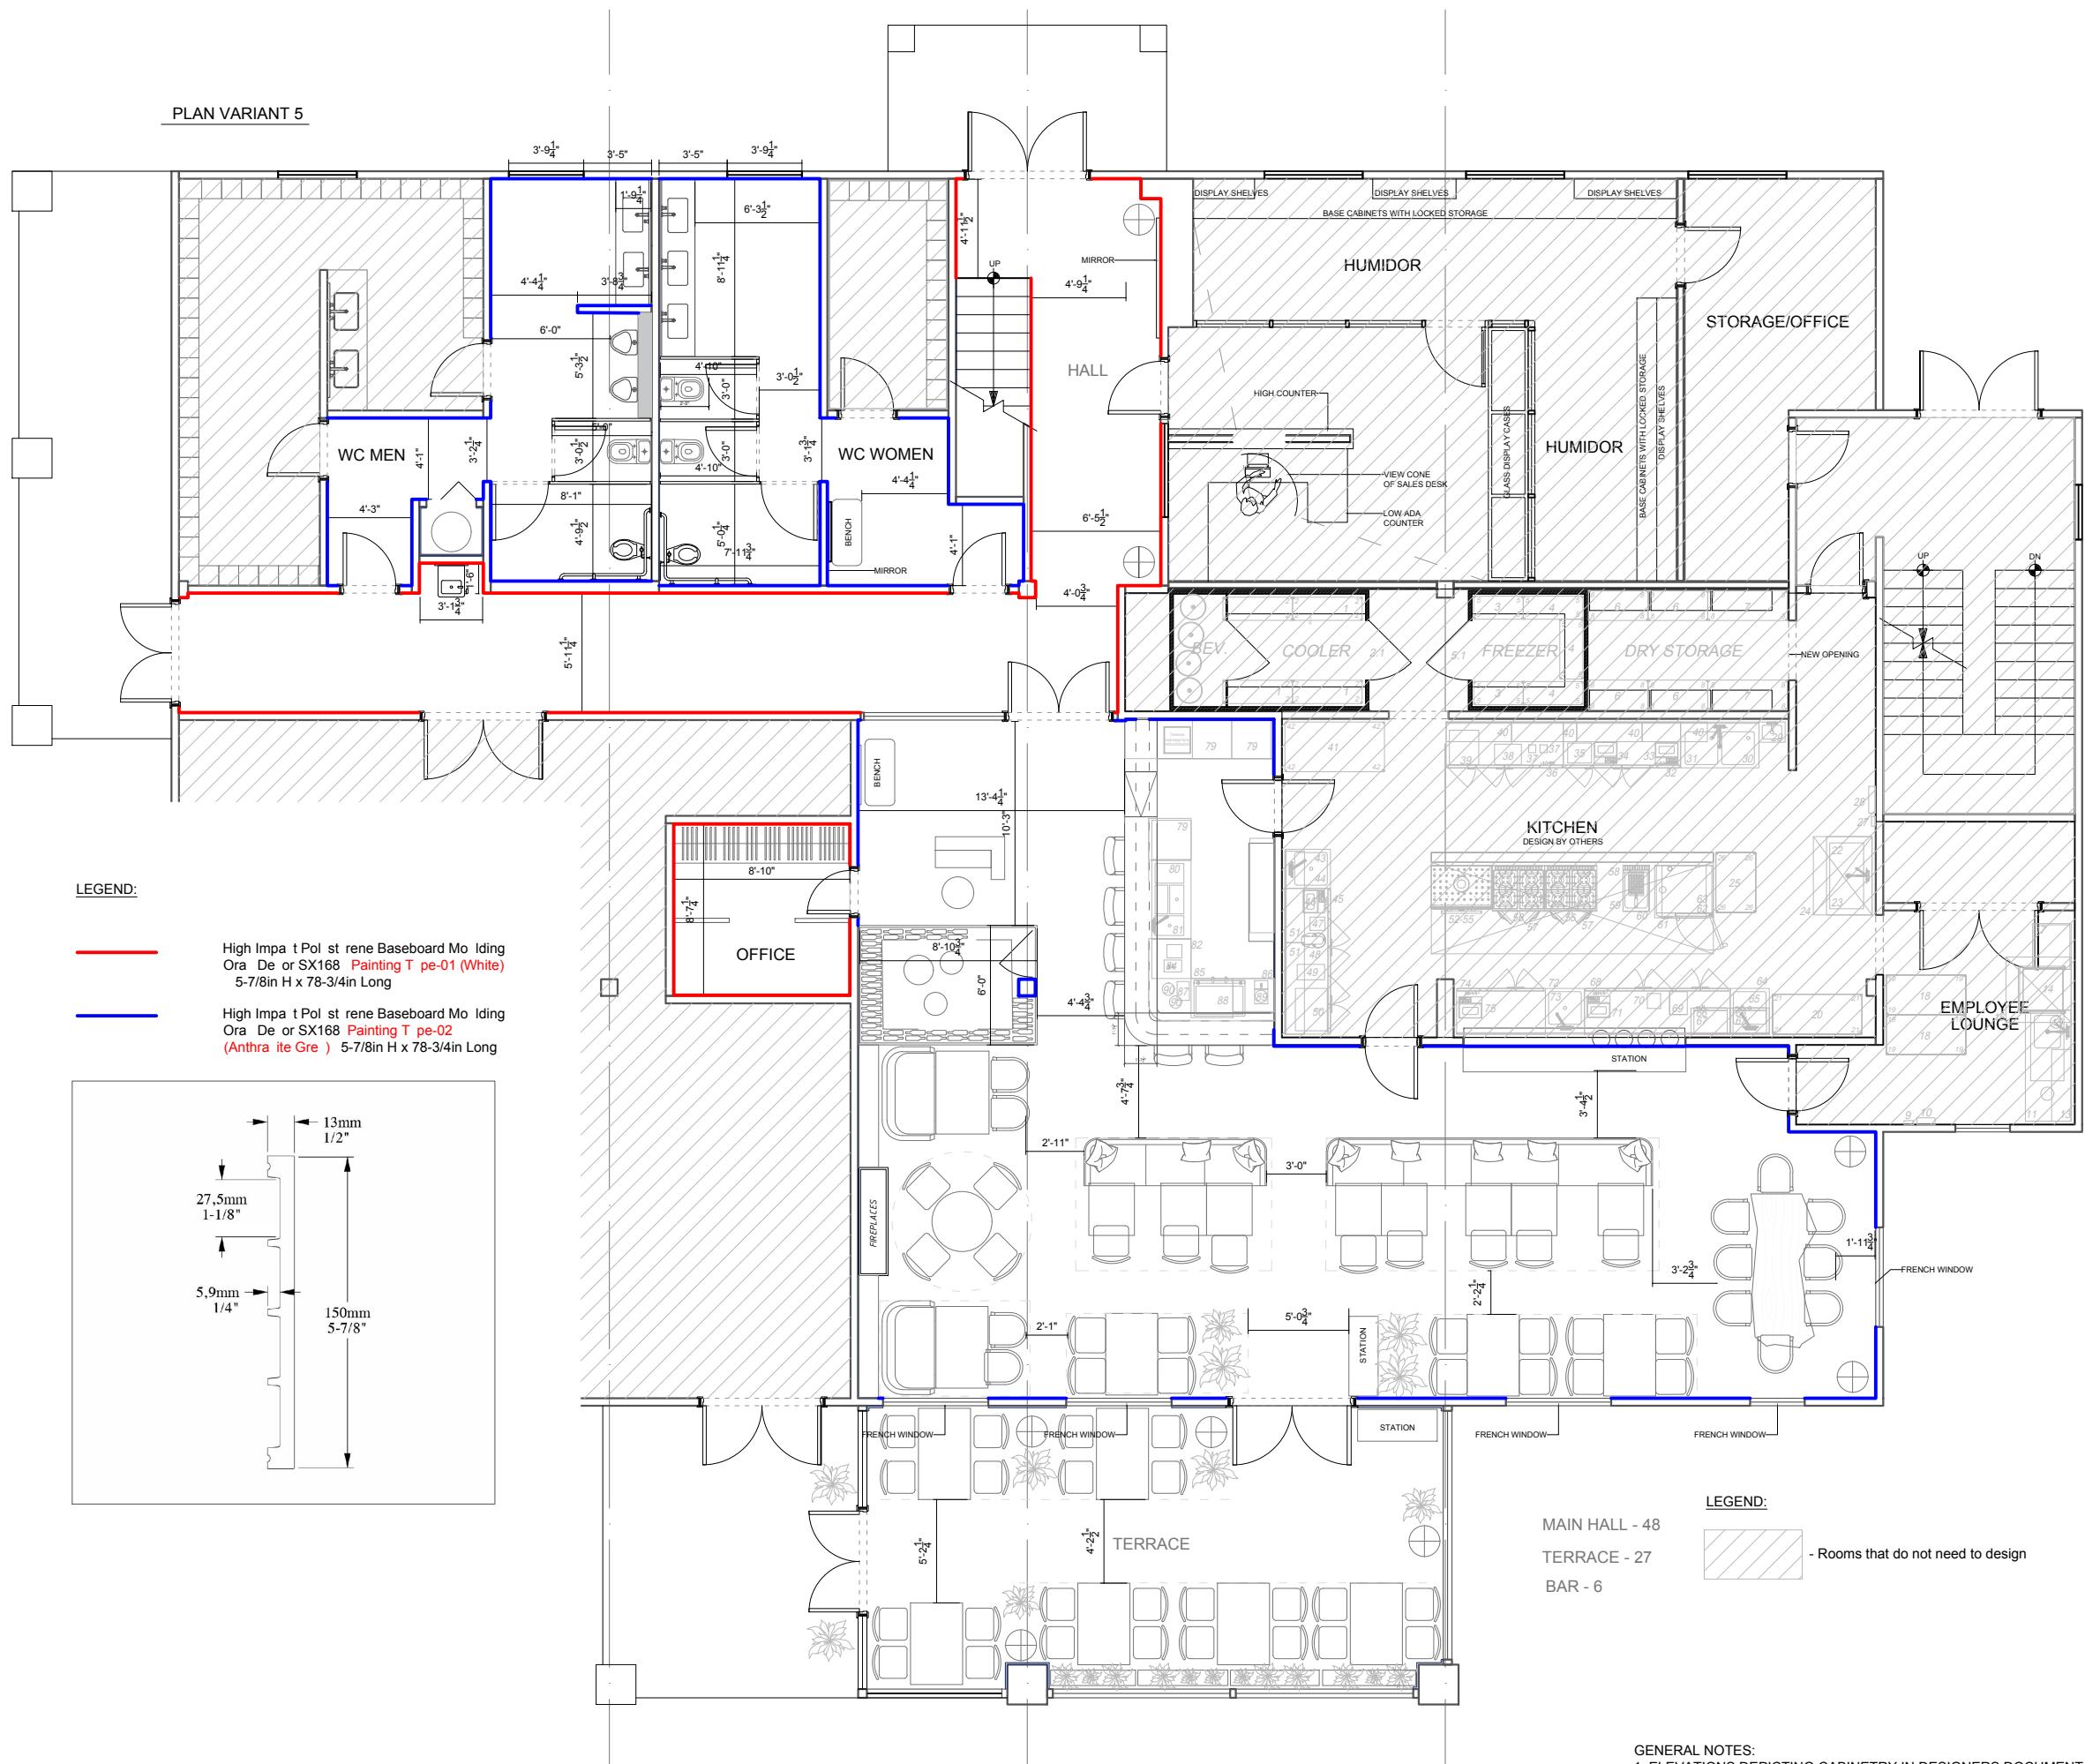

DRAWING TITLE:
BASEBOARD MOLDING LAYOUT

DRAWN BY: KEIDUNOV IRINA


SCALE: 1/4"=1'-0"

DATE: 03.21.2022

SHEET : 4.10

A1

ELEVATIONS DRAWING

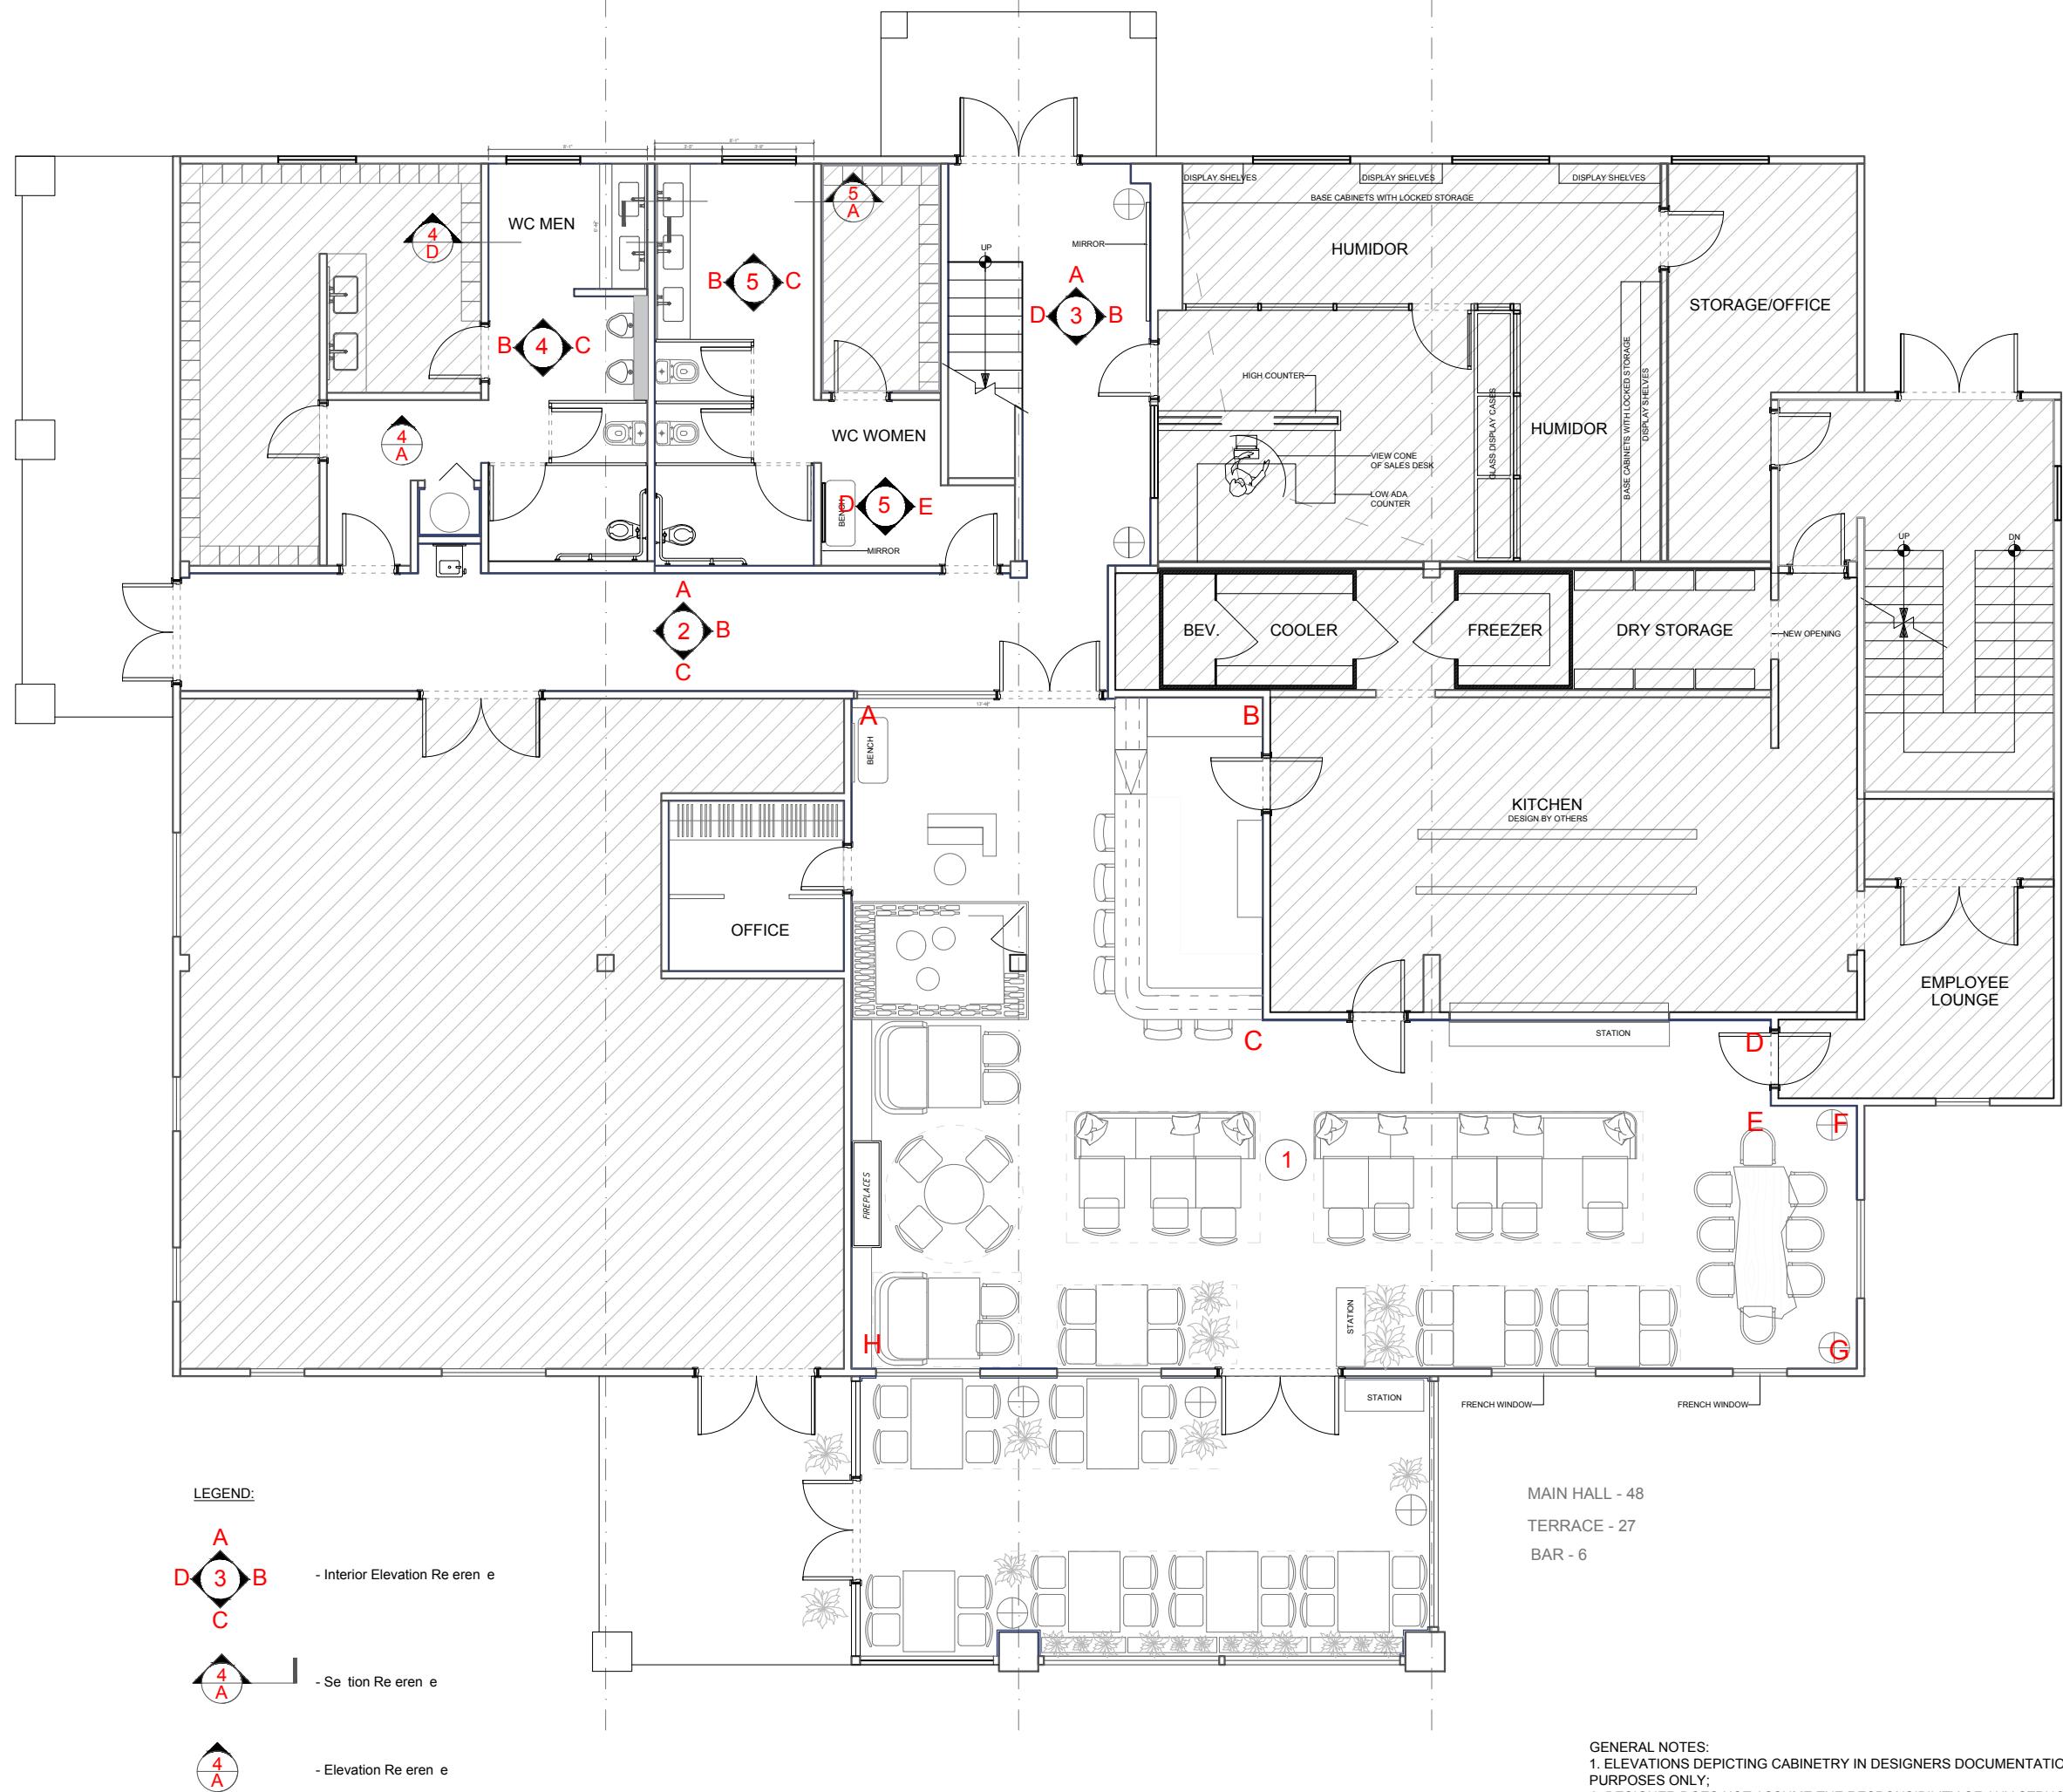

DRAWING TITLE:
REFERENCE LAYOUT

DRAWN BY: KEIDUNOV IRINA




SCALE: 1/4"=1'-0"

DATE: 03.21.2022

SHEET : 5.1

A1

RESTAURANT OWL'S NEST

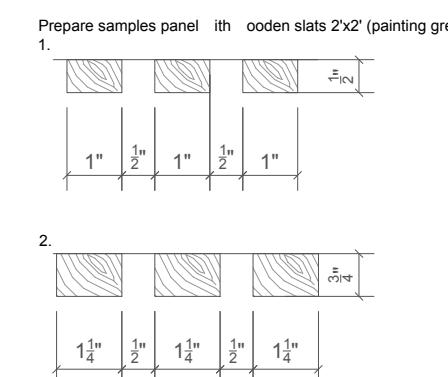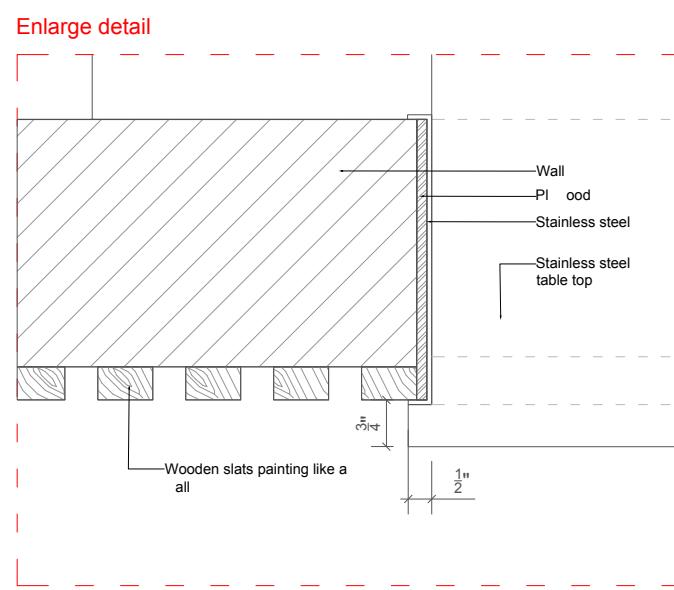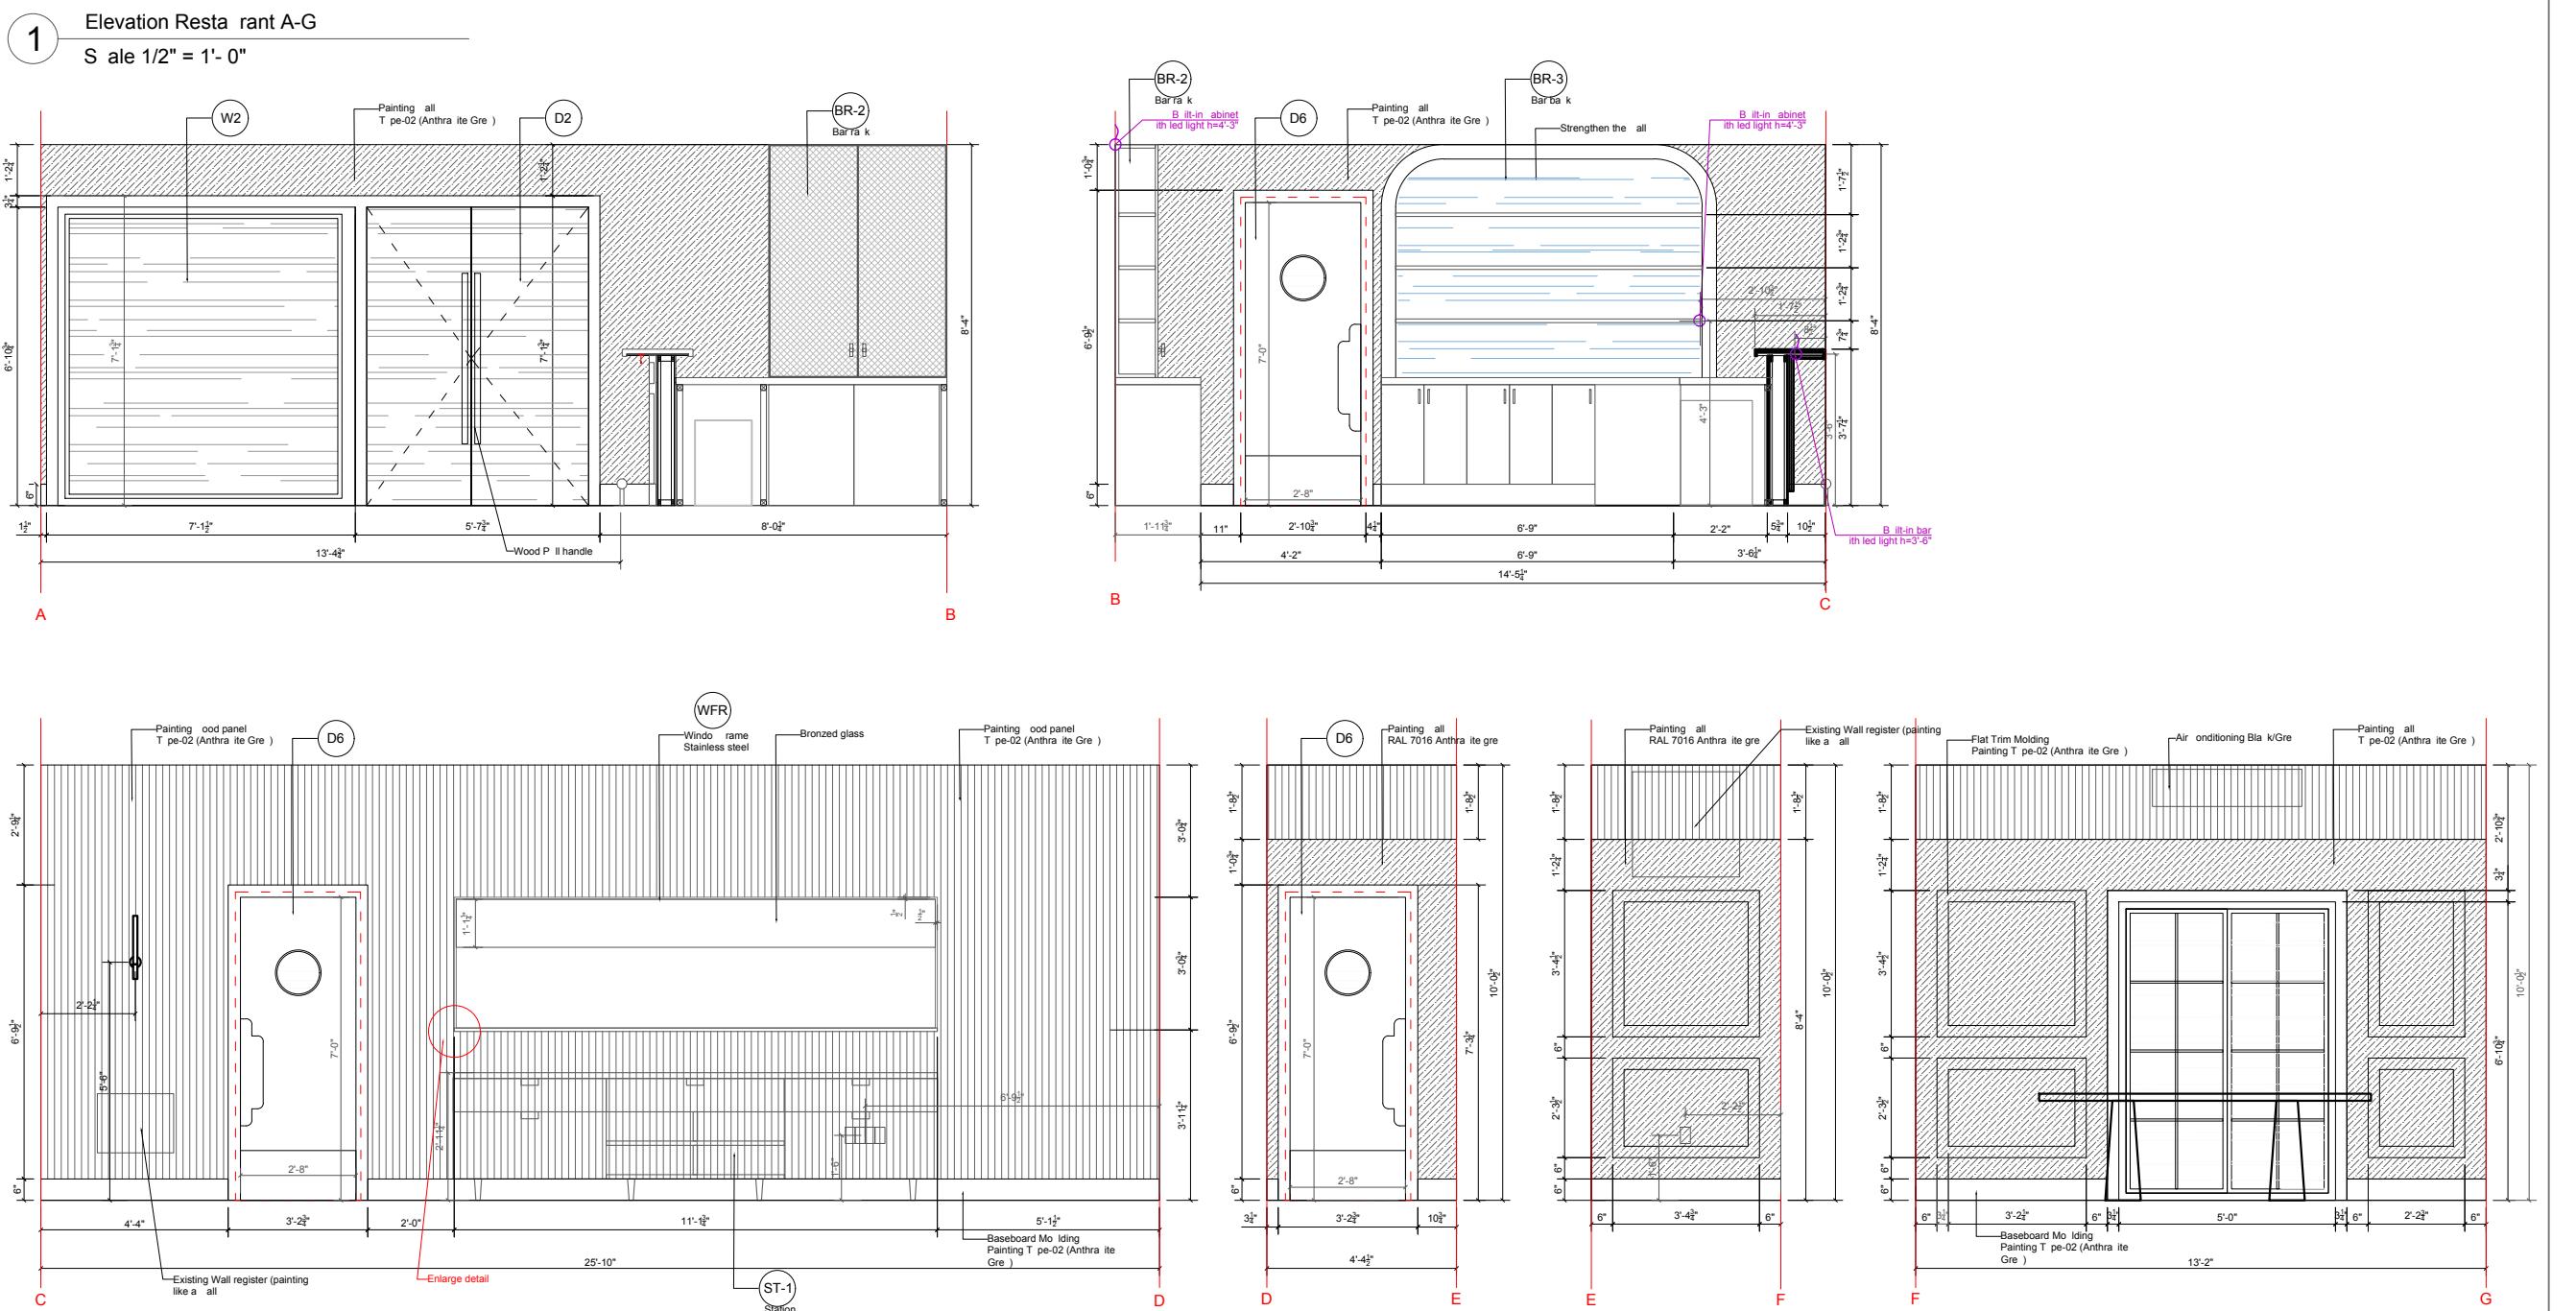

GENERAL NOTES:
1. ELEVATIONS DEPICTING CABINETRY IN DESIGNERS DOCUMENTATION IS FOR DESIGN PURPOSES ONLY;
2. DESIGNER DOES NOT ASSUME THE RESPONSIBILITY OF ANY STRUCTURAL OR FIELD DIMENSIONS/CONDITIONS;

DRAWING TITLE:
ELEVATION 1 A-G

DRAWN BY: KEIDUNOV IRINA



SCALE: 1/2"=1'-0"

DATE: 03.21.2022


SHEET : 5.2

A1

1 Elevation Restaurant G-A
Scale 1/2" = 1'-0"

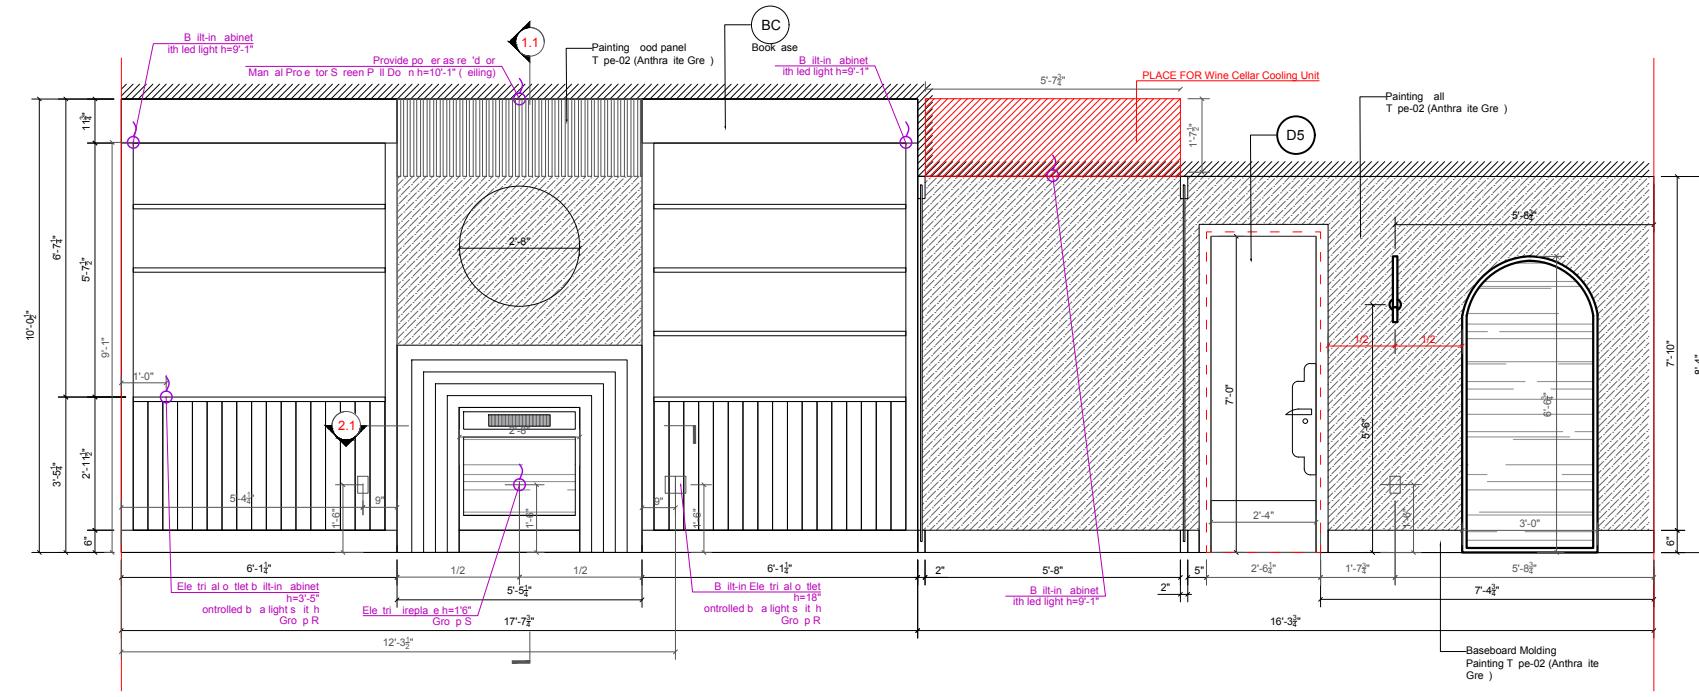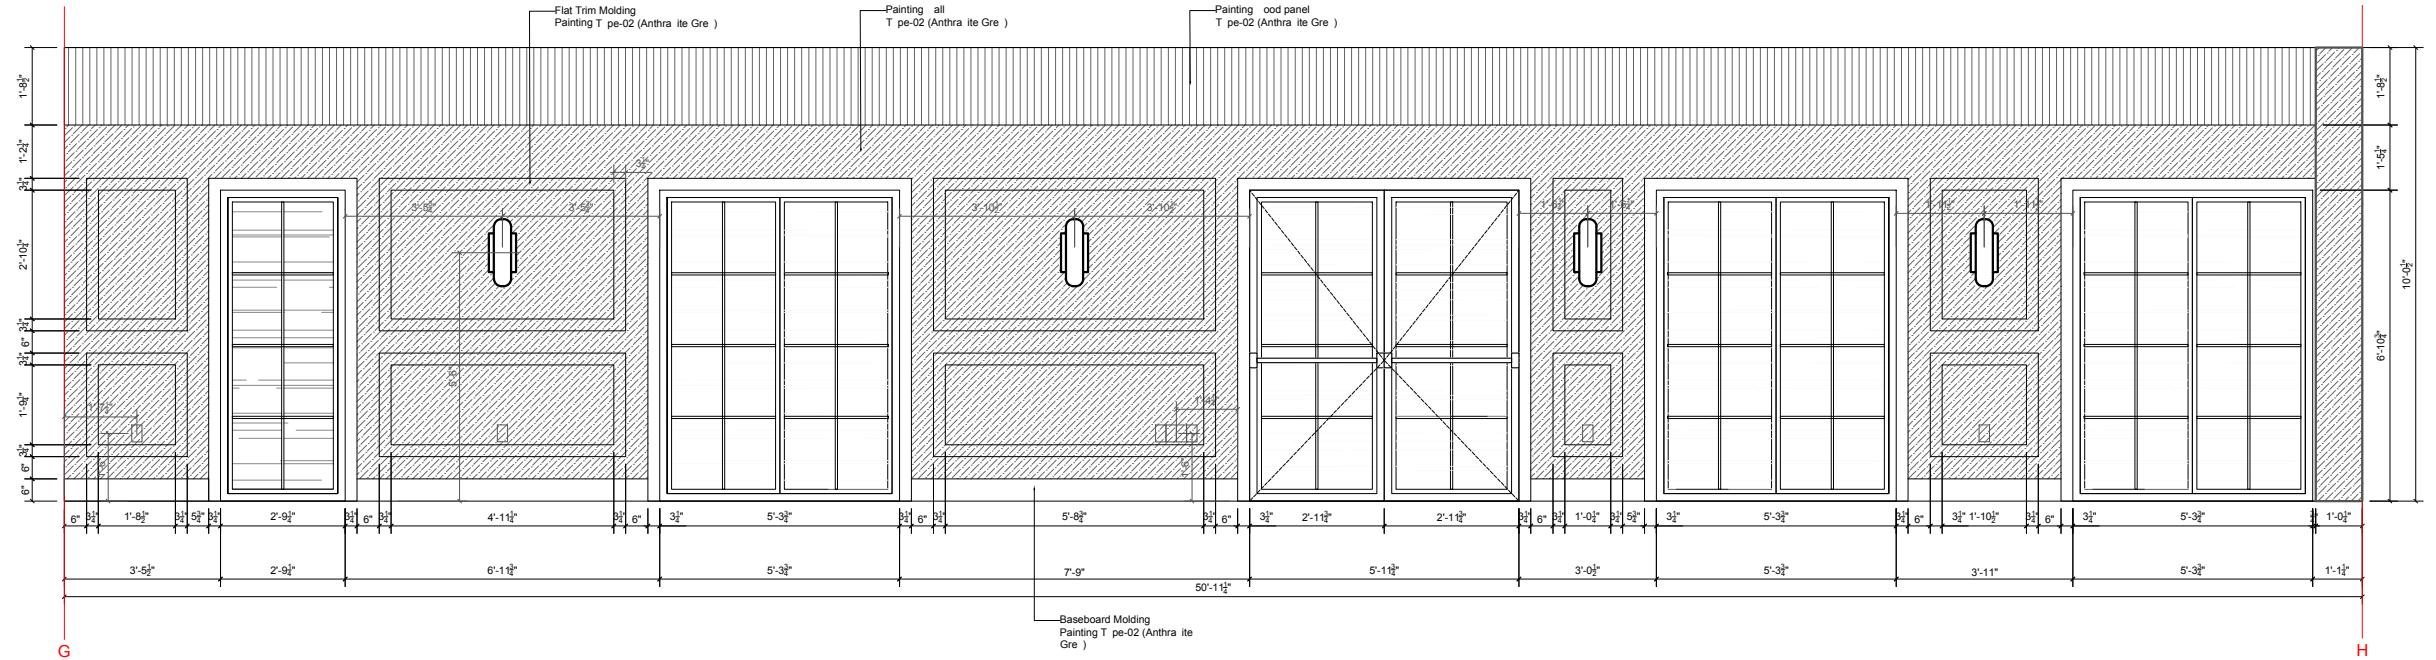

2.1 Elevation Fireplace
Scale 1/1" = 1'-0"


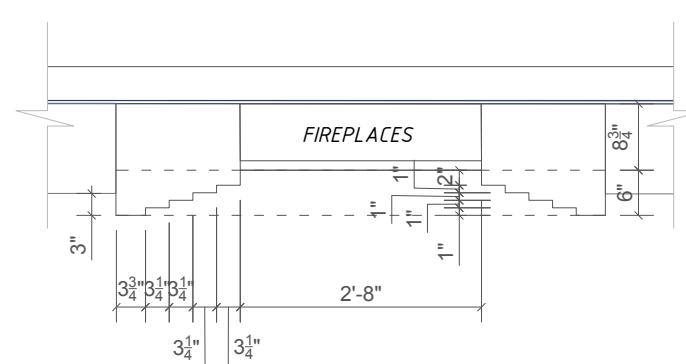


1.1 Elevation Fireplace
Scale 1/1" = 1'-0"

Painting odd panel
T pe-02 (Anthracite Gre)

Painting all
T pe-02 (Anthracite Gre)

Painting all
T pe-02 (Anthracite Gre)

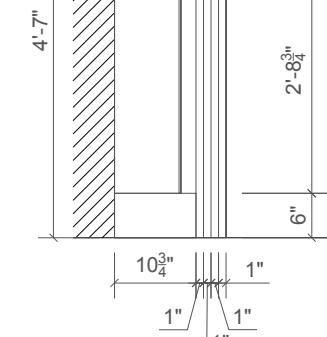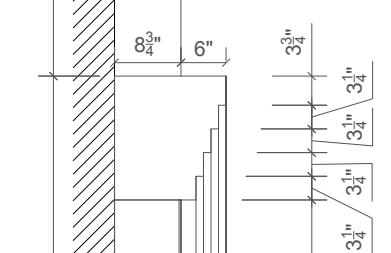

RESTAURANT
OWL'S NEST

DRAWING TITLE:
ELEVATION 1 G-A

DRAWN BY: KEIDUNOV IRINA

SCALE: 1/2"=1'-0"

DATE: 03.21.2022



SHEET : 5.3

A1


GENERAL NOTES:
1. ELEVATIONS DEPICTING CABINETRY IN DESIGNERS DOCUMENTATION IS FOR DESIGN PURPOSES ONLY;
2. DESIGNER DOES NOT ASSUME THE RESPONSIBILITY OF ANY STRUCTURAL OR FIELD DIMENSIONS/CONDITIONS;

**RESTAURANT
OWL'S NEST**

2 Elevation Hall
Scale 1/2" = 1'- 0"

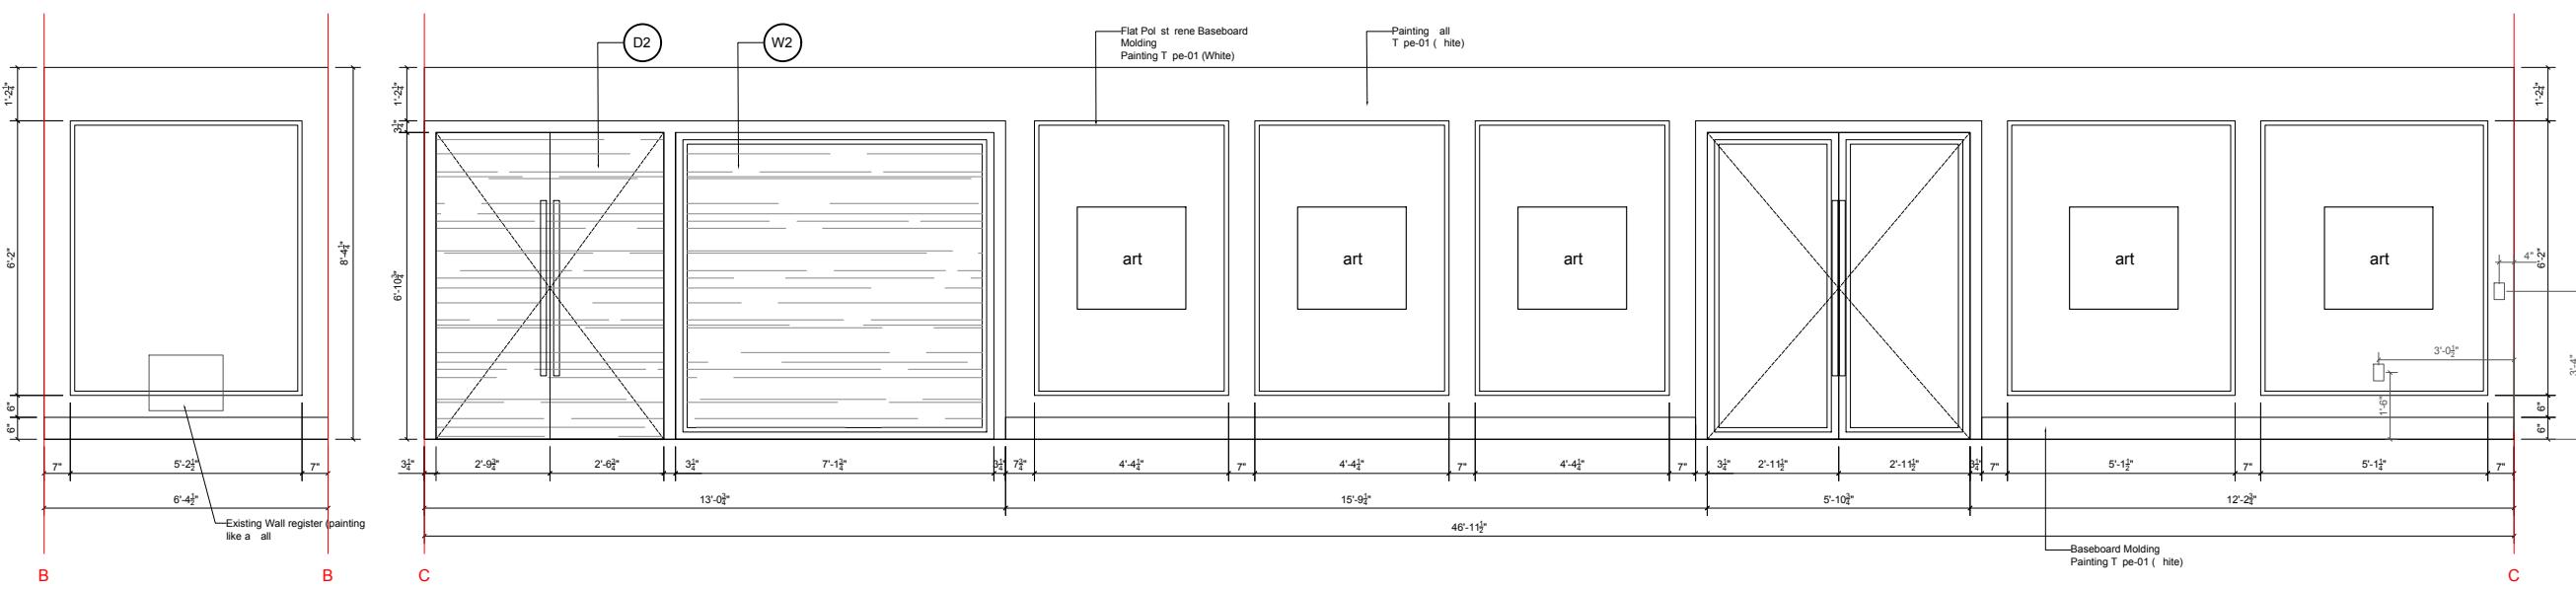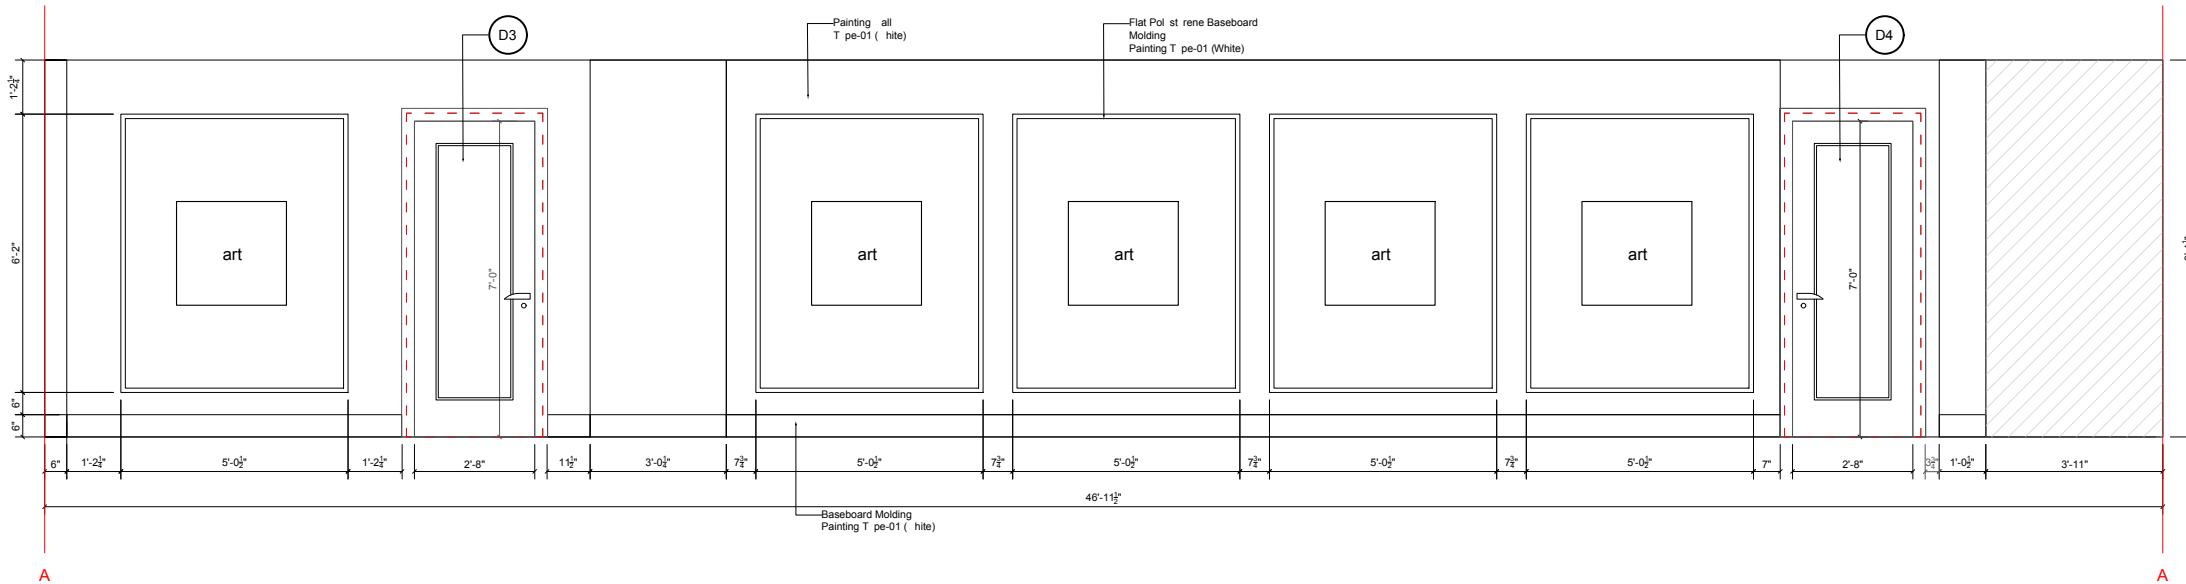

2 Floor plan Hall
Scale 1/4" = 1'- 0"

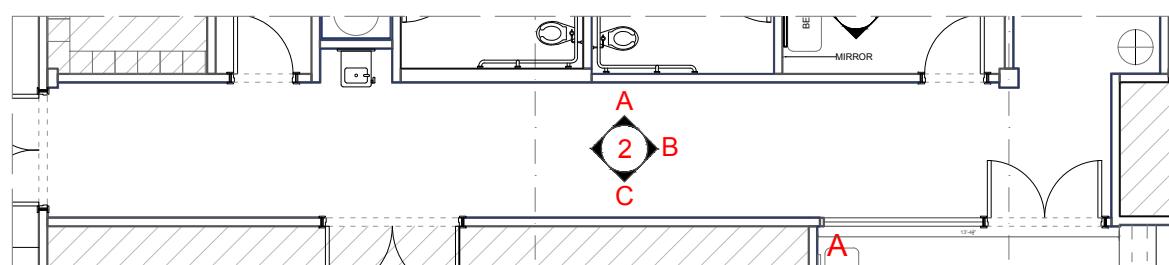

DRAWING TITLE:
ELEVATION 2

DRAWN BY: KEIDUNOV IRINA


SCALE: 1/2"=1'-0"

DATE: 03.21.2022


SHEET : 5.4

GENERAL NOTES:
1. ELEVATIONS DEPICTING CABINETRY IN DESIGNERS DOCUMENTATION IS FOR DESIGN PURPOSES ONLY;
2. DESIGNER DOES NOT ASSUME THE RESPONSIBILITY OF ANY STRUCTURAL OR FIELD DIMENSIONS/CONDITIONS;

RESTAURANT OWL'S NEST

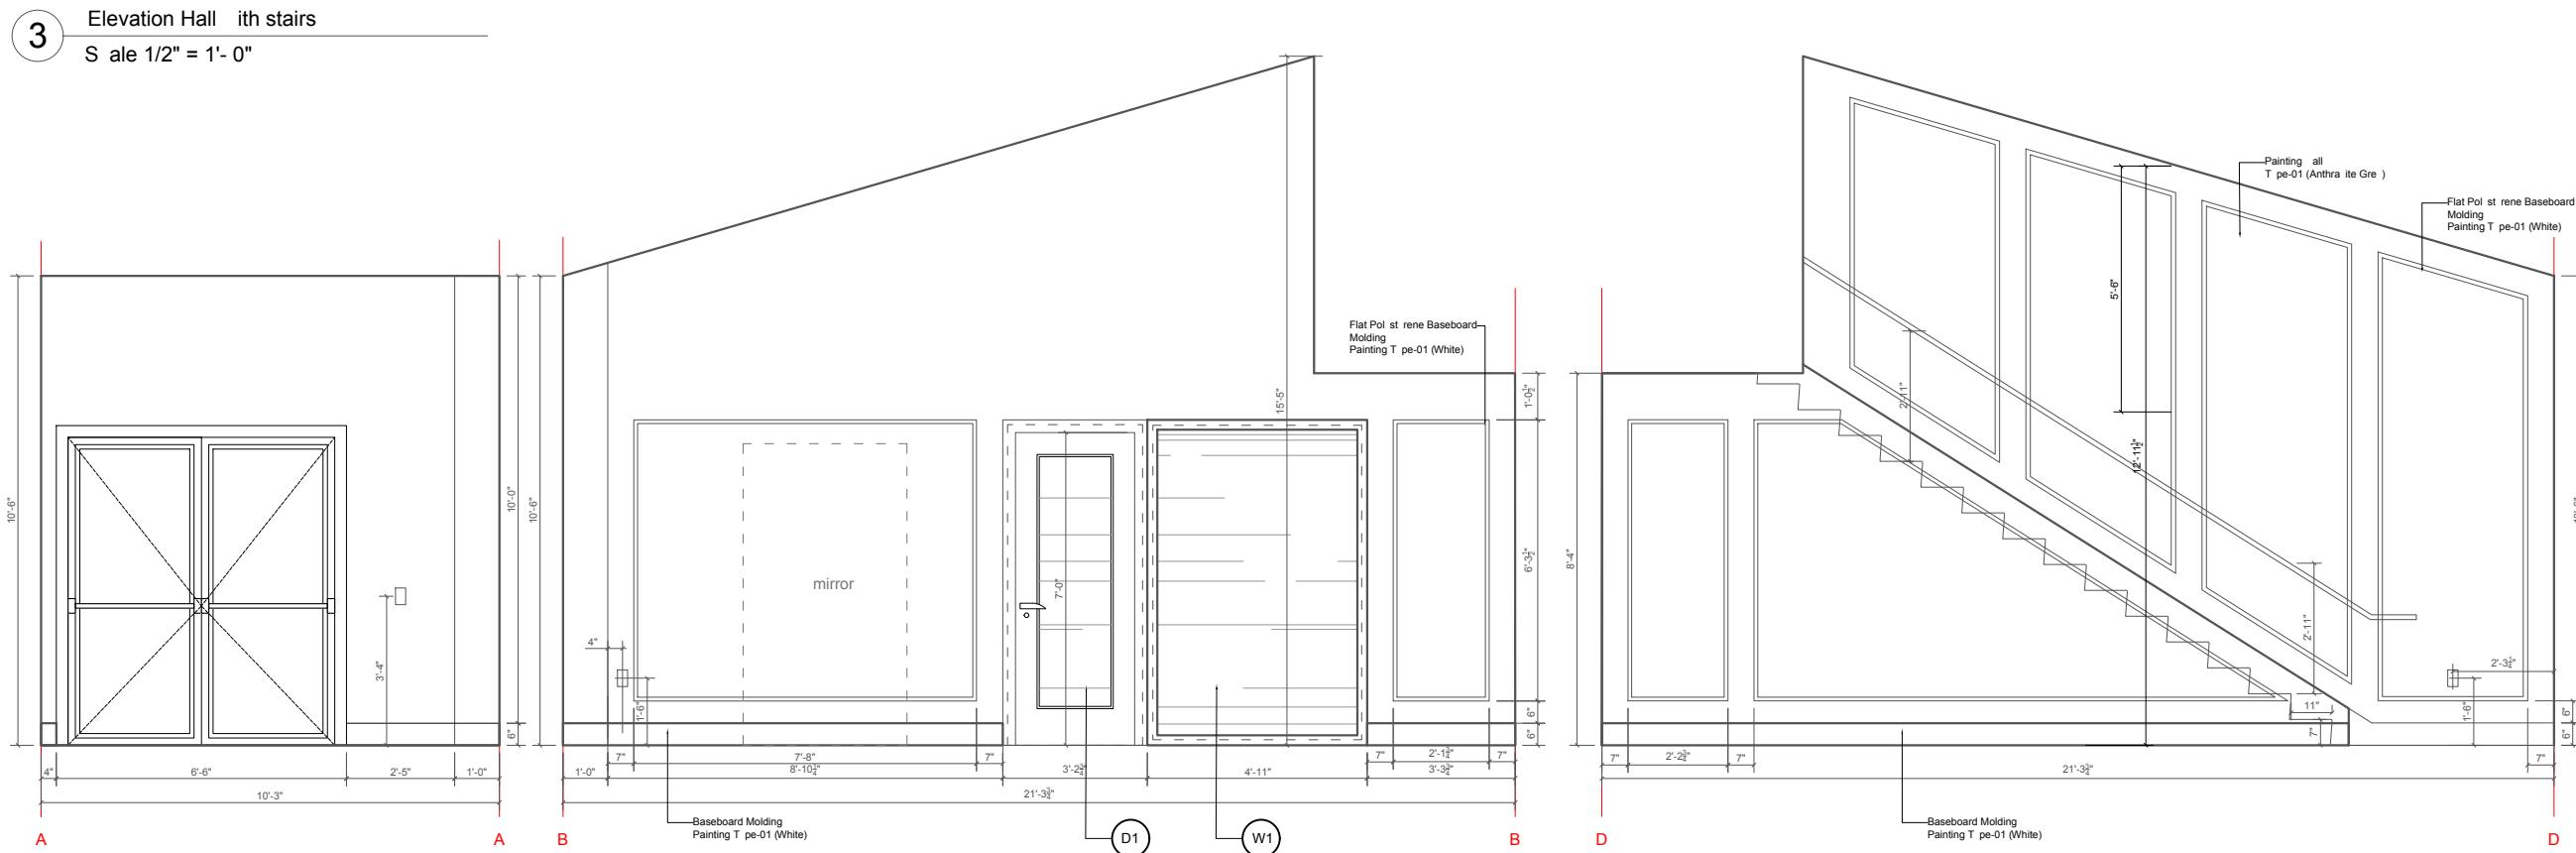

Floor plan Hall with stairs
Scale 1/4" = 1'- 0"

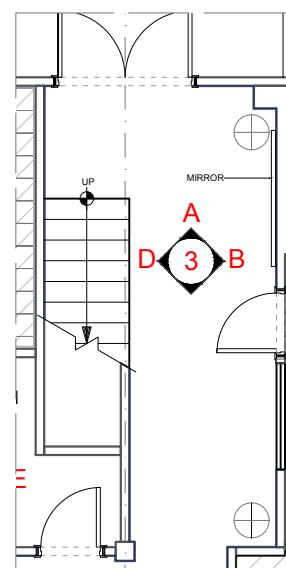

GENERAL NOTES:
 1. ELEVATIONS DEPICTING CABINETRY IN DESIGNERS DOCUMENTATION IS FOR DESIGN PURPOSES ONLY;
 2. DESIGNER DOES NOT ASSUME THE RESPONSIBILITY OF ANY STRUCTURAL OR FIELD DIMENSIONS/CONDITIONS;

DRAWING TITLE:
ELEVATION 3

DRAWN BY: KEIDUNOV IRINA







SCALE: 1/2"=1'-0"

DATE: 03.21.2022

SHEET : 5.5

A1

RESTAURANT OWL'S NEST

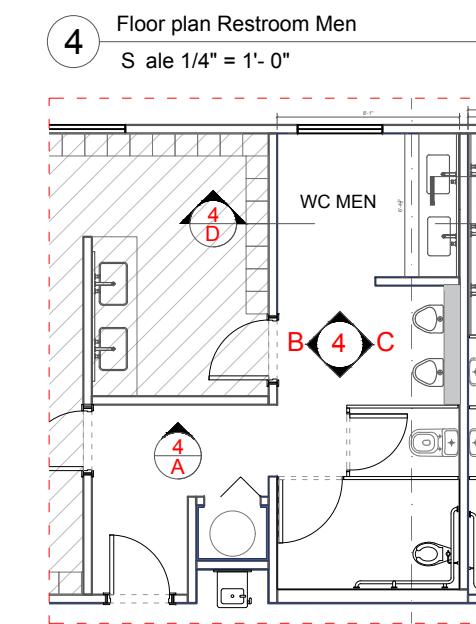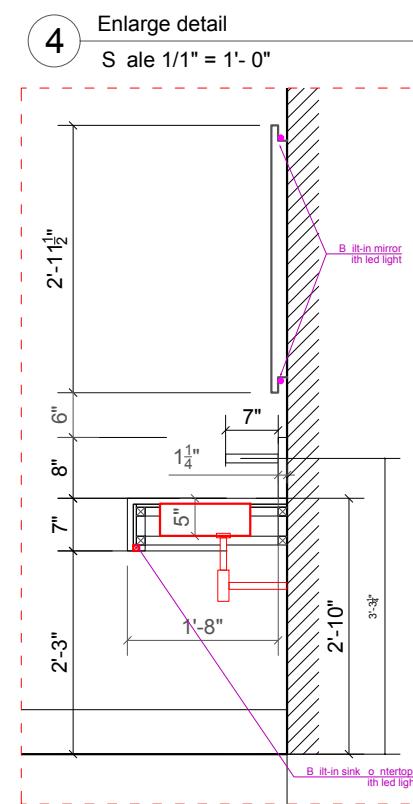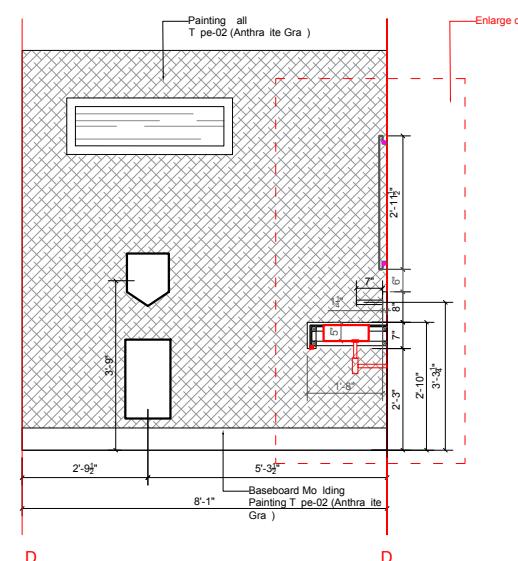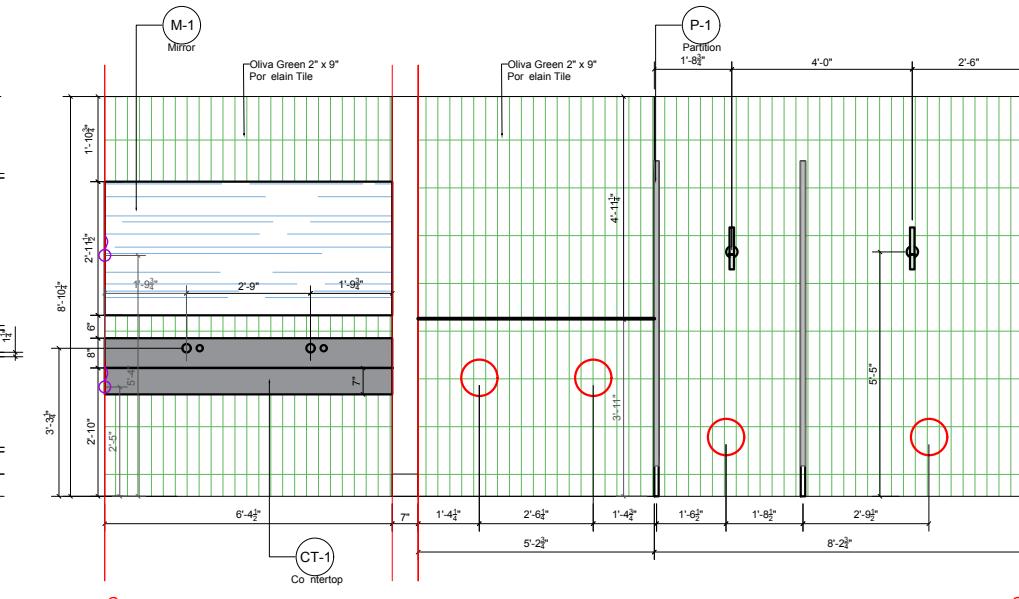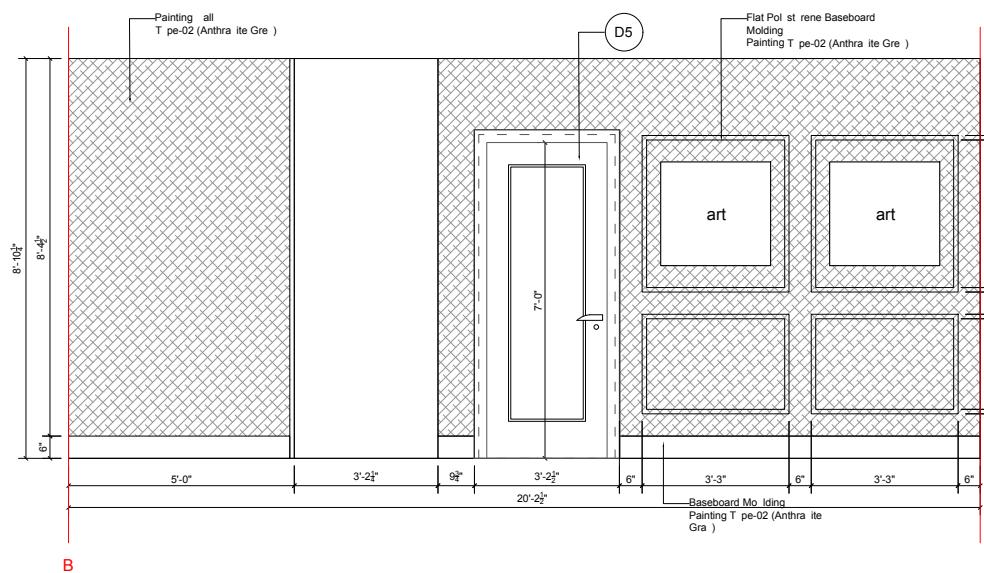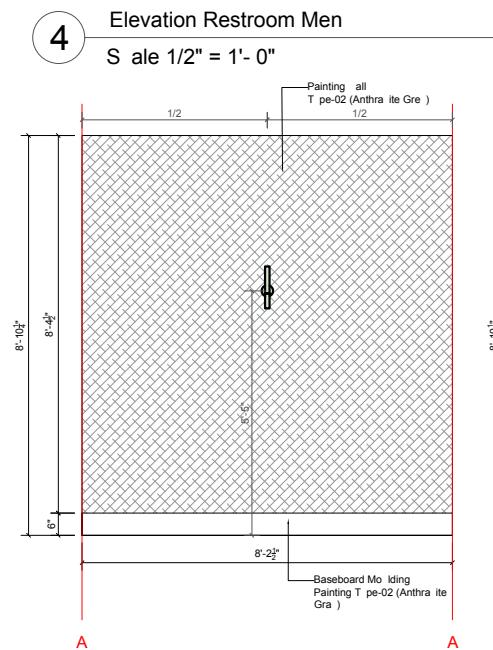

DRAWING TITLE:
ELEVATION 4

DRAWN BY: KEIDUNOV IRINA

SCALE: 1/2"=1'-0"

DATE: 03.21.2022


SHEET : 5.6

GENERAL NOTES:
1. ELEVATIONS DEPICTING CABINETRY IN DESIGNERS DOCUMENTATION IS FOR DESIGN PURPOSES ONLY;
2. DESIGNER DOES NOT ASSUME THE RESPONSIBILITY OF ANY STRUCTURAL OR FIELD DIMENSIONS/CONDITIONS;


RESTAURANT OWL'S NEST

5 Elevation Restroom Women


Scale 1/2" = 1'- 0"

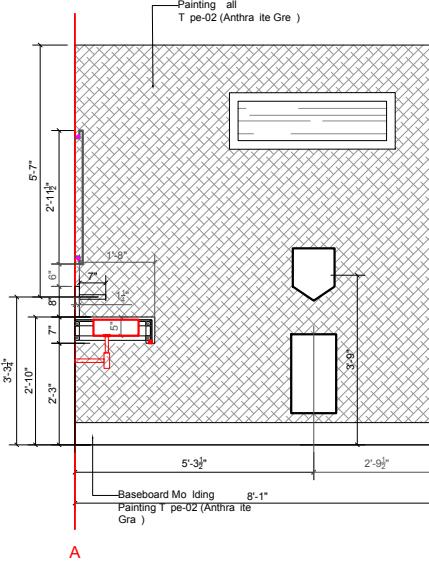


A A

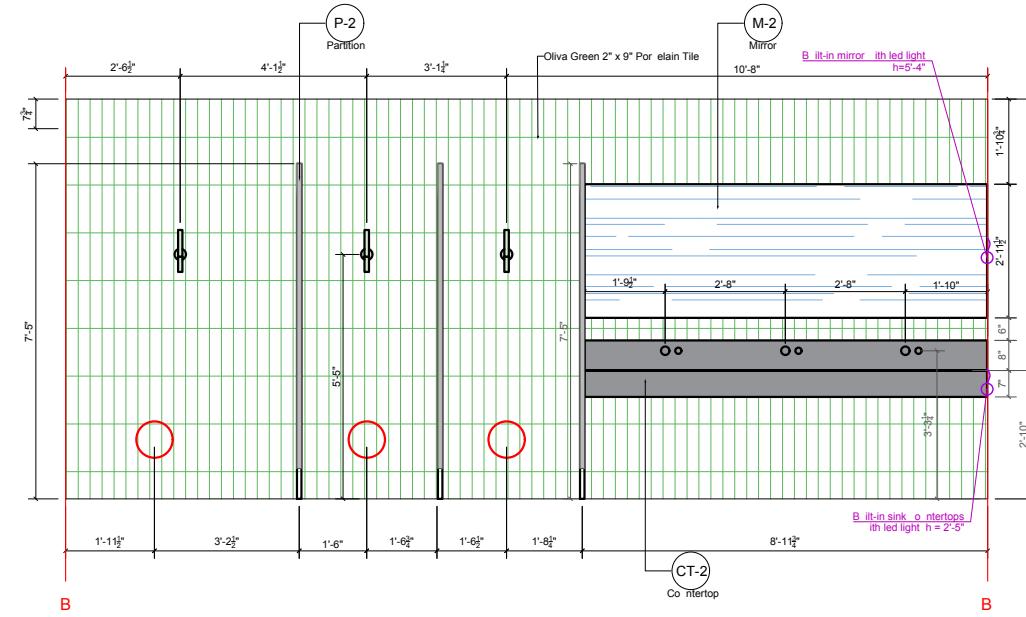


B B

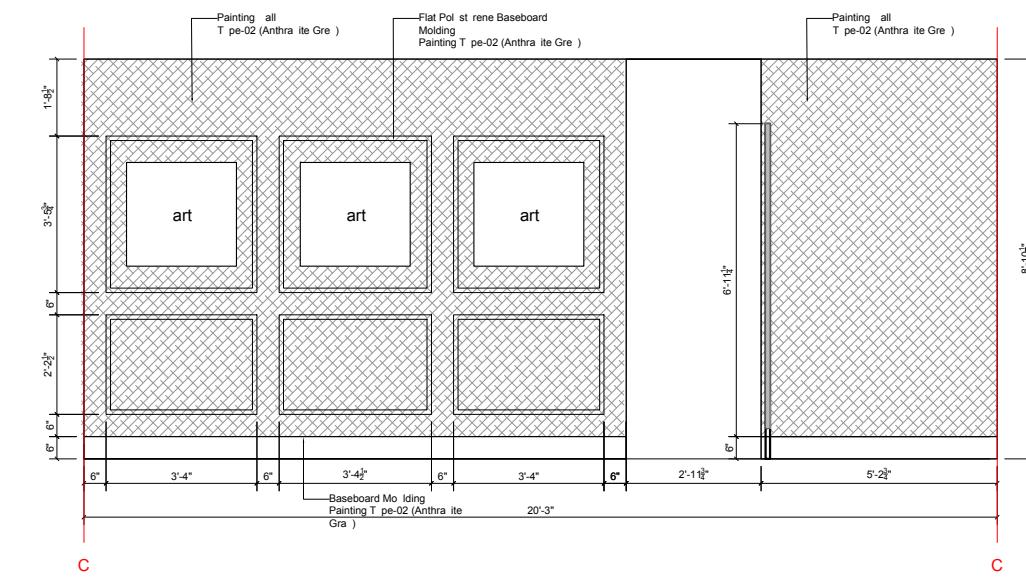

C C

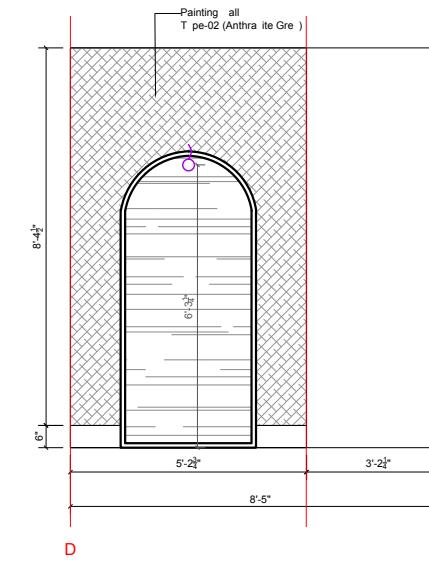


D D

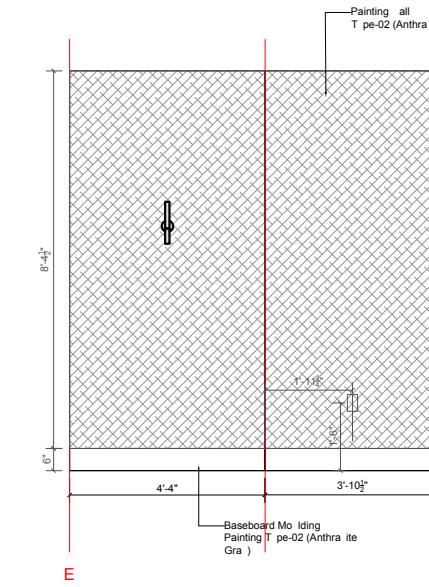

E E

4 Floor plan Restroom Women

Scale 1/4" = 1'- 0"

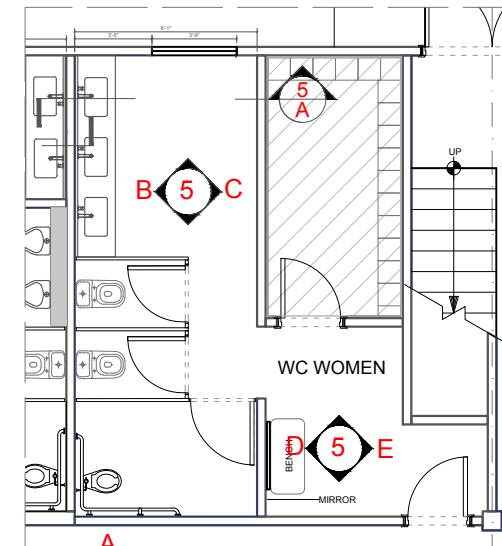

DRAWING TITLE:

ELEVATION 5

DRAWN BY: KEIDUNOV IRINA

SCALE: 1/2"=1'-0"


DATE: 03.21.2022

SHEET : 5.7

GENERAL NOTES:
1. ELEVATIONS DEPICTING CABINETRY IN DESIGNERS DOCUMENTATION IS FOR DESIGN PURPOSES ONLY;
2. DESIGNER DOES NOT ASSUME THE RESPONSIBILITY OF ANY STRUCTURAL OR FIELD DIMENSIONS/CONDITIONS;

A1

FURNITURE SCHEMES, JOINERY AND FURNITURE

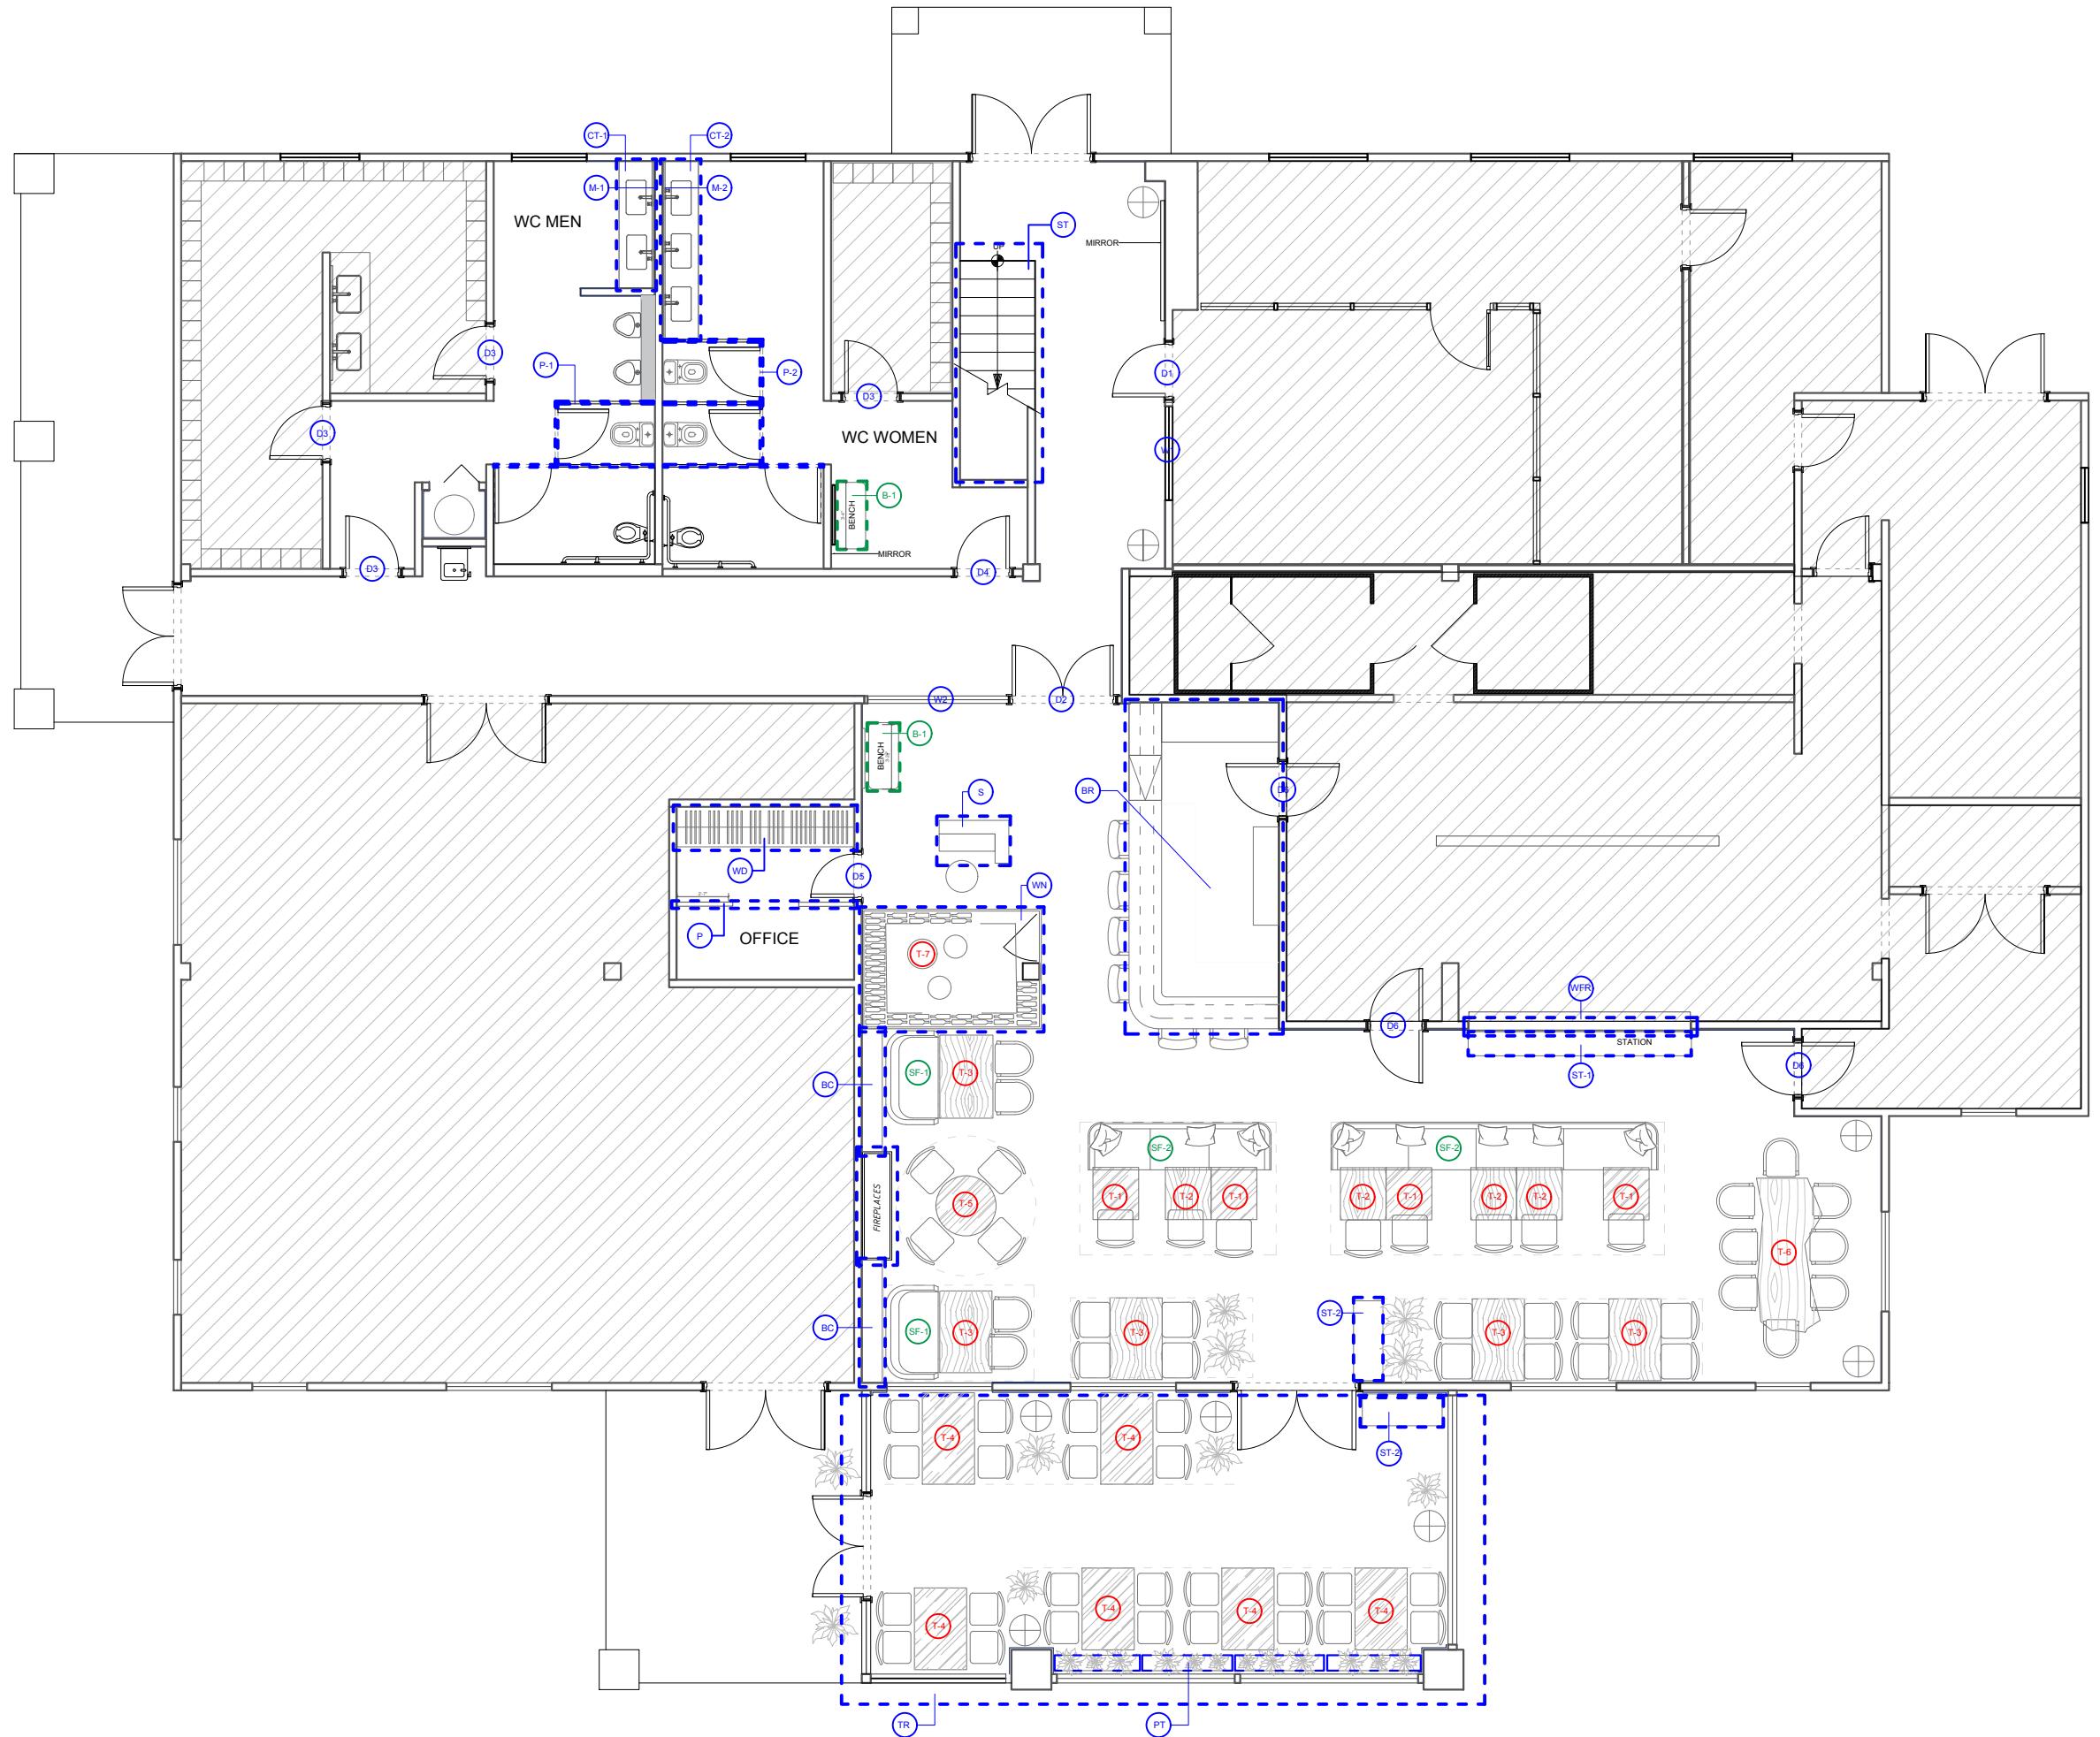

RESTAURANT OWL'S NEST

DRAWING TITLE:
FURNITURE LAYOUT

DRAWN BY: KEIDUNOV IRINA

SCALE: 1/4"=1'-0"

DATE: 03.21.2022



SHEET : 6.1

A1



GENERAL NOTES:
 1. ELEVATIONS DEPICTING CABINETS IN DESIGNERS DOCUMENTATION IS FOR DESIGN PURPOSES ONLY;
 2. DESIGNER DOES NOT ASSUME THE RESPONSIBILITY OF ANY STRUCTURAL OR FIELD DIMENSIONS/CONDITIONS;

RESTAURANT OWL'S NEST



D1,W1 cigar store door and indo
N mber - 1
Right hand reverse

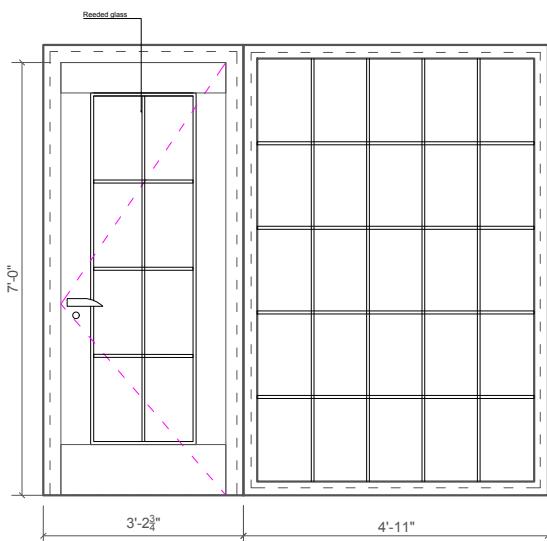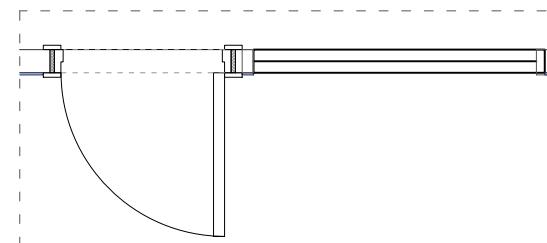



D2,W2 Double Door and indo to the restaurant
N mber - 1

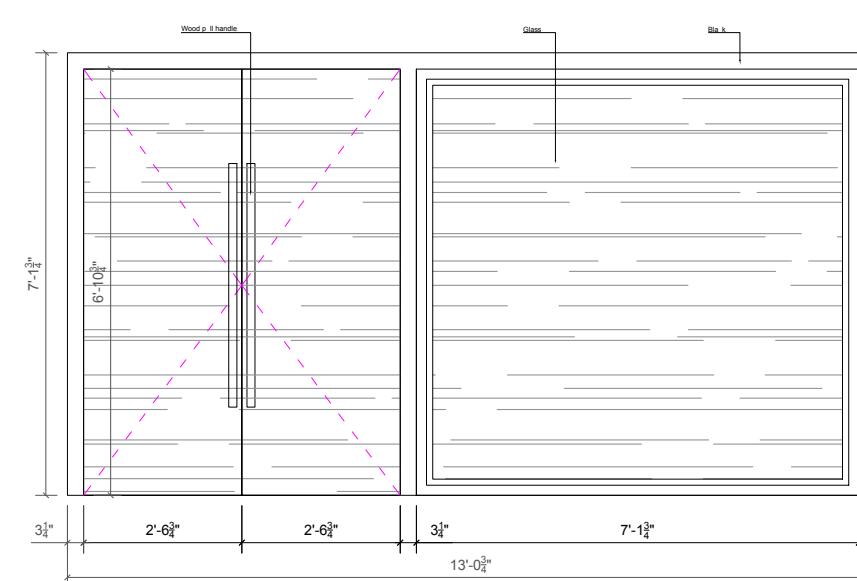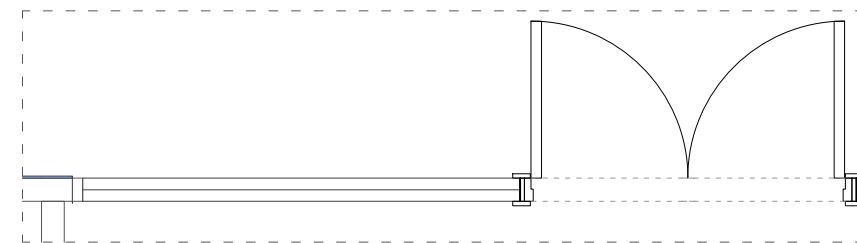



D3 Door 3
N mber - 4
Le t hand

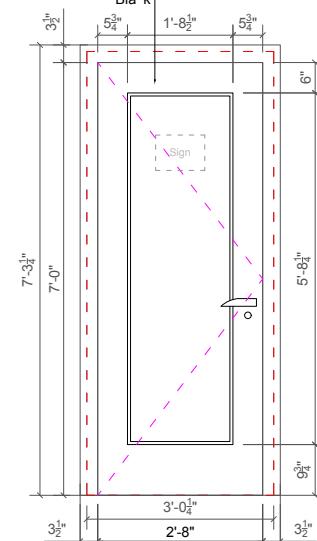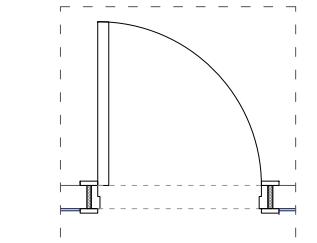



D4 Door 4
N mber - 1
Right hand

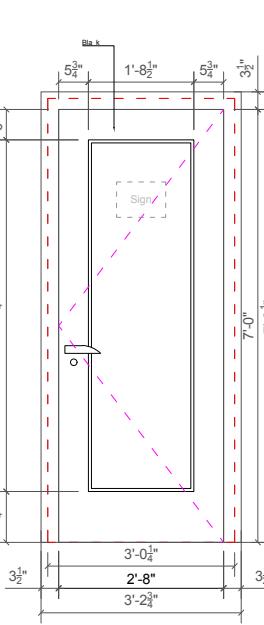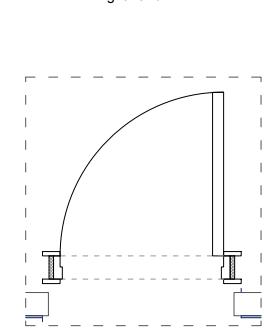



D5 Door 5
N mber - 1
Le t hand

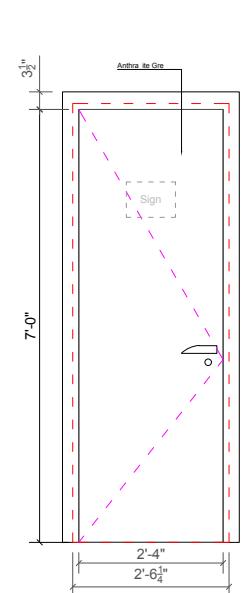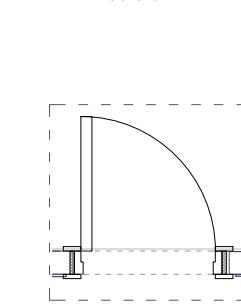

D6 Door 6
N mber - 2
S singing door

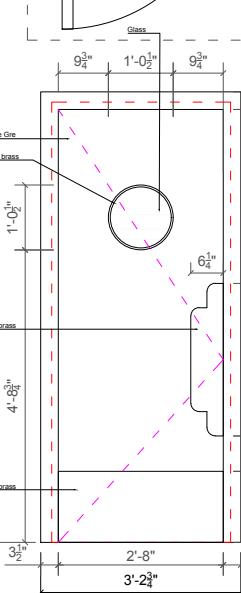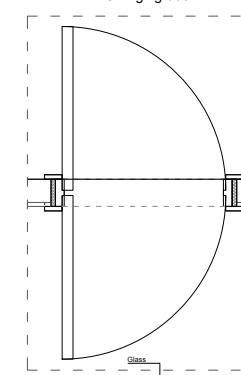

D7 Door 7
N mber - 1
S singing door

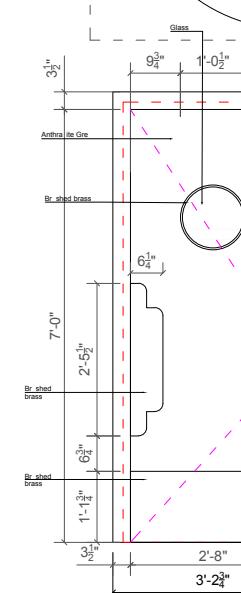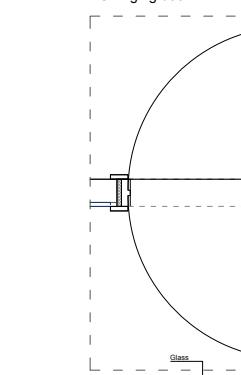

DRAWING TITLE:
DOORS

DRAWN BY: KEIDUNOV IRINA

SCALE: 1/1"=1'-0"



DATE: 03.21.2022

SHEET : 6.2

A1

GENERAL NOTES:
 1. ELEVATIONS DEPICTING CABINETRY IN DESIGNERS DOCUMENTATION IS FOR DESIGN PURPOSES ONLY;
 2. DESIGNER DOES NOT ASSUME THE RESPONSIBILITY OF ANY STRUCTURAL OR FIELD DIMENSIONS/CONDITIONS;
 3. Vendor shall provide bl eprints;
 4. Get client and designer approvals or materials be ore prod tion

**RESTAURANT
OWL'S NEST**

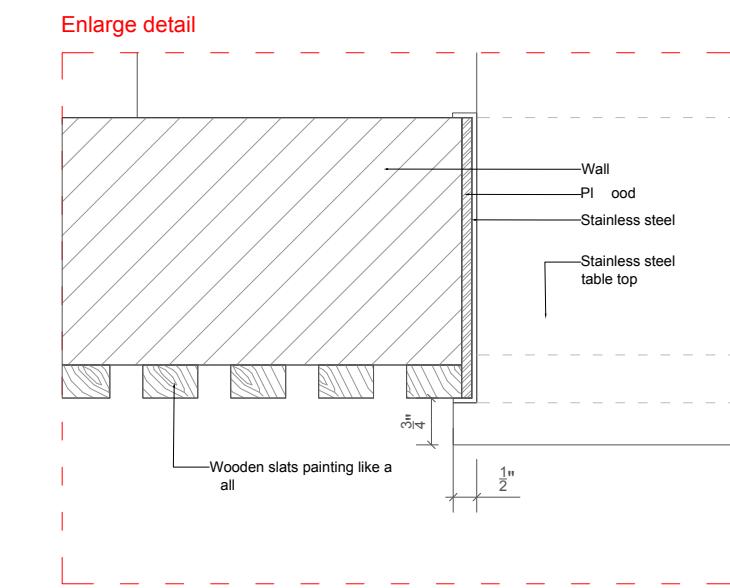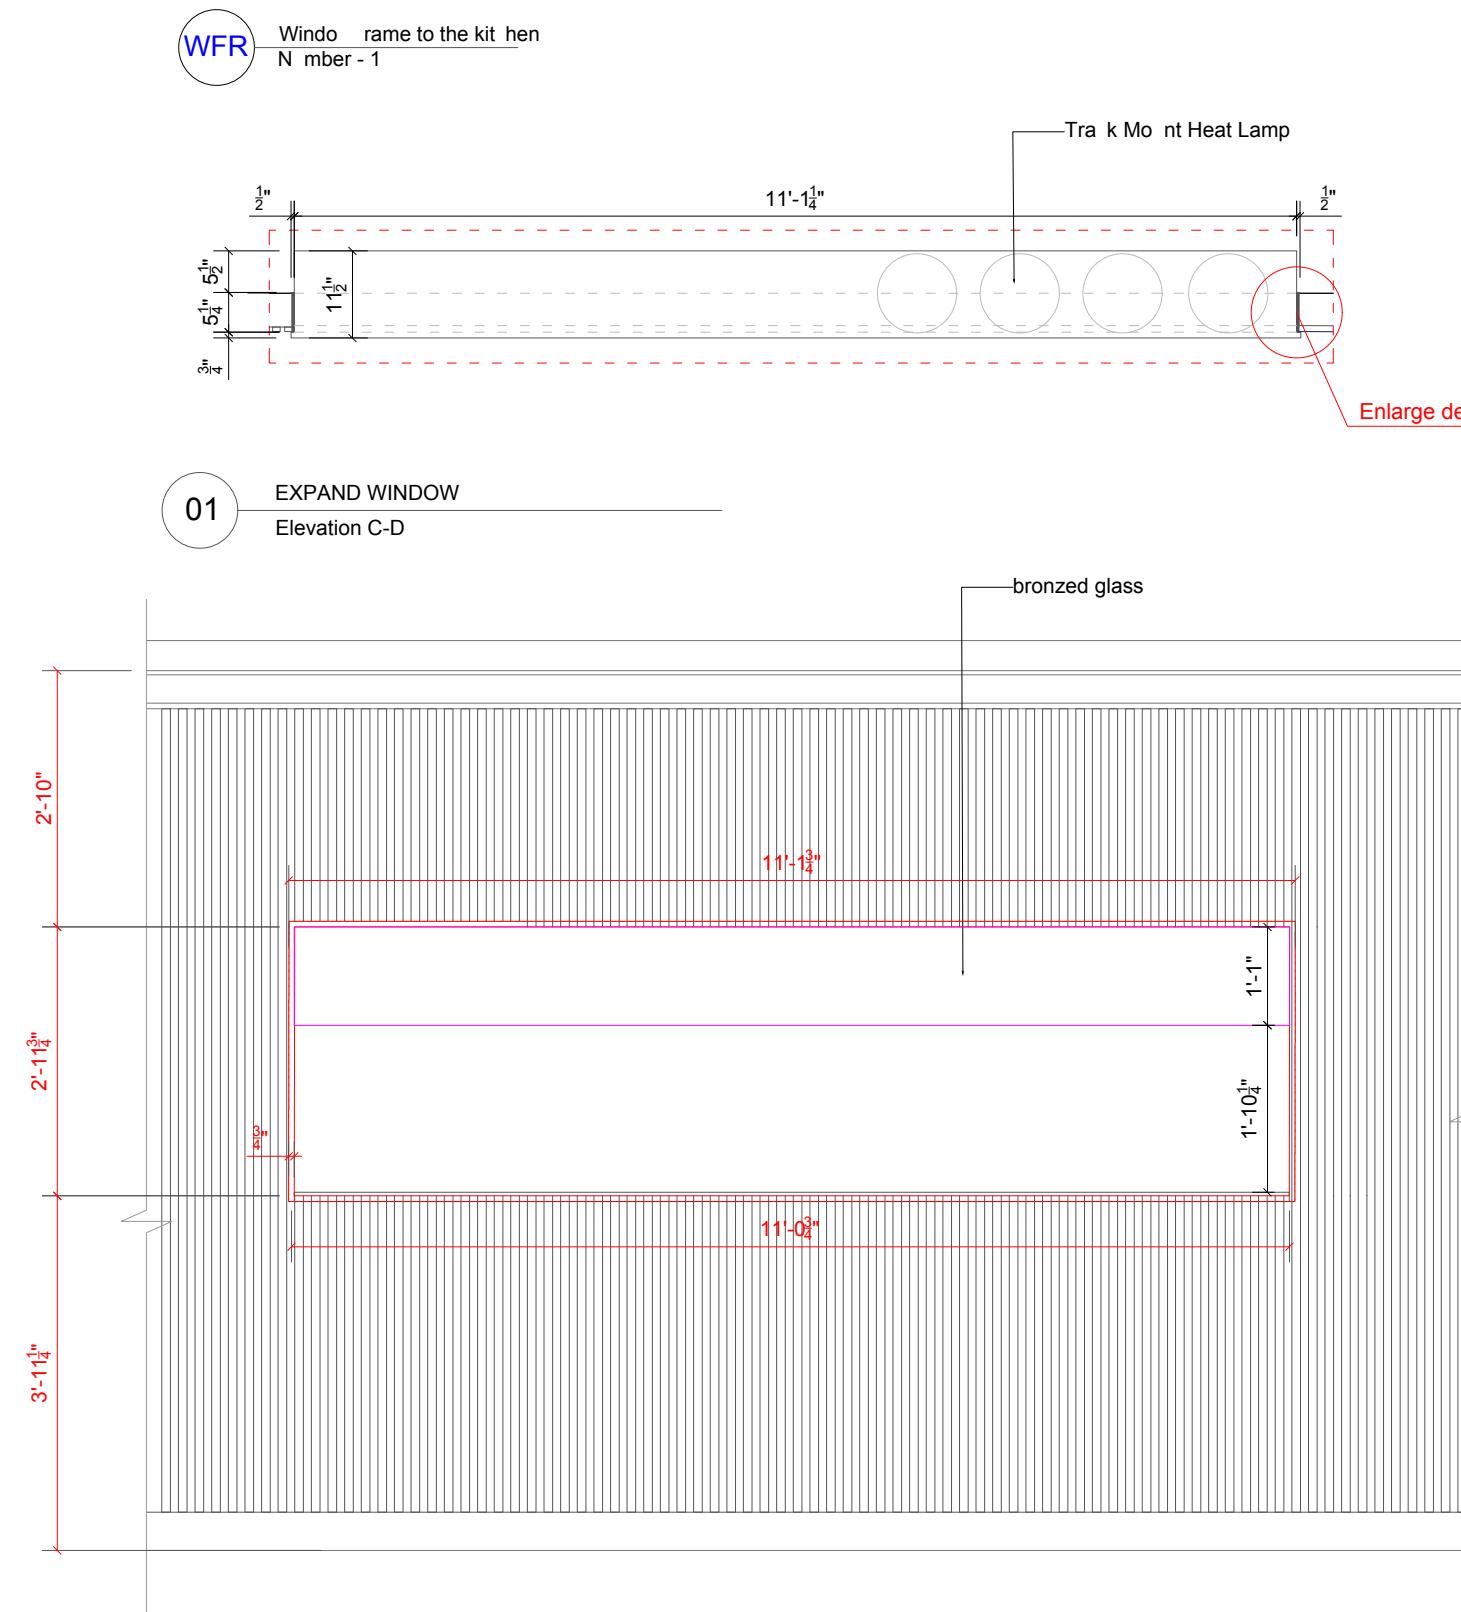

GENERAL NOTES:
 1. ELEVATIONS DEPICTING CABINETRY IN DESIGNERS DOCUMENTATION IS FOR DESIGN PURPOSES ONLY;
 2. DESIGNER DOES NOT ASSUME THE RESPONSIBILITY OF ANY STRUCTURAL OR FIELD DIMENSIONS/CONDITIONS;
 3. Vendor shall provide blueprints;
 4. Get client and designer approvals or materials before production

DRAWING TITLE:
EXPAND WINDOW

DRAWN BY: KEIDUNOV IRINA

SCALE: 1/1"=1'-0"

DATE: 03.21.2022

SHEET : 6.3



A1

SF-1 SCHEME So a


N mber - 2

Material: Wain t veneer, Gra velvet


De orative pillo s 16"x 16" /400x400 mm (olive velvet) - 4

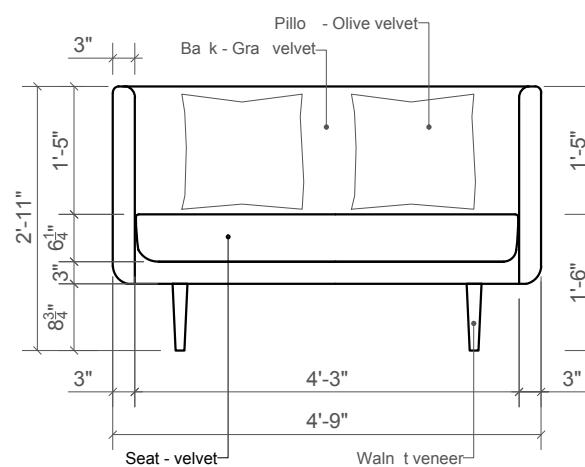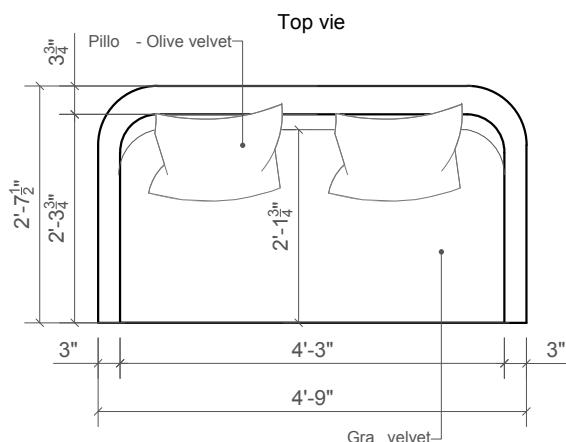

Front vie

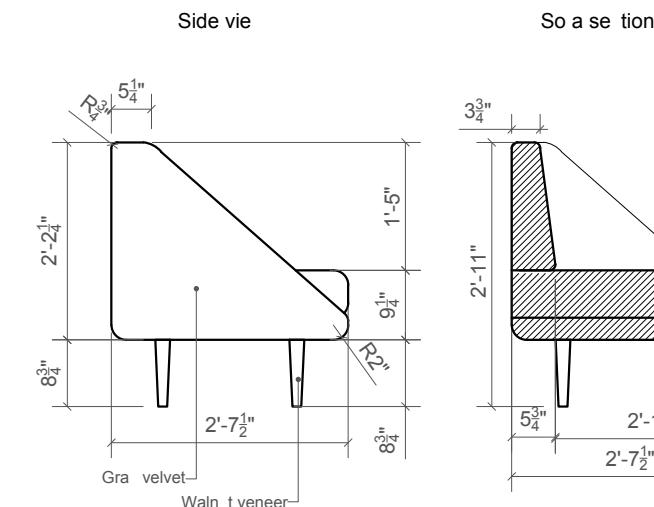

Side vie

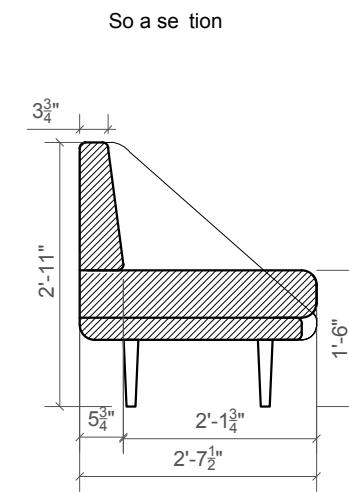

So a se tion




Sample

SF-2 SCHEME So a


N mber - 1

Material: Wain t veneer, Olive velvet, Brass


De orative pillo s 16"x 16" /400x400 mm (olive velvet) - 3

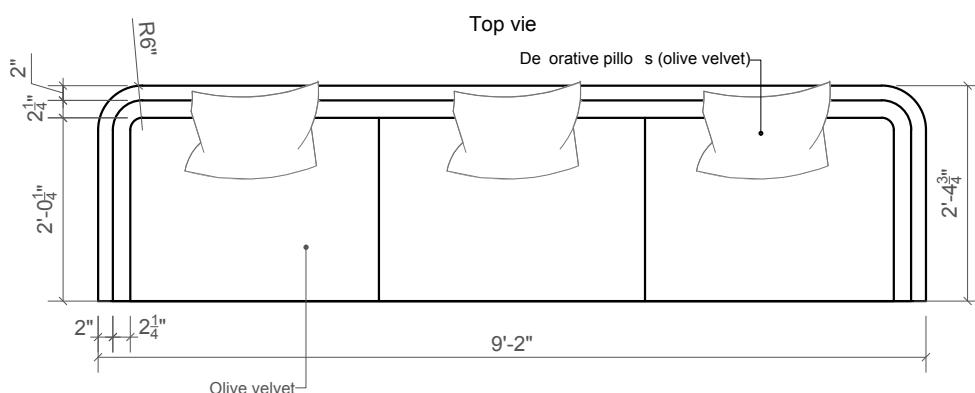


Front vie

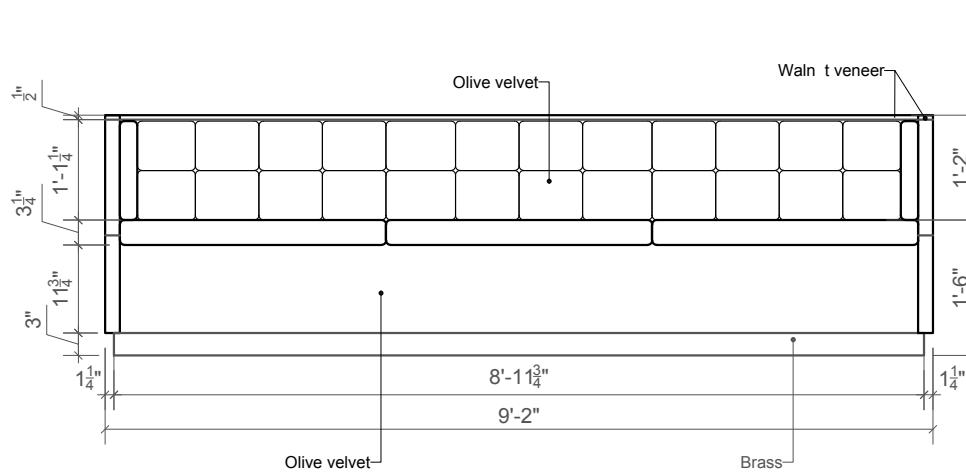

Side vie

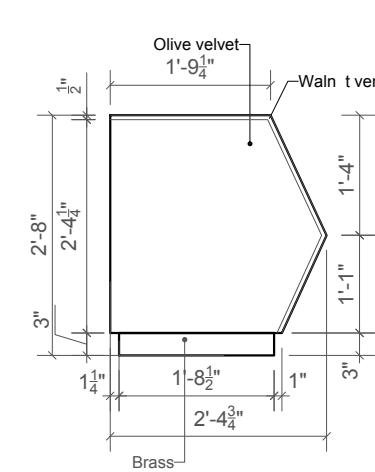

Se tion

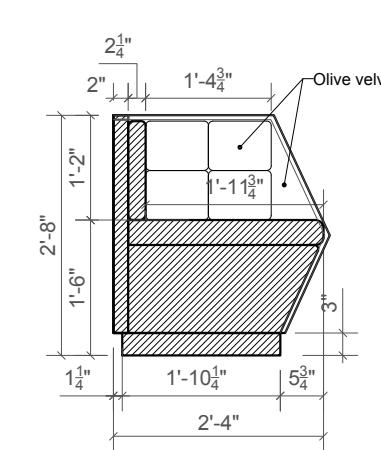

Sample



Sample Gra velvet



Sample Olive velvet



RESTAURANT
OWL'S NEST

DRAWING TITLE:
FURNITURE
SOFAS

DRAWN BY: KEIDUNOV IRINA





SCALE: 1/4"=1'-0"

DATE: 03.21.2022


SHEET : 6.4

GENERAL NOTES:
1. ELEVATIONS DEPICTING CABINETRY IN DESIGNERS DOCUMENTATION IS FOR DESIGN PURPOSES ONLY;
2. DESIGNER DOES NOT ASSUME THE RESPONSIBILITY OF ANY STRUCTURAL OR FIELD DIMENSIONS/CONDITIONS;
3. Vendor shall provide bl eprints;
4. Get client and designer approvals or materials be ore prod tion

SF-3 SCHEME So a
N mber - 1
Material: Walnut veneer, Olive velvet, Brass
De orative pilo s 16"x 16" /400x400 mm (olive velvet) - 5

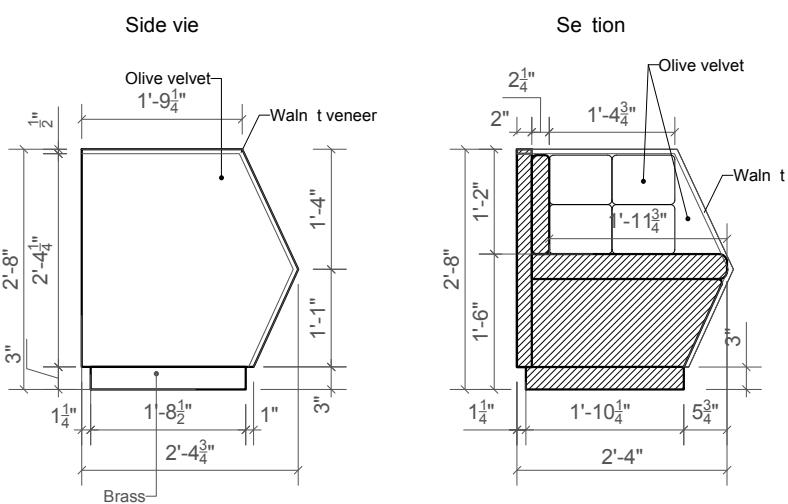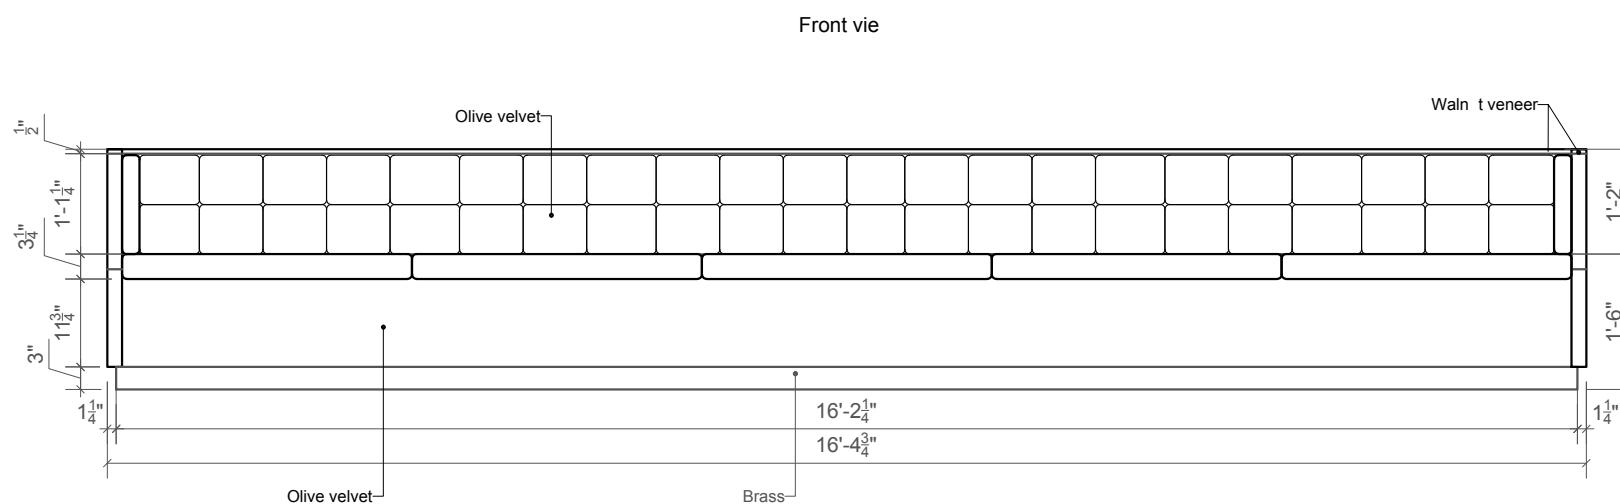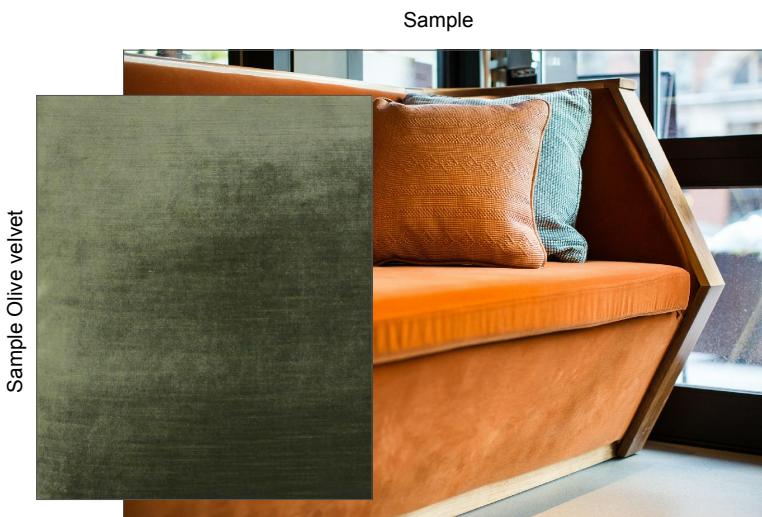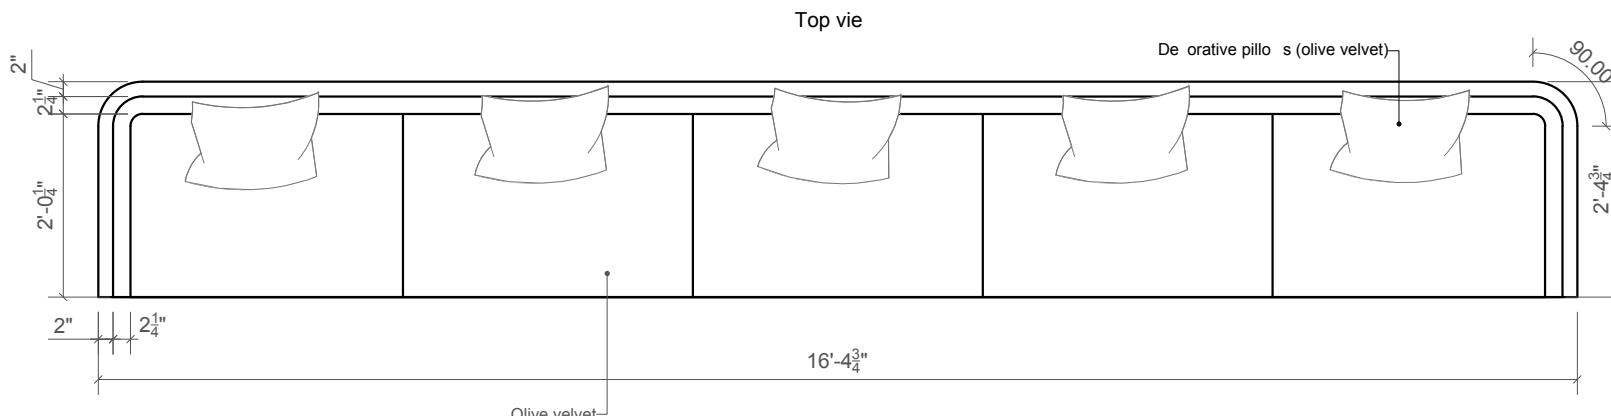

B-1 SCHEME Ben h
N mber - 2
Material: leg - brass, Beige bro n leather
40" x 18" h=17"

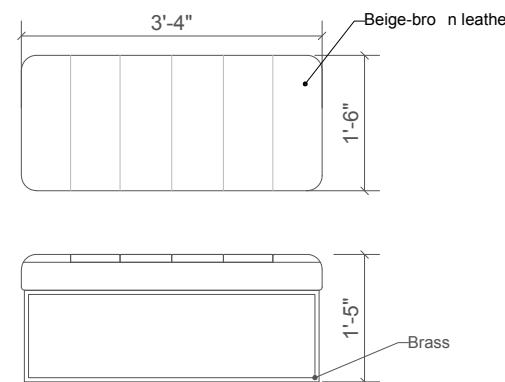

RESTAURANT
OWL'S NEST

DRAWING TITLE:
FURNITURE
SOFAS

DRAWN BY: KEIDUNOV IRINA

SCALE: 1/4"=1'-0"


DATE: 03.21.2022

SHEET : 6.5


GENERAL NOTES:
1. ELEVATIONS DEPICTING CABINETRY IN DESIGNERS DOCUMENTATION IS FOR DESIGN PURPOSES ONLY;
2. DESIGNER DOES NOT ASSUME THE RESPONSIBILITY OF ANY STRUCTURAL OR FIELD DIMENSIONS/CONDITIONS;
3. Vendor shall provide bl eprints;
4. Get client and designer approvals or materials be ore prod tion

RESTAURANT OWL'S NEST


T-1 SCHEME TABLE
Number - 4
Material: Black Metal - legs, Marble - top
32"x29" (810x740mm) h= 29 1/2 " (750mm)

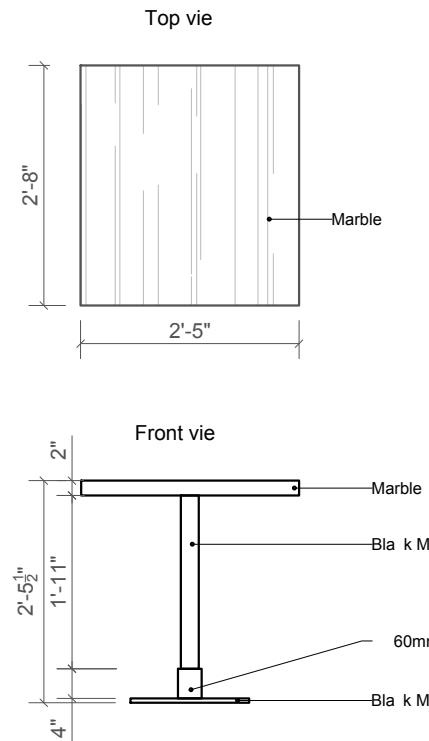


T-2 SCHEME TABLE
Number - 4
Material: Black Metal - legs, Wood - top
32"x29" (810x740mm) h= 29 1/2 " (750mm)

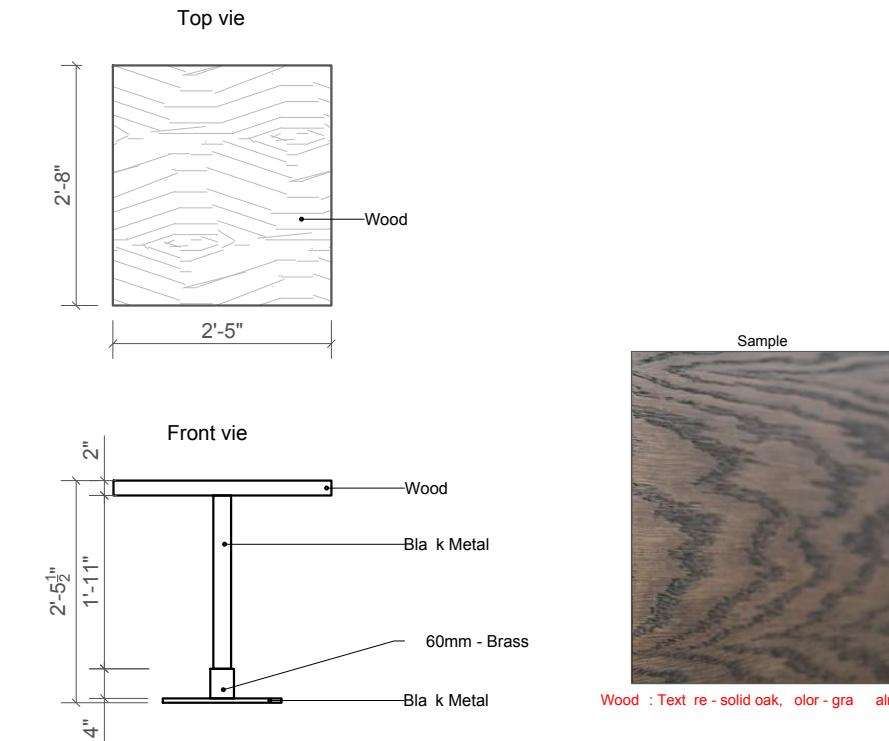

T-3 SCHEME TABLE
Number - 5
Material: Black Metal - legs, Wood - top
50"x32" (1270x810mm) h= 29 1/2 " (750mm)

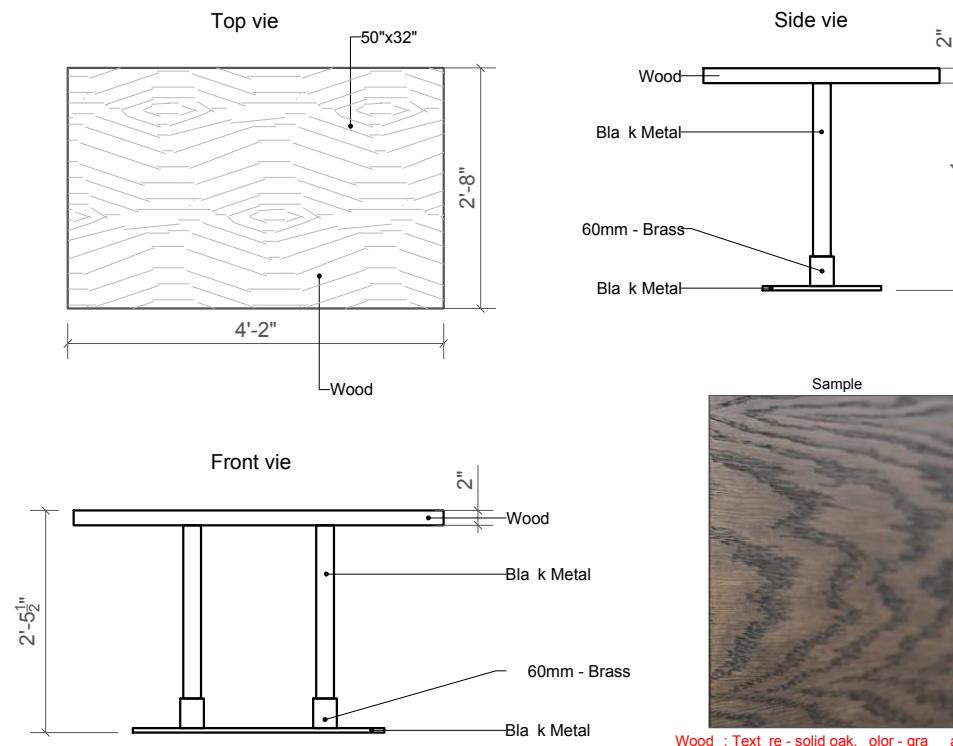

T-4 SCHEME TABLE
Number - 6
Material: Black Metal - legs, Marble - top
50"x32" (1270x810mm) h= 29 1/2 " (750mm)

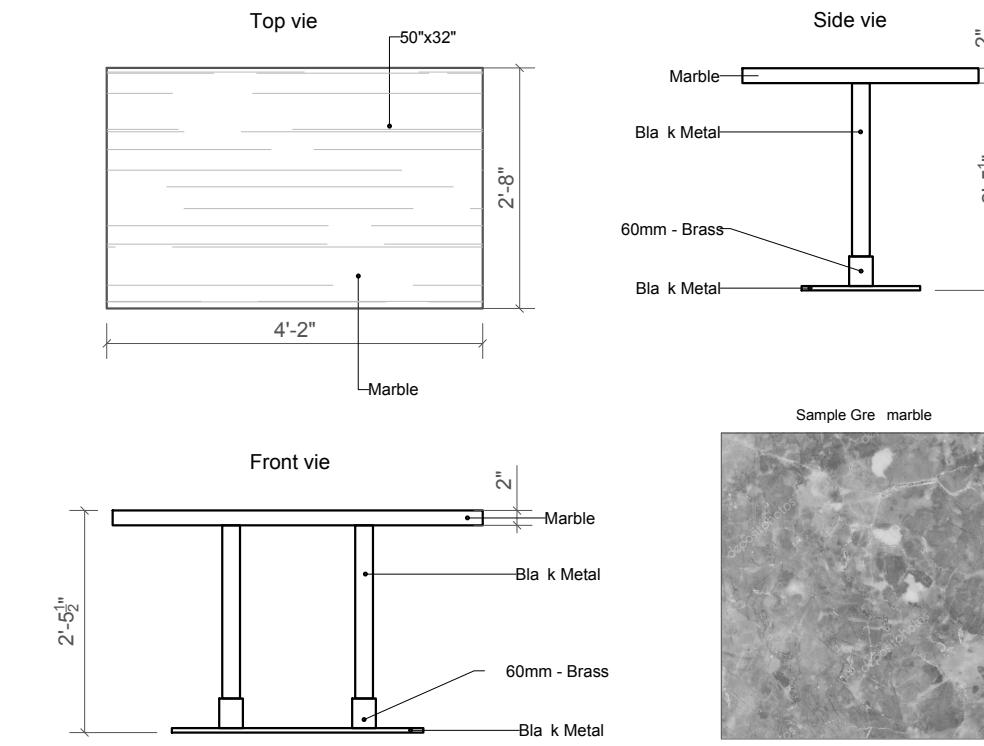

GENERAL NOTES:
 1. ELEVATIONS DEPICTING CABINETS IN DESIGNERS DOCUMENTATION IS FOR DESIGN PURPOSES ONLY;
 2. DESIGNER DOES NOT ASSUME THE RESPONSIBILITY OF ANY STRUCTURAL OR FIELD DIMENSIONS/CONDITIONS;
 3. Vendor shall provide bl eprints;
 4. Get client and designer approvals or materials be ore prod tion

DRAWING TITLE:
FURNITURE
TABLES

DRAWN BY: KEIDUNOV IRINA

SCALE: 1/4"=1'-0"



DATE: 03.21.2022

SHEET : 6.5


A1

RESTAURANT OWL'S NEST



T-5
SCHEME TABLE
N mber - 1
Material: Bla k Metal - legs, Marble - top
36" (915 mm) h= $29\frac{1}{2}$ " (750mm)

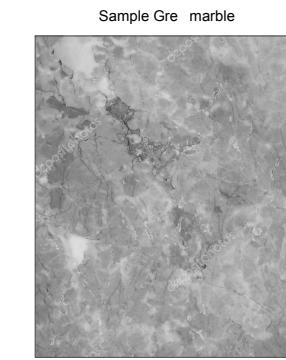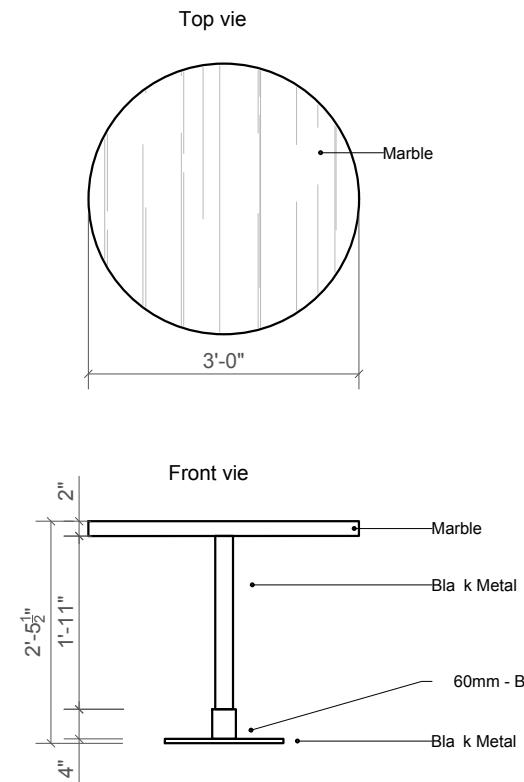

T-7
SCHEME TABLE
N mber - 1
Material: Wood - legs, Wood - top
19" (483 mm) h= 43.3 " (1100mm)

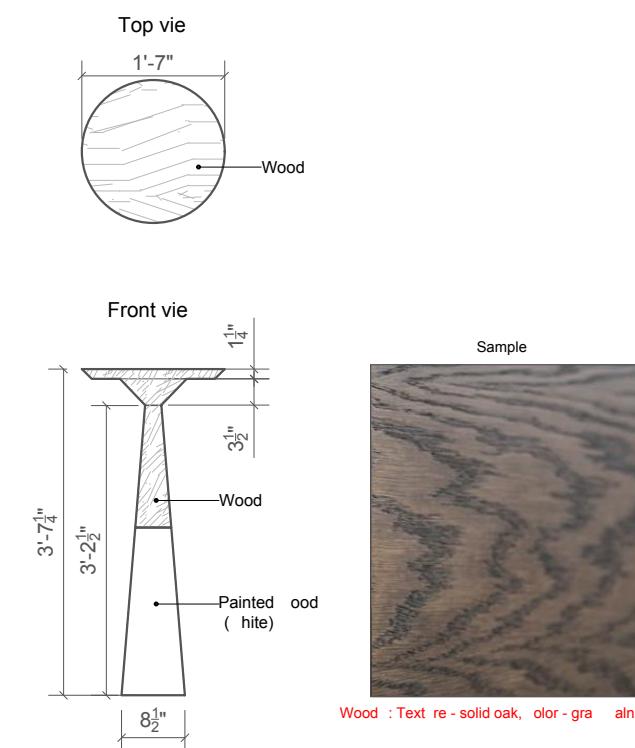

T-6
SCHEME TABLE
N mber - 1
Material: Br shed Brass - legs, Ameri an Waln t - top
92"x39" (2330x990 mm) h= $29\frac{1}{2}$ " (750mm)

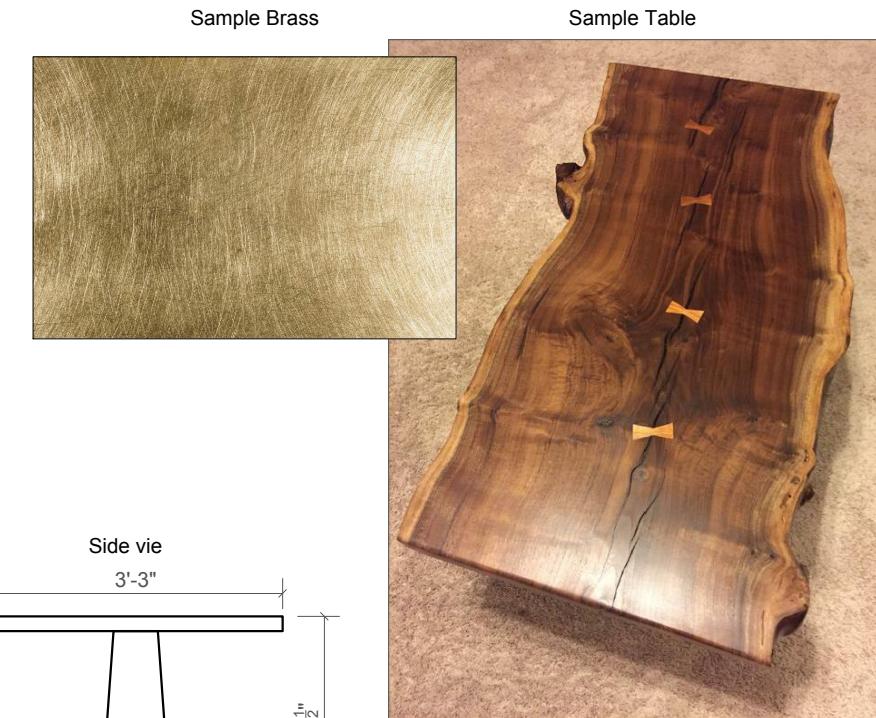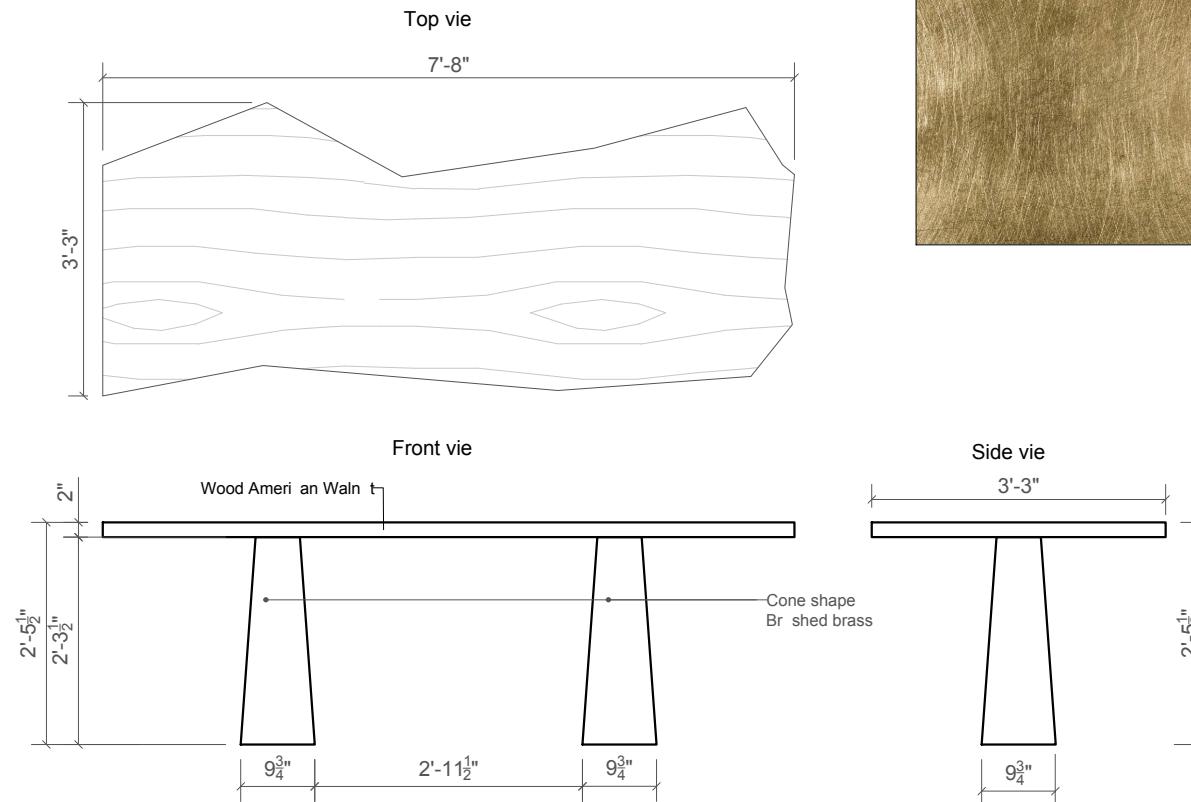

GENERAL NOTES:
 1. ELEVATIONS DEPICTING CABINETS IN DESIGNERS DOCUMENTATION IS FOR DESIGN PURPOSES ONLY;
 2. DESIGNER DOES NOT ASSUME THE RESPONSIBILITY OF ANY STRUCTURAL OR FIELD DIMENSIONS/CONDITIONS;
 3. Vendor shall provide blueprints;
 4. Get client and designer approvals or materials before production

DRAWING TITLE:
FURNITURE
TABLES

DRAWN BY: KEIDUNOV IRINA

SCALE: 1/4"=1'-0"






DATE: 03.21.2022

SHEET : 6.7


A1

S



SCHEME Hostess station
Number - 1
Material: Brass, Wood
41"x30" (1040x762mm) h=45" (1140mm)

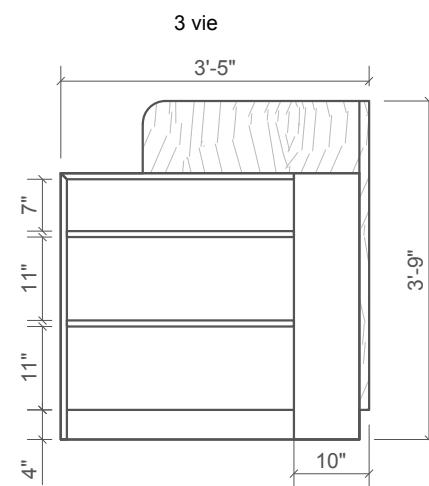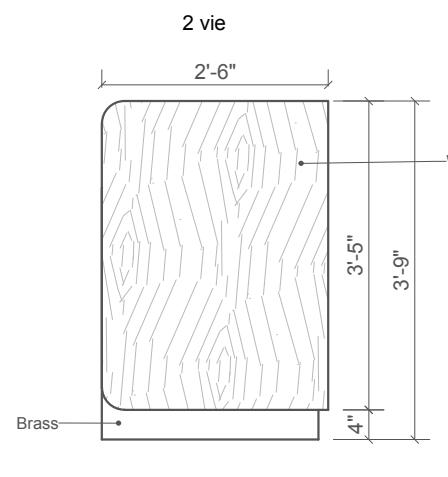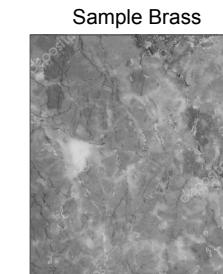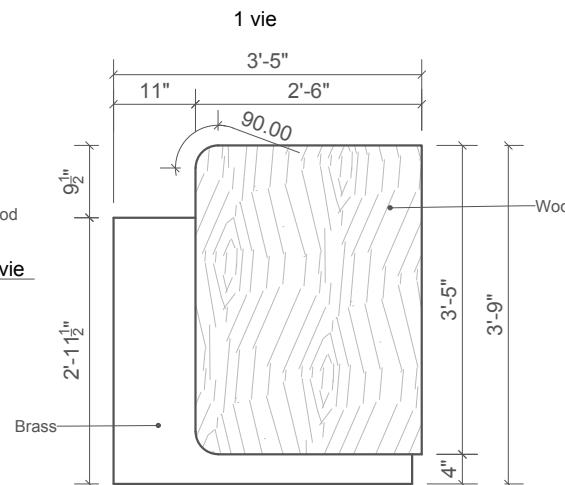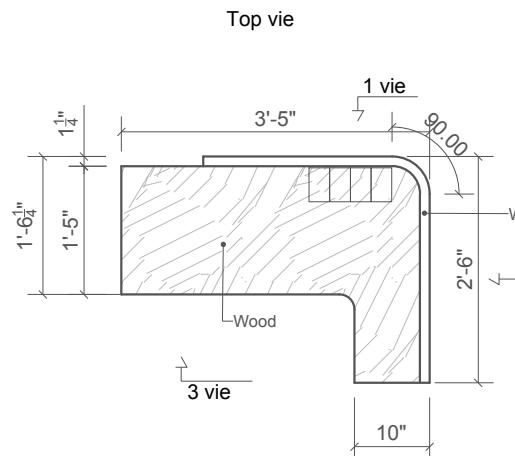**ST-1**

SCHEME Station
Number - 1
Material: Black Metal - legs, Marble - top, Walnut veneer/ Wood - frame
15"x34" (380x3400mm) h= 35" (890mm)

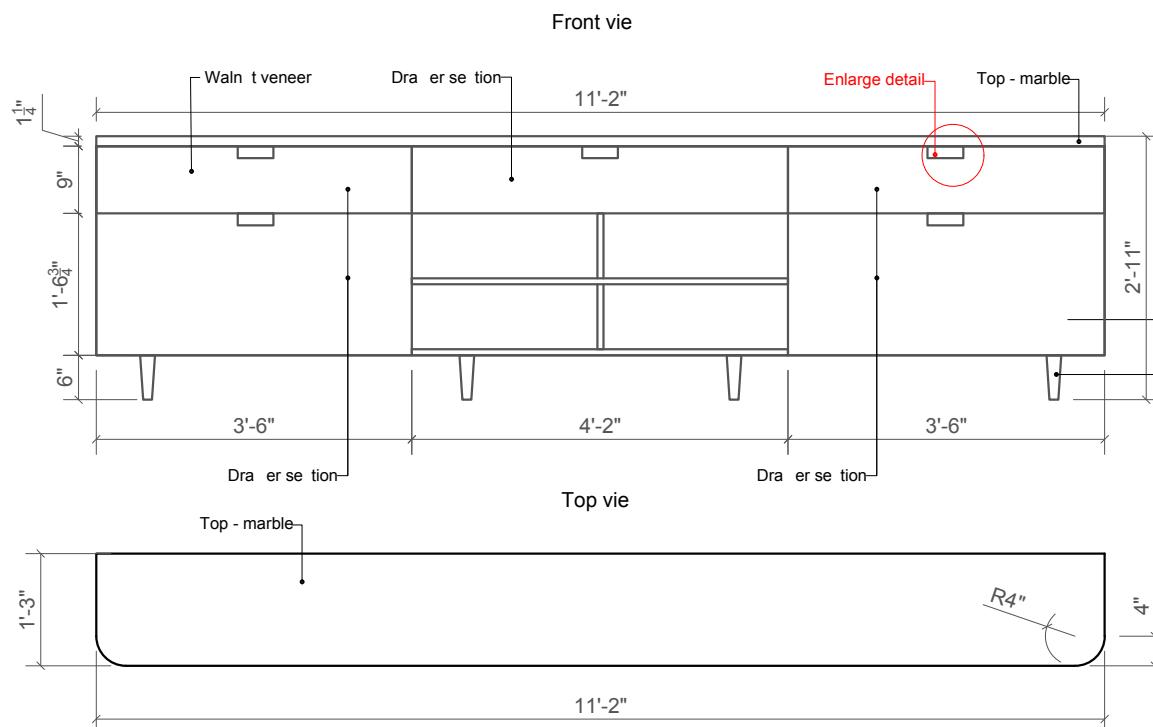**ST-2**

SCHEME Station
Number - 2
Material: Black Metal - legs, Marble - top, Walnut veneer - frame
17"x50" (430x1270mm) h= 41" (1041mm)

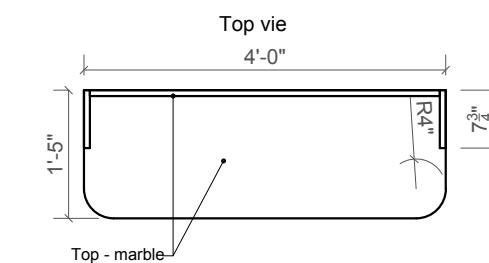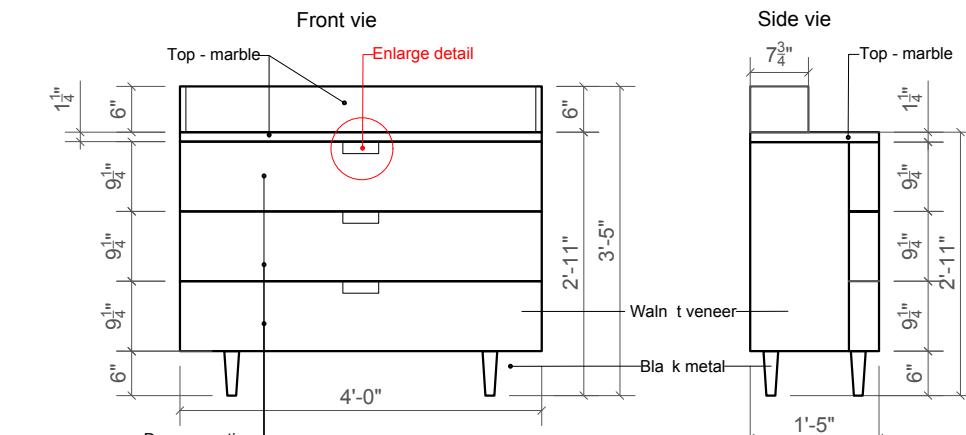


Sample CAPPUCINO VEIN CUT/ DARK EMPERADOR



Sample Wood (Aln t)/Walnut veneer



Enlarge detail

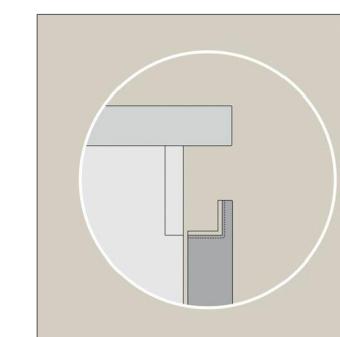

**RESTAURANT
OWL'S NEST**

DRAWING TITLE:
FURNITURE STATIONS

DRAWN BY: KEIDUNOV IRINA

SCALE: 1/4"=1'-0"

DATE: 03.21.2022

SHEET : 6.8






GENERAL NOTES:
1. ELEVATIONS DEPICTING CABINETRY IN DESIGNERS DOCUMENTATION IS FOR DESIGN PURPOSES ONLY;
2. DESIGNER DOES NOT ASSUME THE RESPONSIBILITY OF ANY STRUCTURAL OR FIELD DIMENSIONS/CONDITIONS;
3. Vendor shall provide blueprints;
4. Get client and designer approvals or materials before production

A1


BC SCHEME Book case
Number - 1

Material: Solid wood/MDF Painting - Anthracite Grey (choose the tone of the wall)

Front view

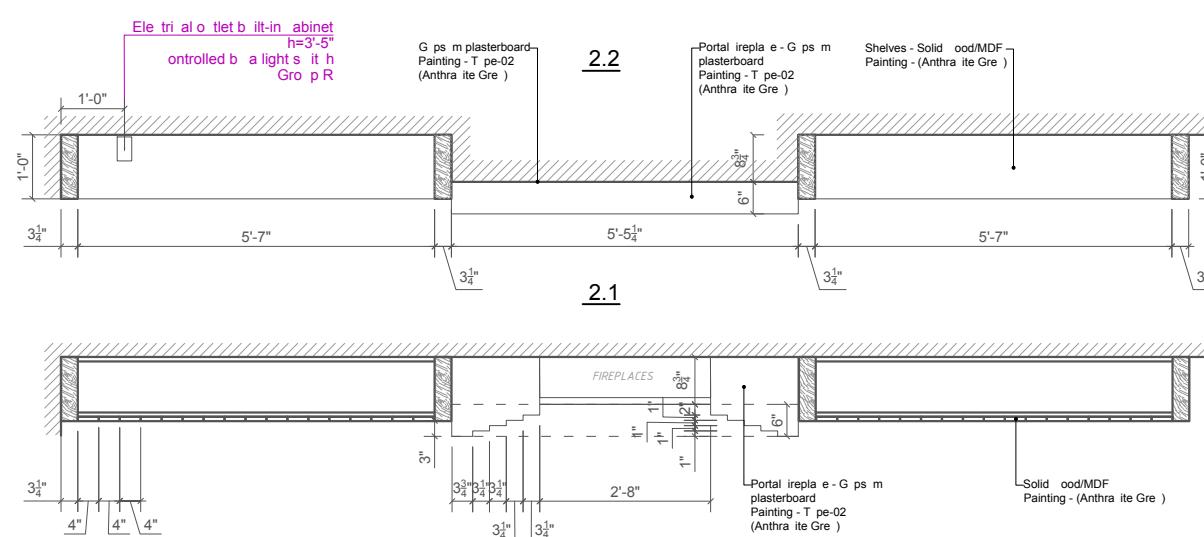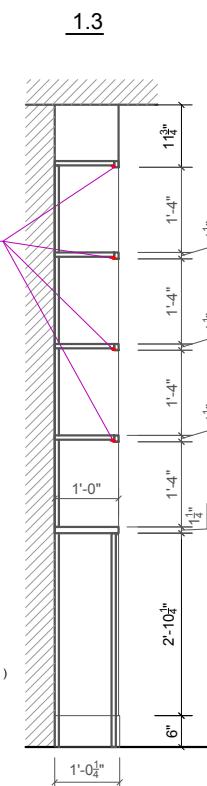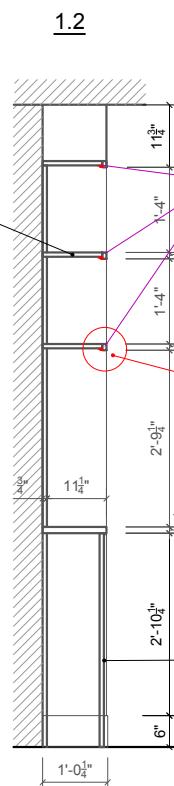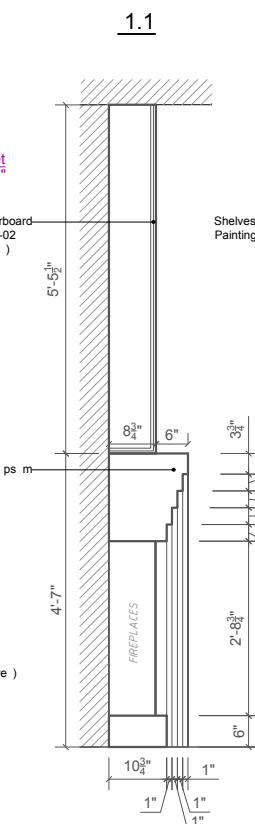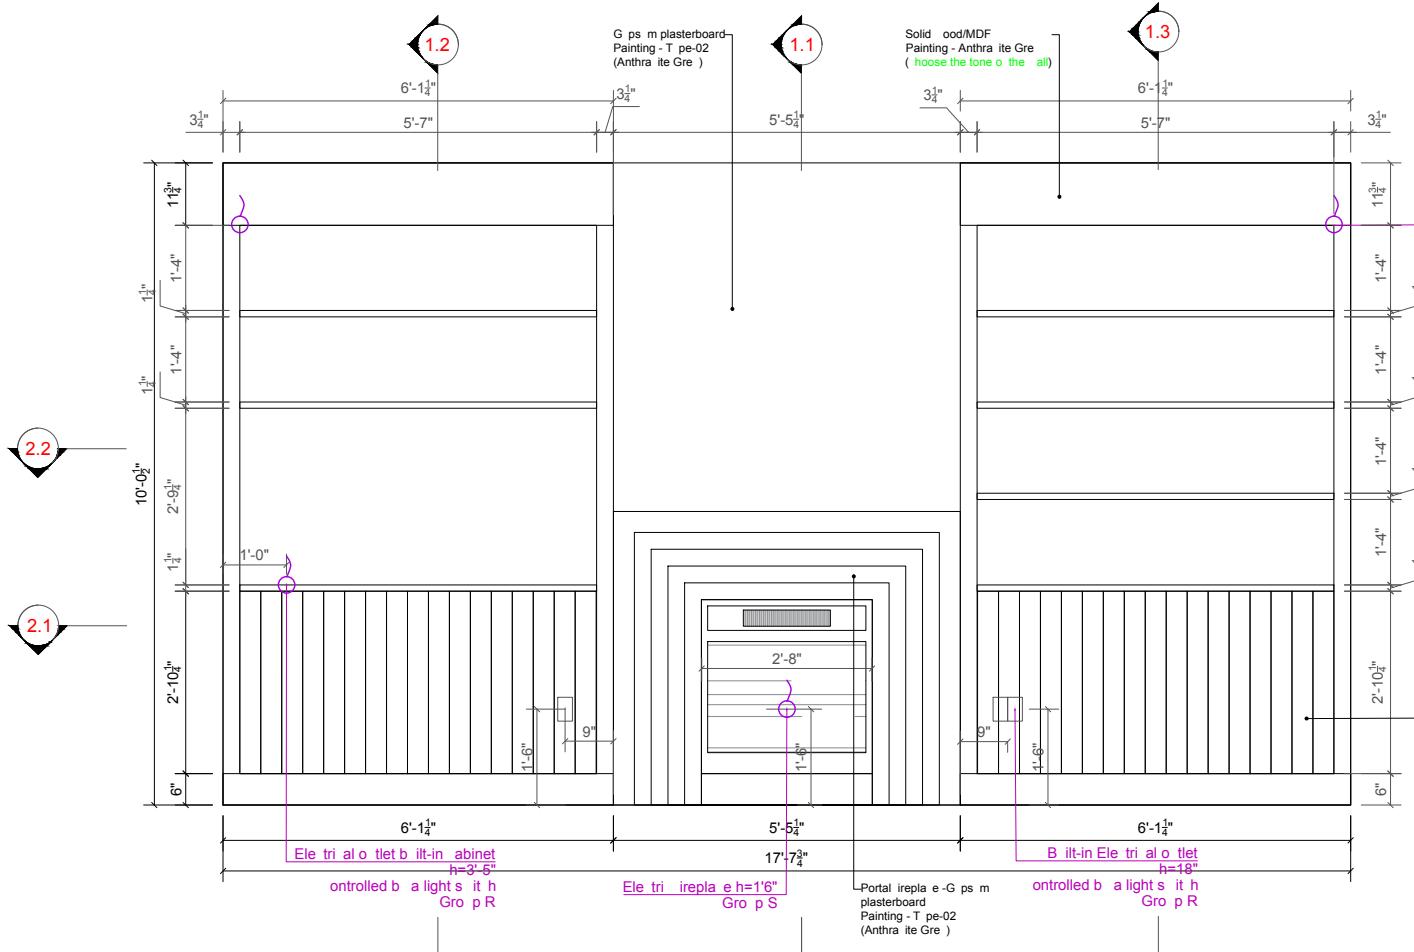

RESTAURANT
OWL'S NEST

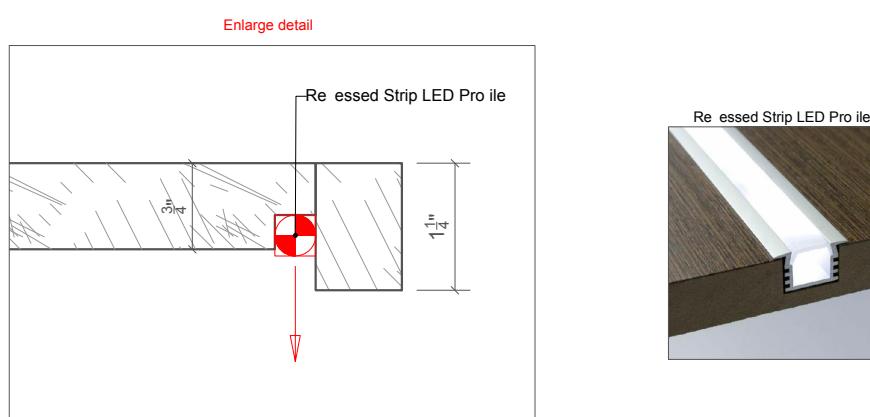

GENERAL NOTES:
 1. ELEVATIONS DEPICTING CABINETRY IN DESIGNERS DOCUMENTATION IS FOR DESIGN PURPOSES ONLY;
 2. DESIGNER DOES NOT ASSUME THE RESPONSIBILITY OF ANY STRUCTURAL OR FIELD DIMENSIONS/CONDITIONS;
 3. Vendor shall provide blueprints;
 4. Get client and designer approvals or materials before production

DRAWING TITLE:
FURNITURE

DRAWN BY: KEIDUNOV IRINA

SCALE: -



DATE: 03.21.2022

SHEET : 6.9

A1

WN

SCHEME Wine room
Number - 1
Material: Brass, Glass

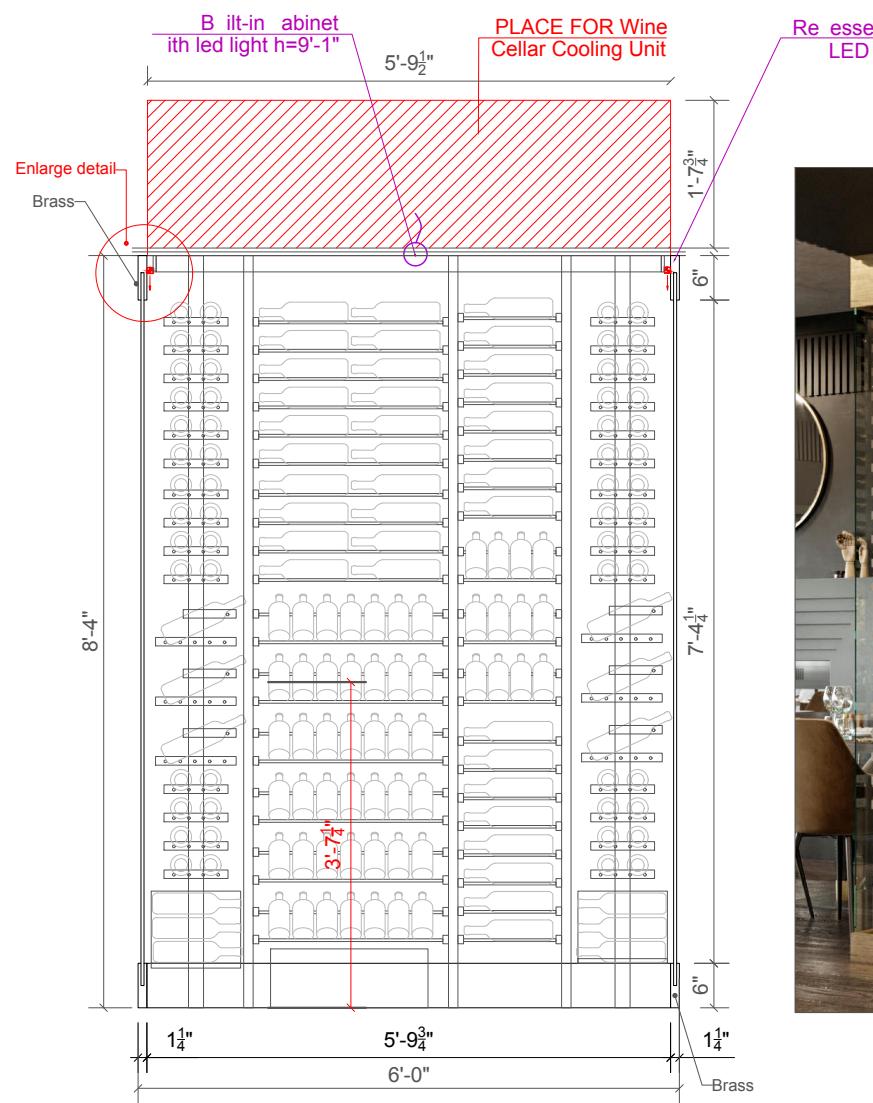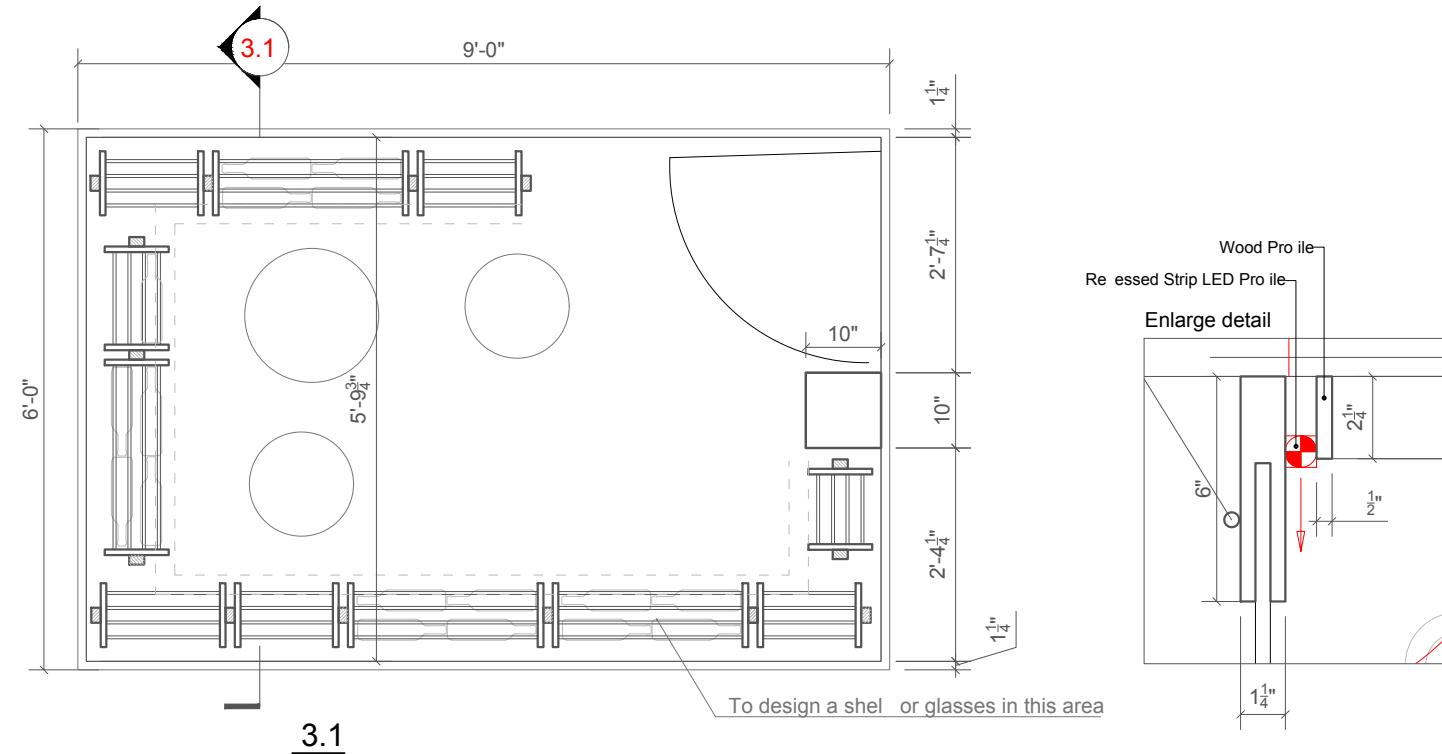

3D visualization



Sample shelves

GENERAL NOTES:
 1. ELEVATIONS DEPICTING CABINETRY IN DESIGNERS DOCUMENTATION IS FOR DESIGN PURPOSES ONLY;
 2. DESIGNER DOES NOT ASSUME THE RESPONSIBILITY OF ANY STRUCTURAL OR FIELD DIMENSIONS/CONDITIONS;
 3. Vendor shall provide bl. prints;
 4. Get client and designer approvals or materials before production;
 5. Wine room gear should be hidden in the ceiling. Strengthen this zone or hanging gear;
 6. Make sure all required glass board hats are in place and their locations approved by designer, client and glass board vendor.

RESTAURANT OWL'S NEST

DRAWING TITLE:
WINE ROOM

DRAWN BY: KEIDUNOV IRINA



SCALE: 1/1"=1'-0"

DATE: 03.21.2022










SHEET : 6.10

A1

RESTAURANT OWL'S NEST

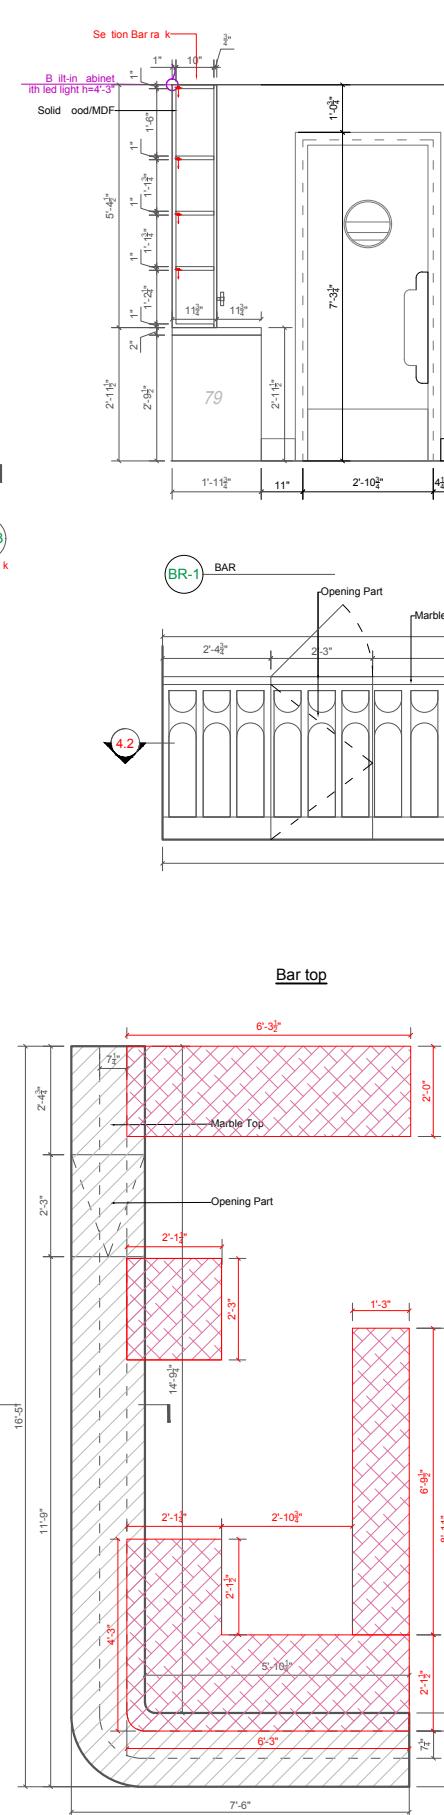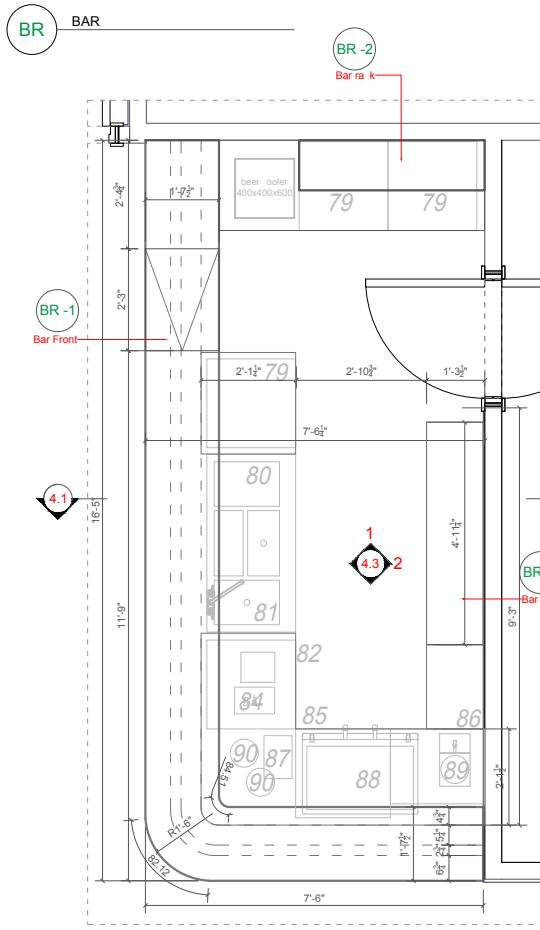

- Work table top - Stainless steel - Guest table top - Marble

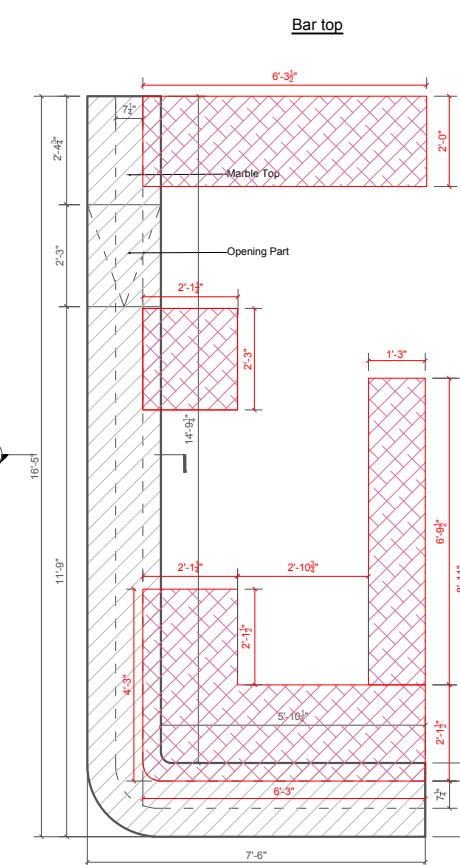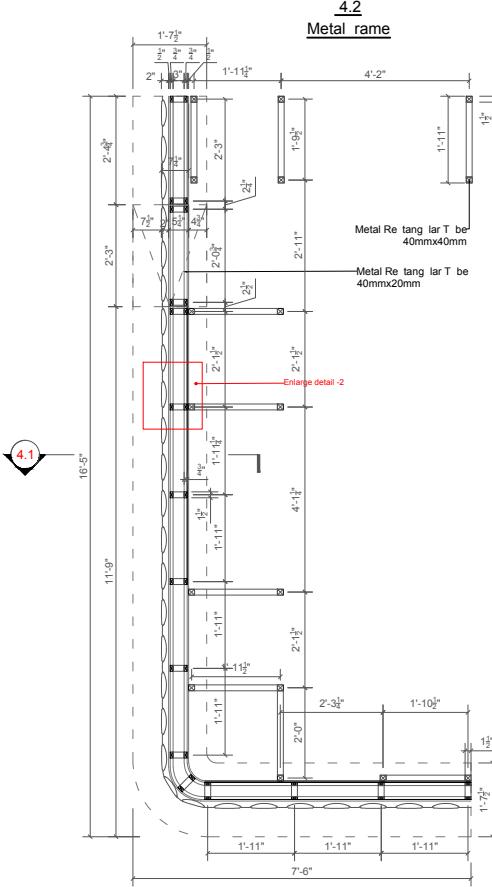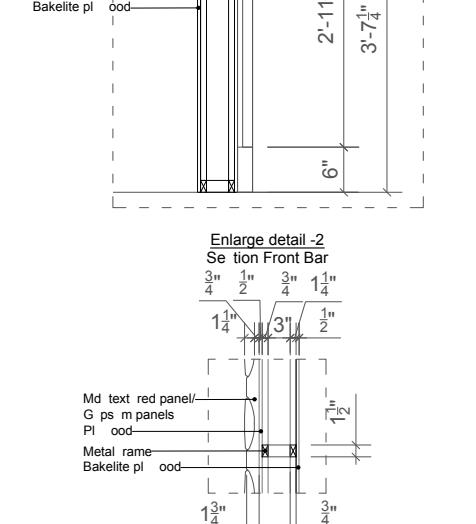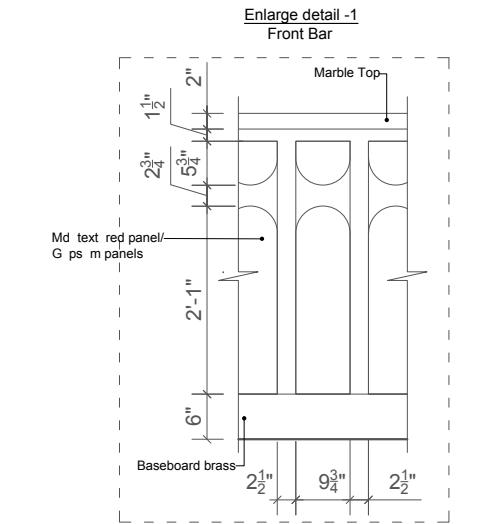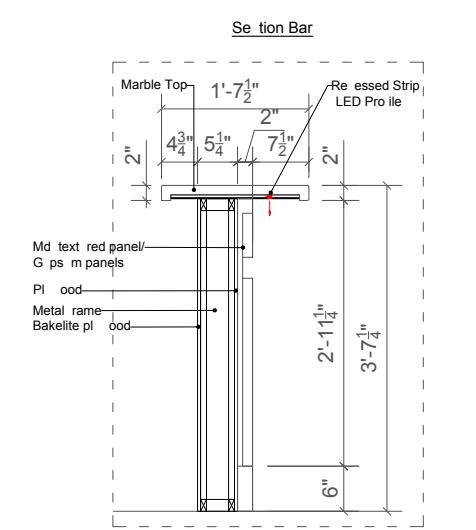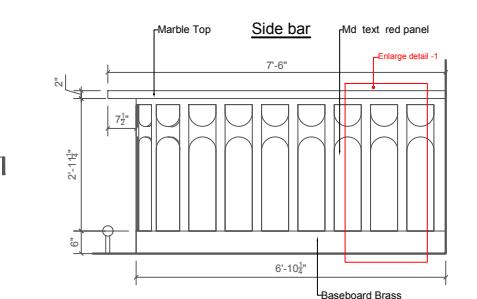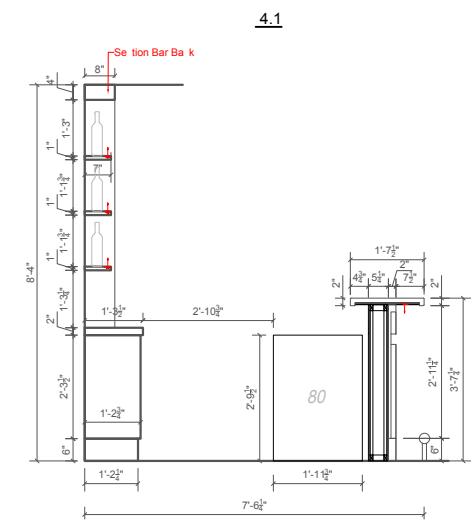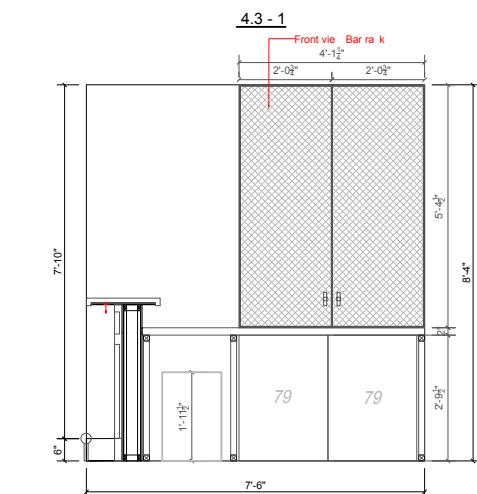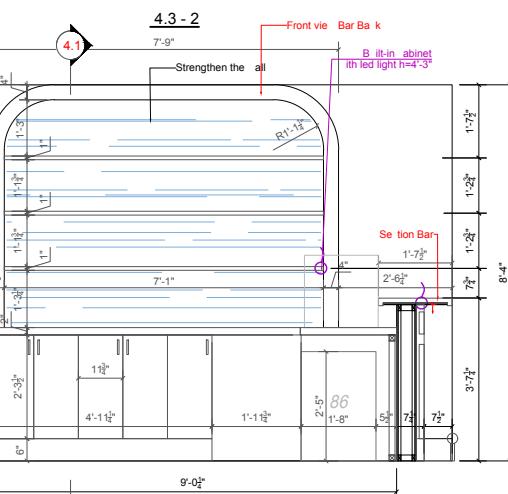

GENERAL NOTES:
 1. elevations depicting abinetr in designers do mentation is or design p poses onl ;
 2. designer does not ass me the responsibilit o an str tial or field dimensions/ conditons;
 3. Vendor shall provide bl eprints;
 4. Get lient and designer approvals or materials be ore prod tion

DRAWING TITLE:
BAR-1






DRAWN BY: KEIDUNOV IRINA

SCALE: 1/2"=1'-0"

DATE: 03.21.2022

SHEET : 6.11

**RESTAURANT
OWL'S NEST**

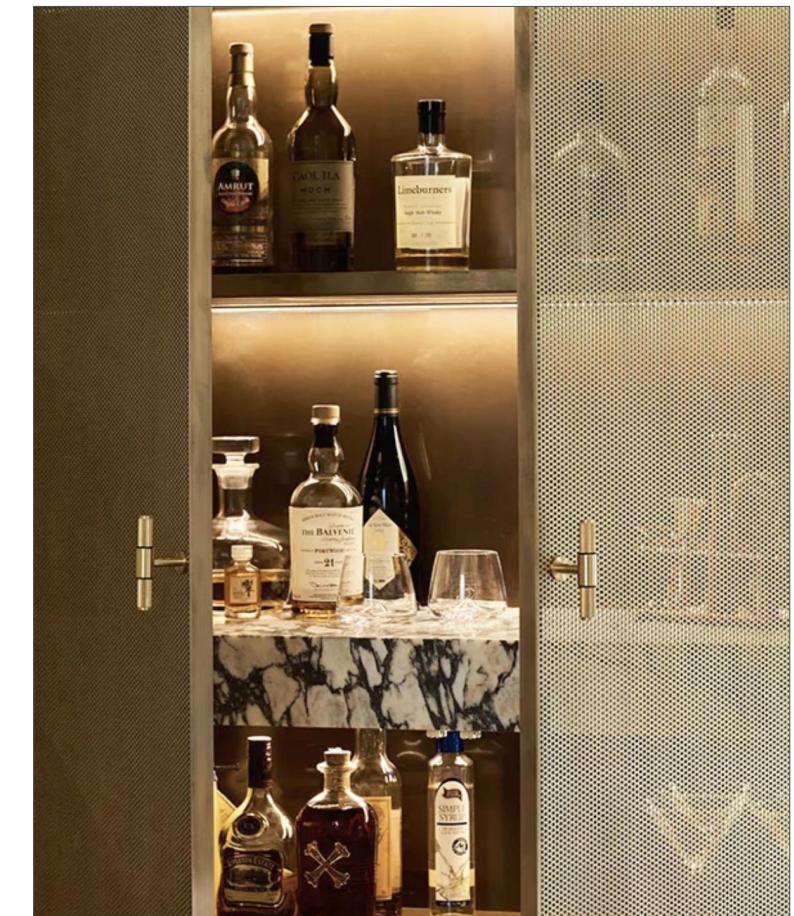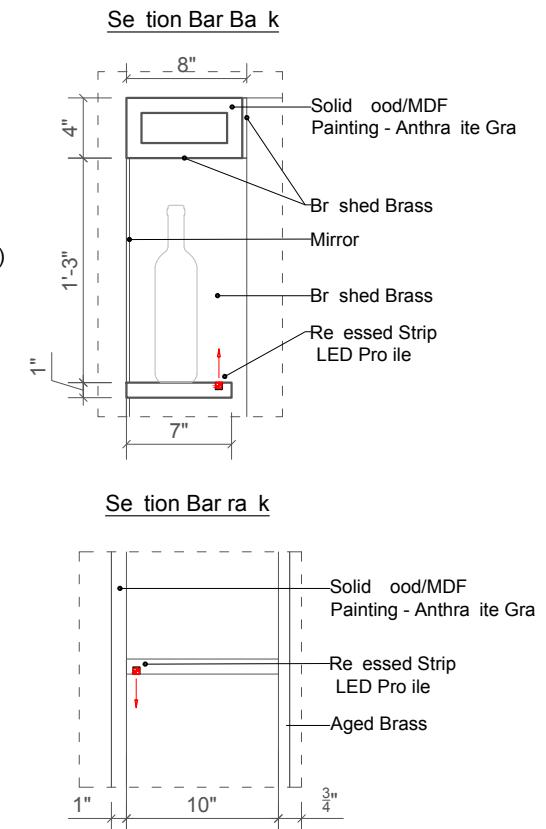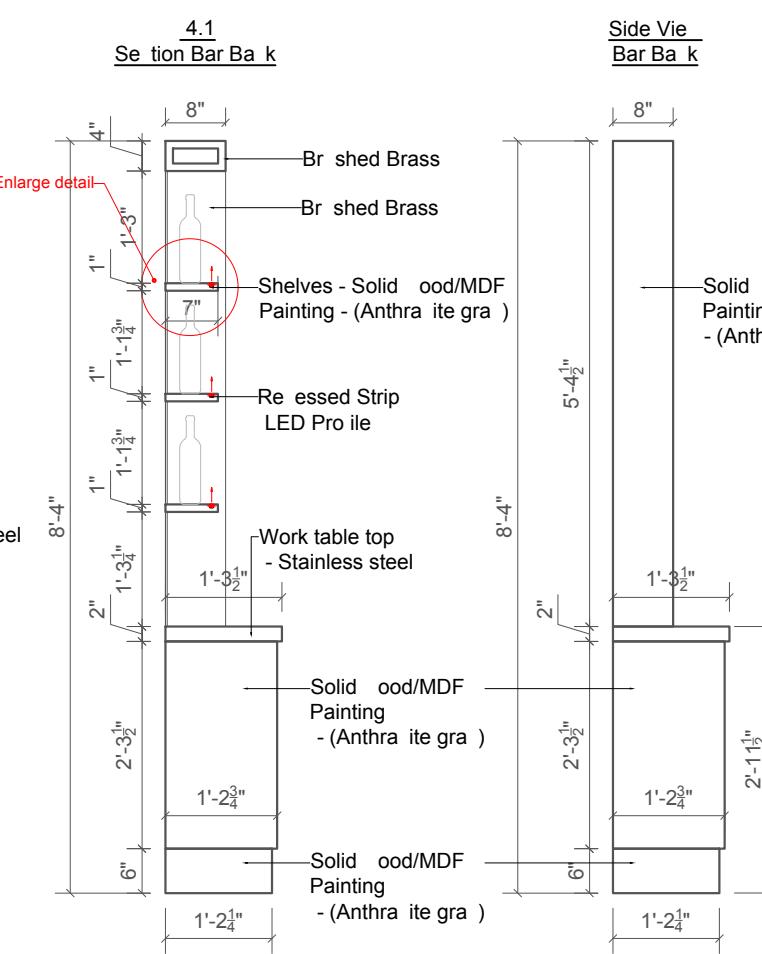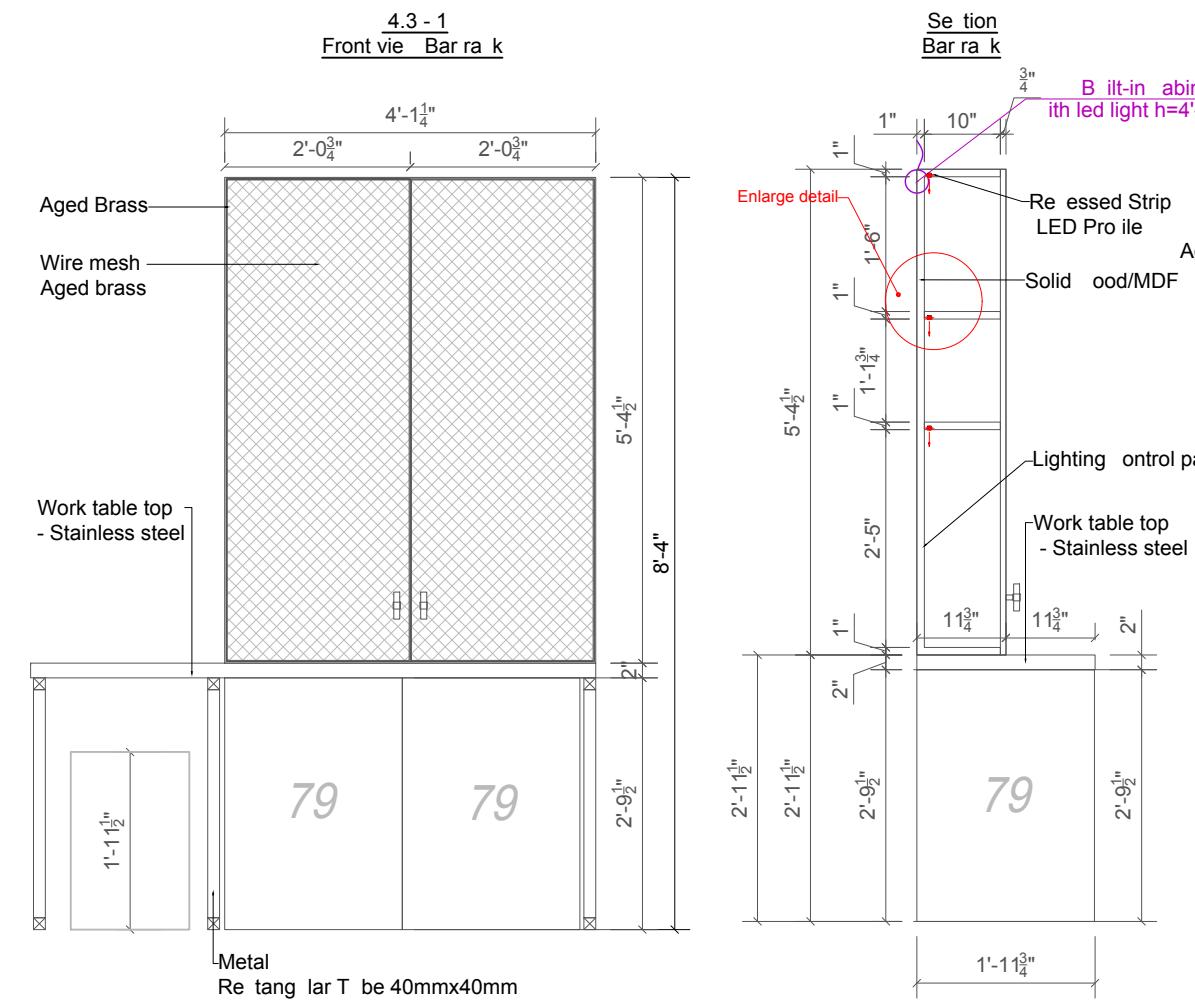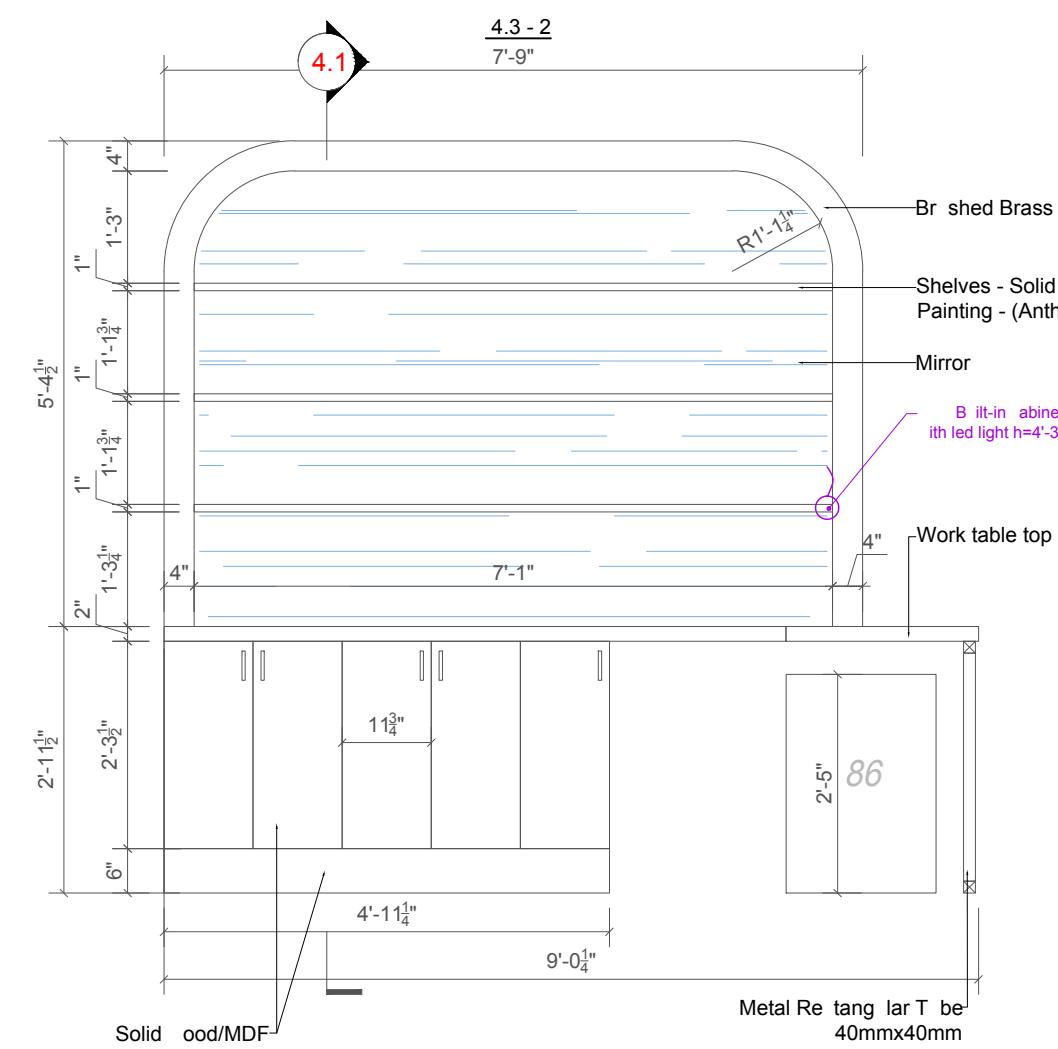

A stainless steel hiske cabinet in aged brass rom proge t "Golden"

DRAWING TITLE:
BAR-2

DRAWN BY: KEIDUNOV IRINA




SCALE: 1/1"=1'-0"

DATE: 03.21.2022

SHEET : 6.12


A1

GENERAL NOTES:
 1. ELEVATIONS DEPICTING CABINETRY IN DESIGNERS DOCUMENTATION IS FOR DESIGN PURPOSES ONLY;
 2. DESIGNER DOES NOT ASSUME THE RESPONSIBILITY OF ANY STRUCTURAL OR FIELD DIMENSIONS/CONDITIONS;
 3. Vendor shall provide bl prints;
 4. Get client and designer approvals or materials before production

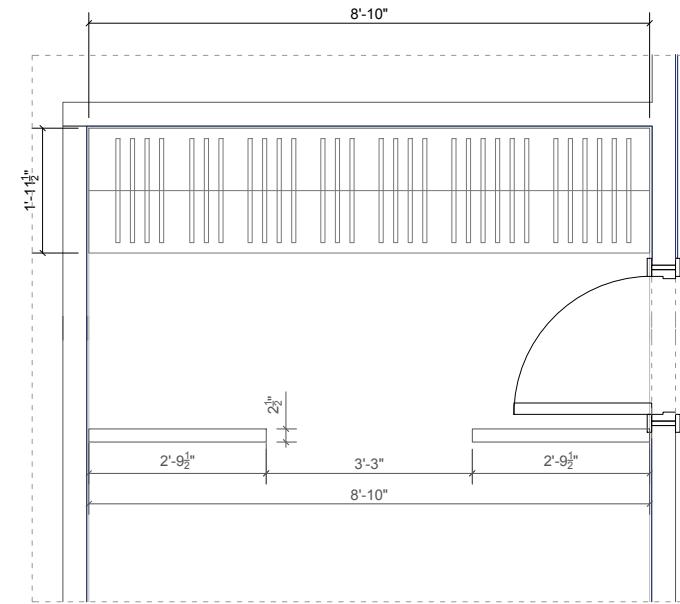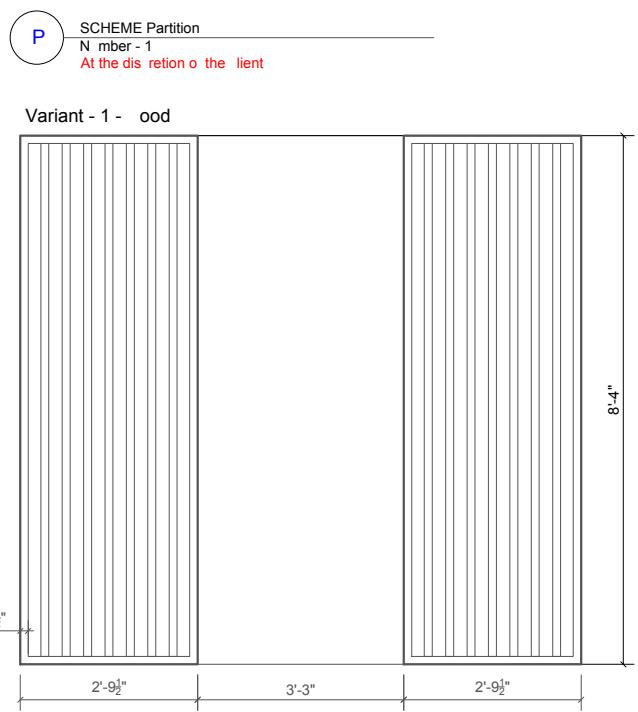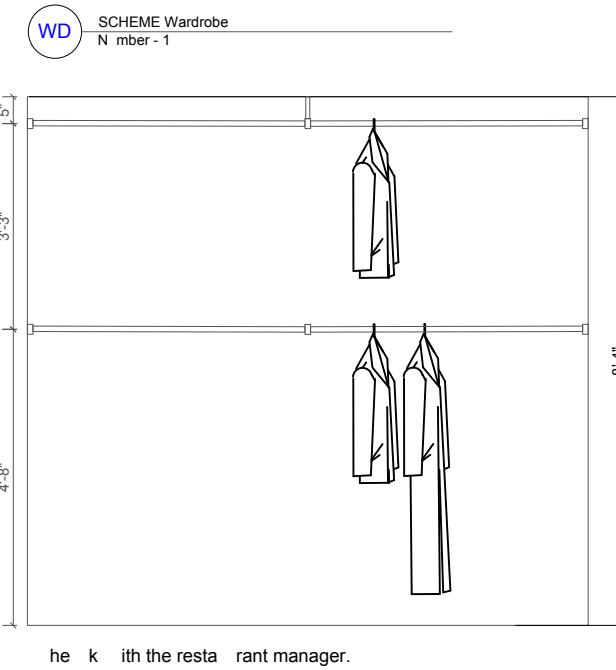

ST Stairs

1. Steps - the same material as floor in the hall (Title). Por elain stone are/Slate. Bla k.) and covered stair r inners (r g r nners)
2. Railing on stairs - To make rom metal ith glass. Metal - re tangle t be 3"x4" painting in bla k. Glass - tempered laminate, panels o 21,52 mm, tinted bronze. Railing on stairs on the all - To make rom metal painting in bla k.

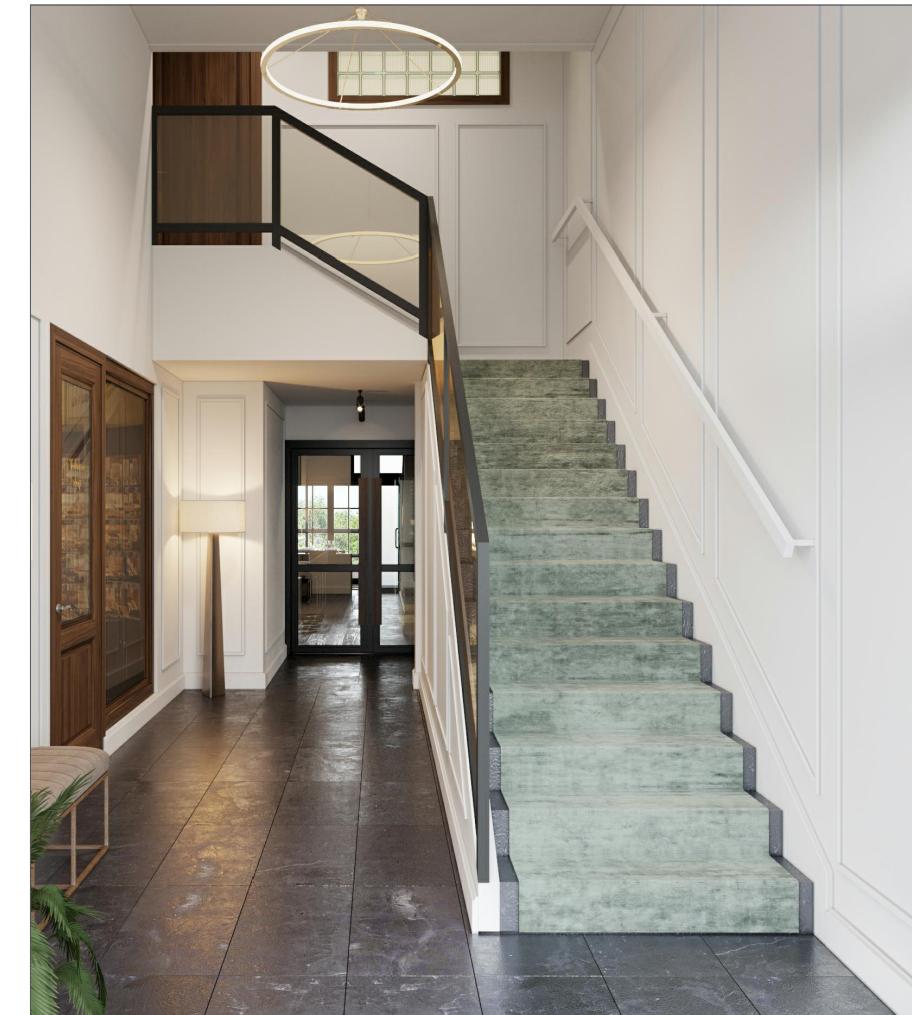

Variant - 2 Metal partition ith matte glass (Reeded glass)



RESTAURANT OWL'S NEST

DRAWING TITLE:
WARDROBE AND
STAIRS

DRAWN BY: KEIDUNOV IRINA

SCALE: 1/1"=1'-0"


DATE: 03.21.2022

SHEET : 6.13


GENERAL NOTES:
1. ELEVATIONS DEPICTING CABINERY IN DESIGNERS DOCUMENTATION IS FOR DESIGN PURPOSES ONLY;
2. DESIGNER DOES NOT ASSUME THE RESPONSIBILITY OF ANY STRUCTURAL OR FIELD DIMENSIONS/CONDITIONS;

M-1, CT-1 SCHEME Mirror and Counterop Sink area de oration (or MALE)
N mber - 1


Top vie

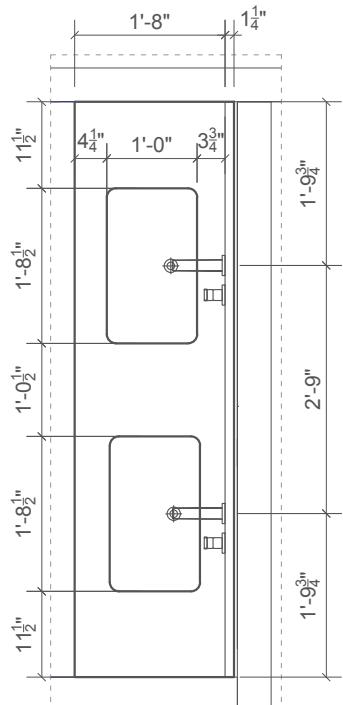

Front vie

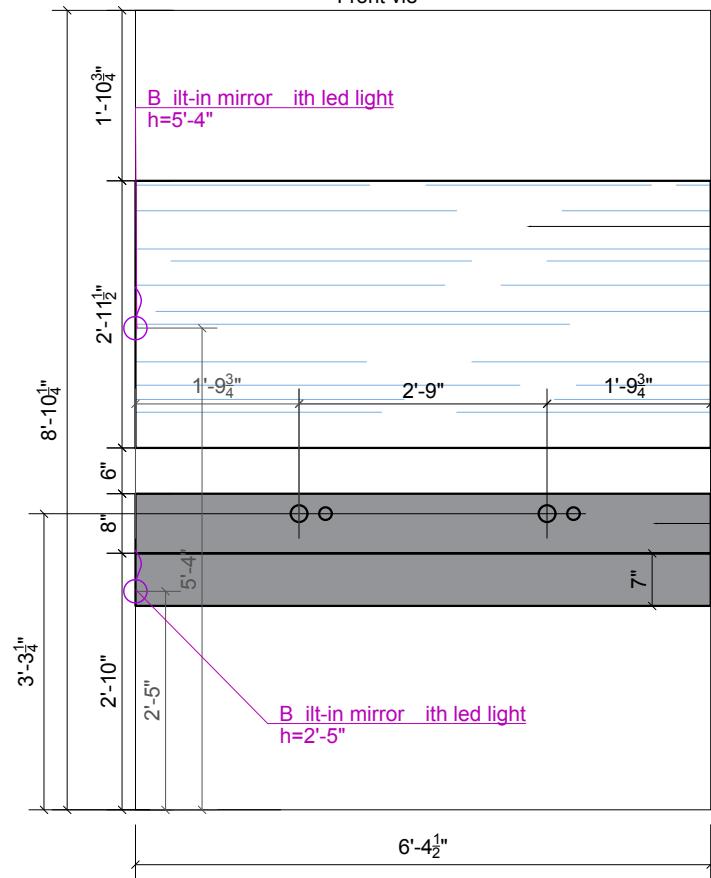


Se tion

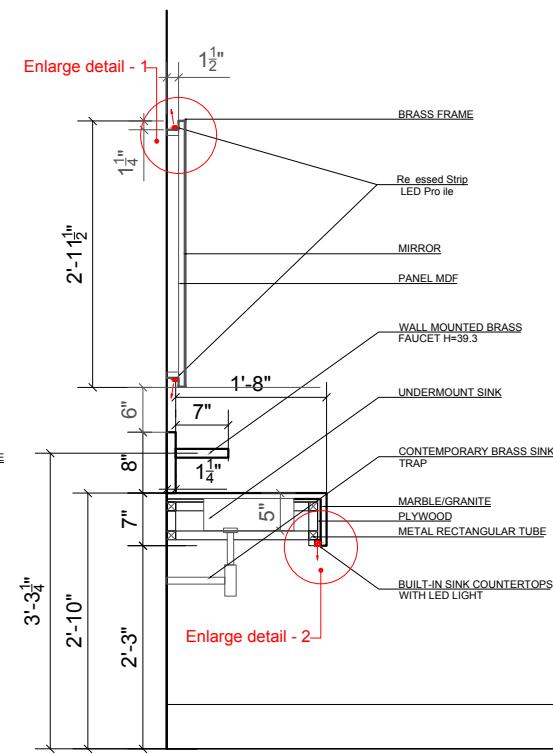


Sample Granite - Titanium Gold Granite



Enlarge detail - 1

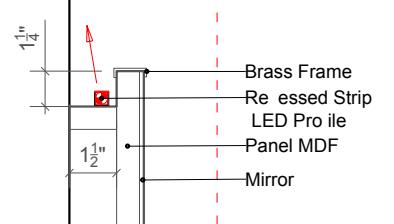


Enlarge detail - 2

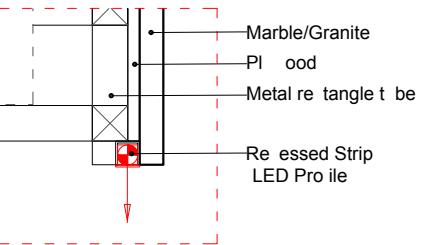


RESTAURANT
OWL'S NEST

M-2, CT-2 SCHEME Mirror and Counterop Sink area de oration (or FEMALE)
N mber - 1


Top vie

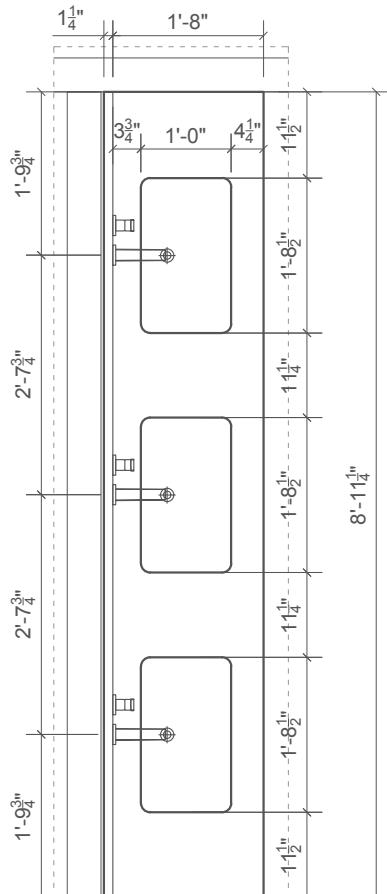

Front vie

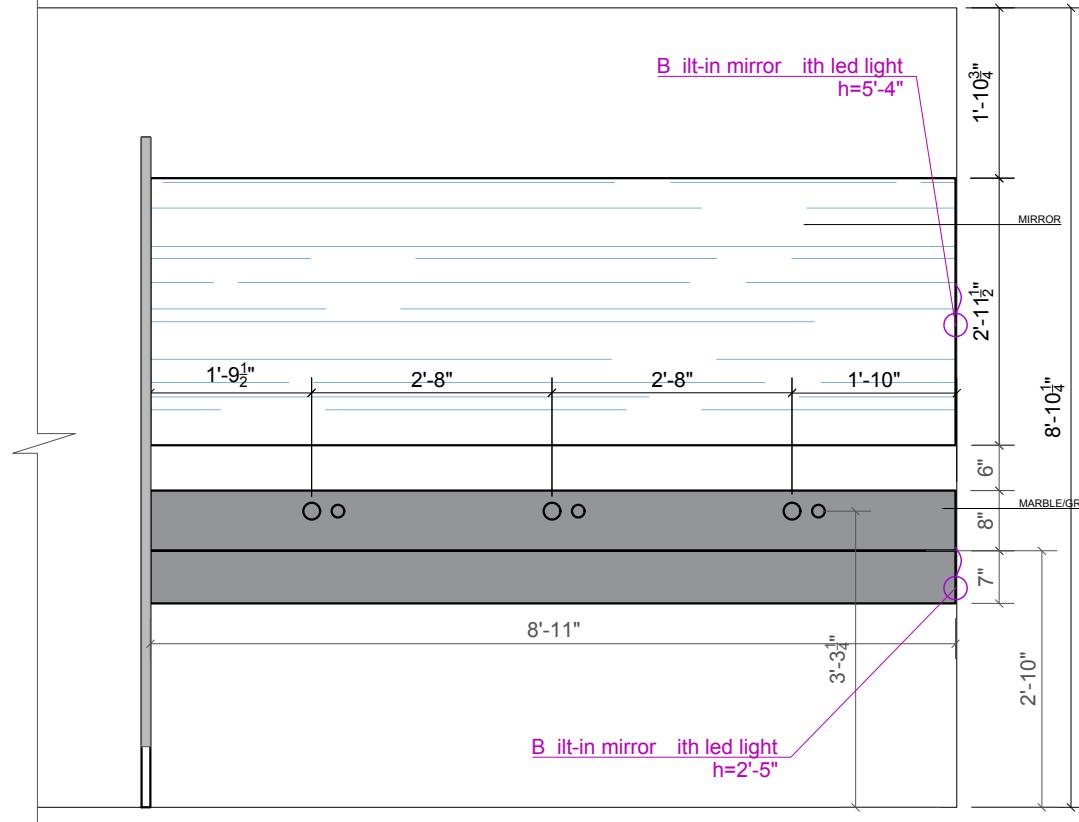

Se tion

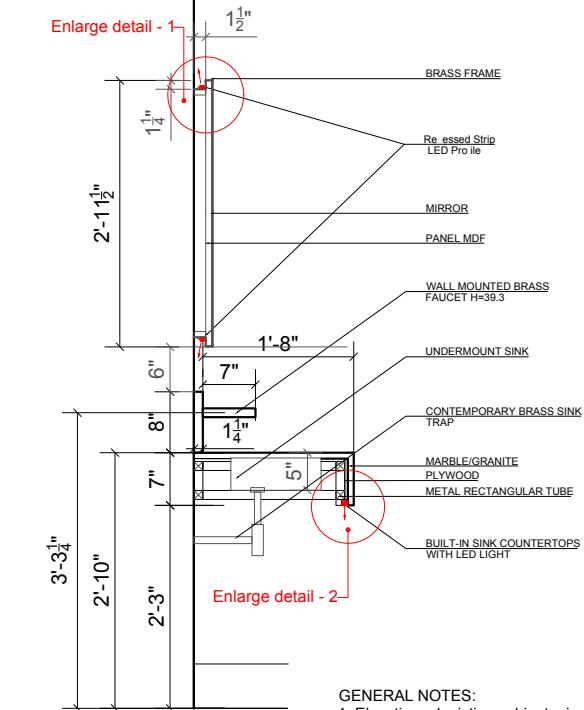

GENERAL NOTES:

1. Elevations depicting cabinetry in designers documentation is for design purposes only;
2. Designer does not assume the responsibility for structural or field dimensions/ conditions;
3. Vendor shall provide blueprints;
4. Get client and designer approvals for materials before production;
5. Make holes in the counter according to the specification on the sink and mixer tap are finalized.

DRAWING TITLE:
MIRROR AND
COUNTEROP SINK





DRAWN BY: KEIDUNOV IRINA

SCALE: 1/1=1'-0"

DATE: 03.21.2022

SHEET : 6.14

Scheme Partition
P-1, P-2

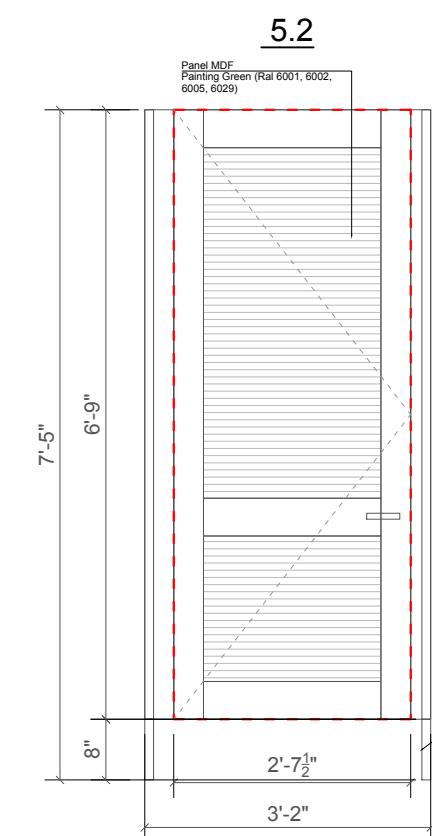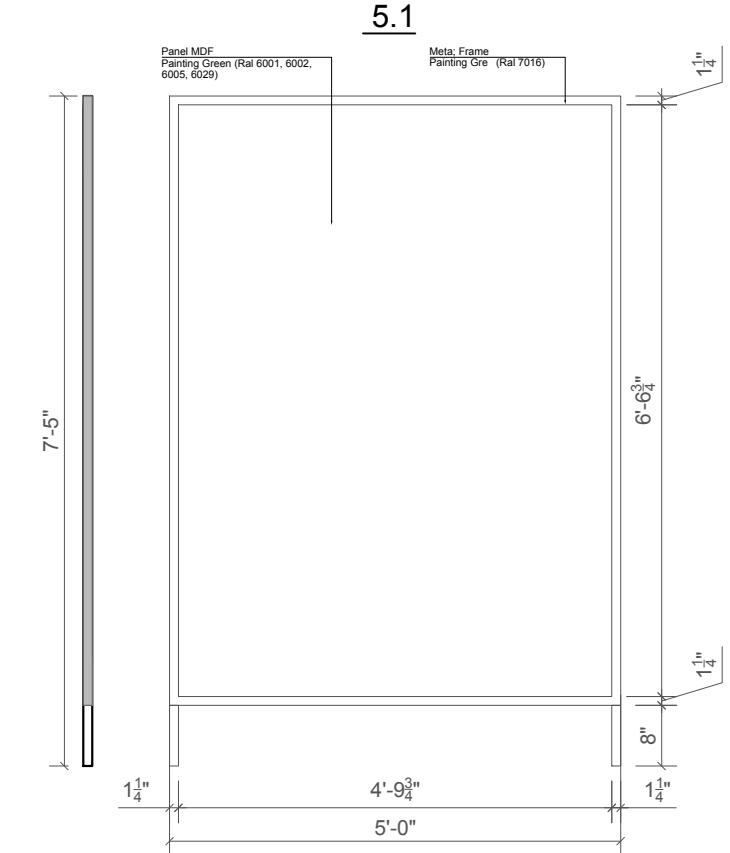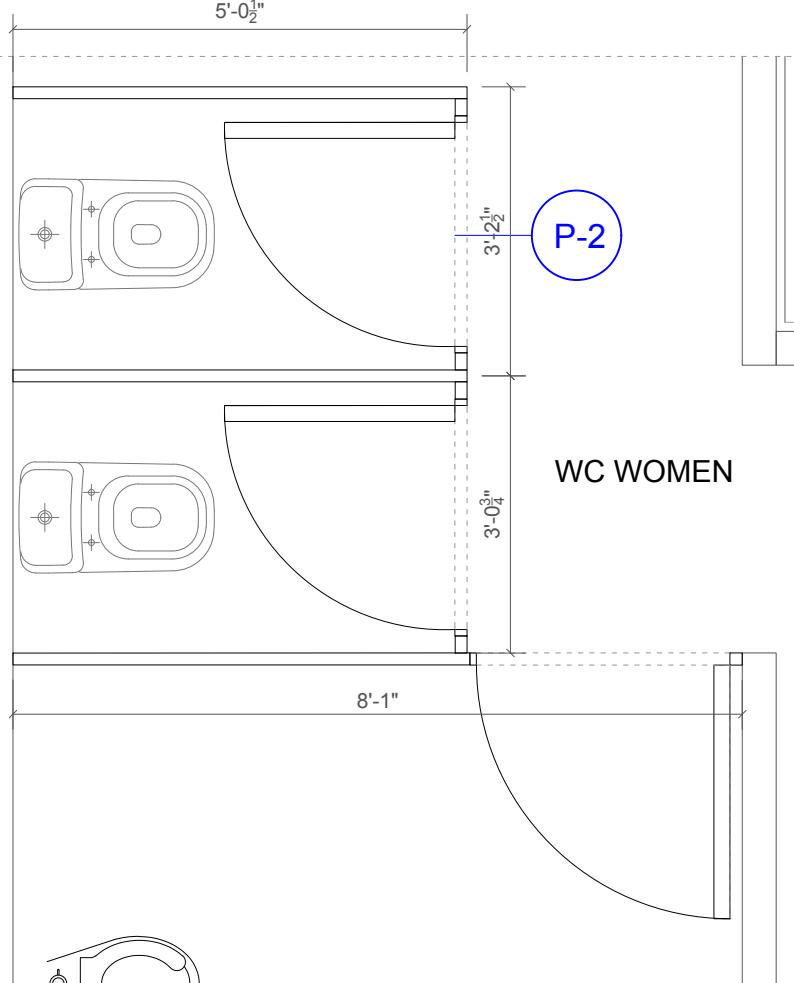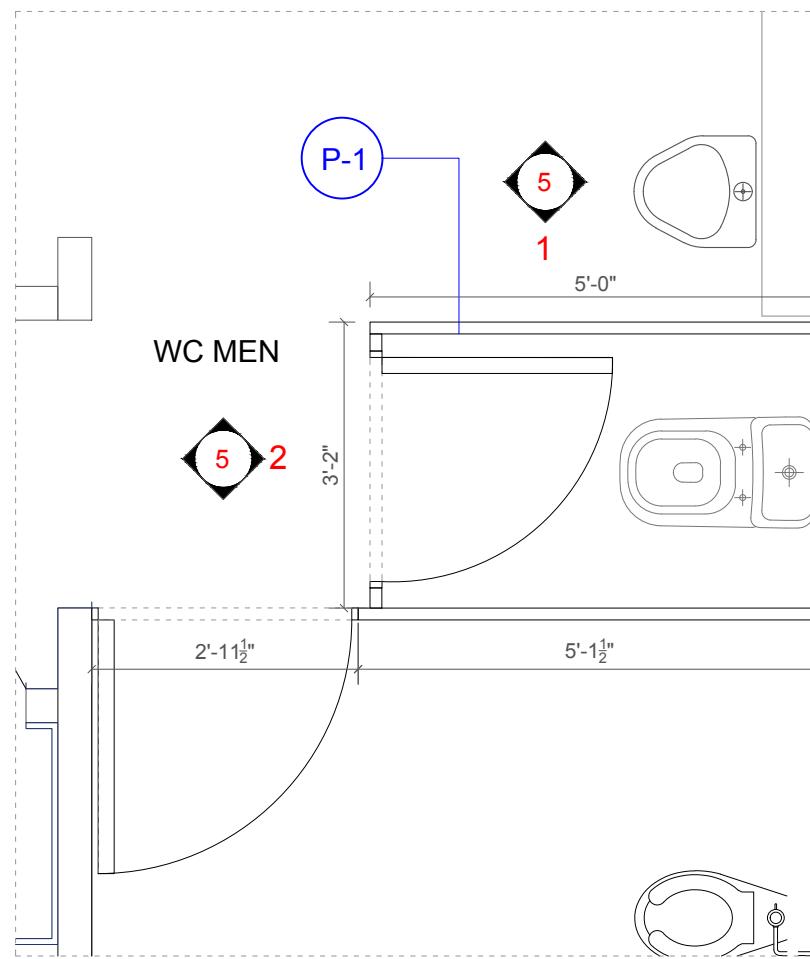

3D visualization



Sample Priva Door Lever - Br shed brass

RESTAURANT OWL'S NEST

DRAWING TITLE:

PARTITIONS IN WC

DRAWN BY: KEIDUNOV IRINA

SCALE: 1/1"=1'-0"




DATE: 03.21.2022

SHEET : 6.15

A1

GENERAL NOTES:

1. ELEVATIONS DEPICTING CABINETRY IN DESIGNERS DOCUMENTATION IS FOR DESIGN PURPOSES ONLY;
2. DESIGNER DOES NOT ASSUME THE RESPONSIBILITY OF ANY STRUCTURAL OR FIELD DIMENSIONS/CONDITIONS;
3. Vendor shall provide blueprints;
4. Get client and designer approvals or materials before production;
5. PREPARE SEVERAL VARIANT SAMPLES (RAL6001, 6002, 6005, 6029) AND APPROVE BY CLIENT ON SITE.

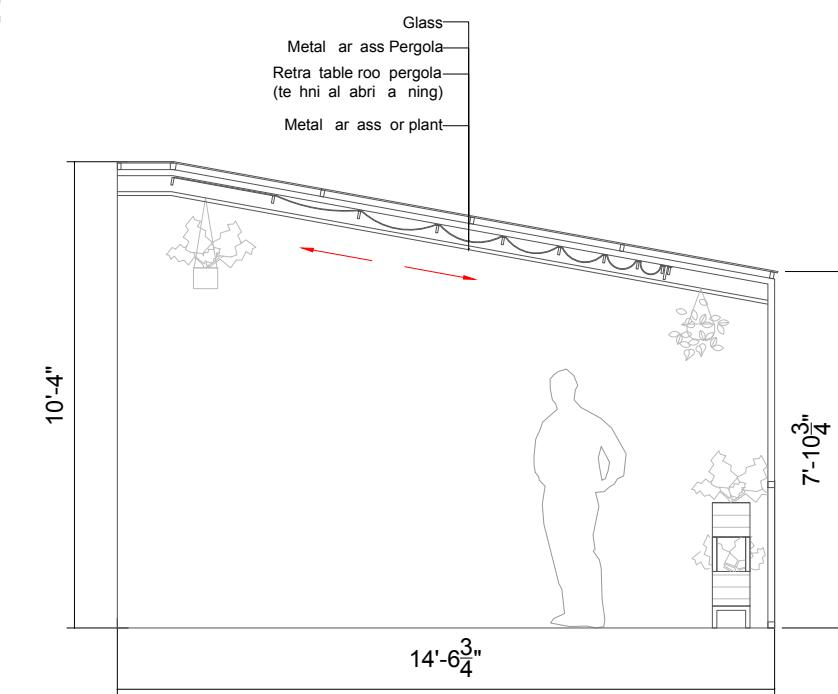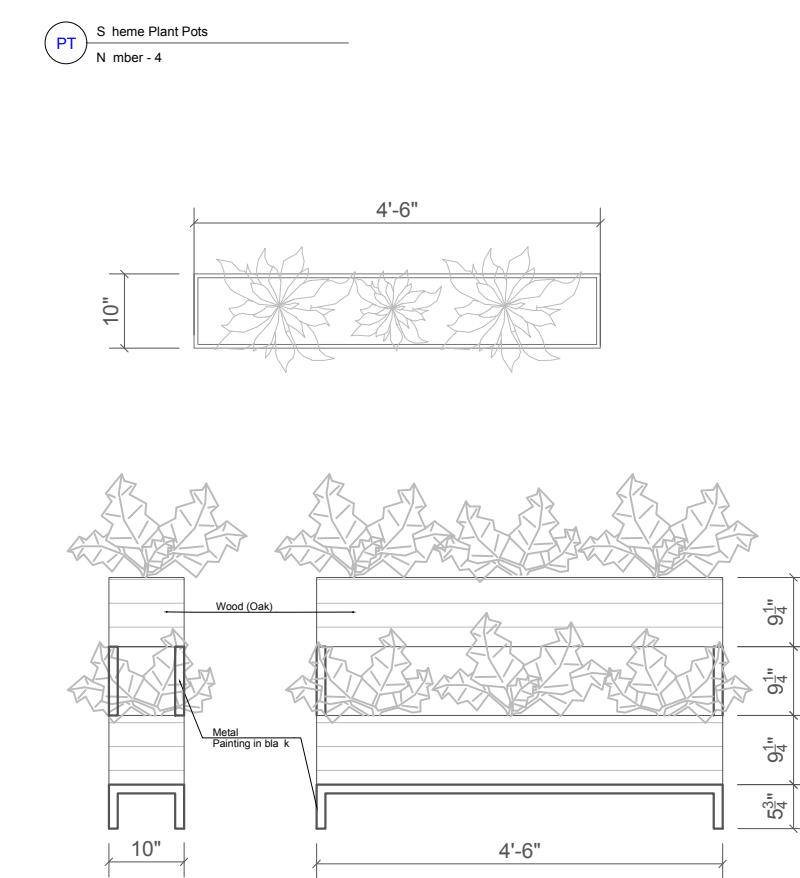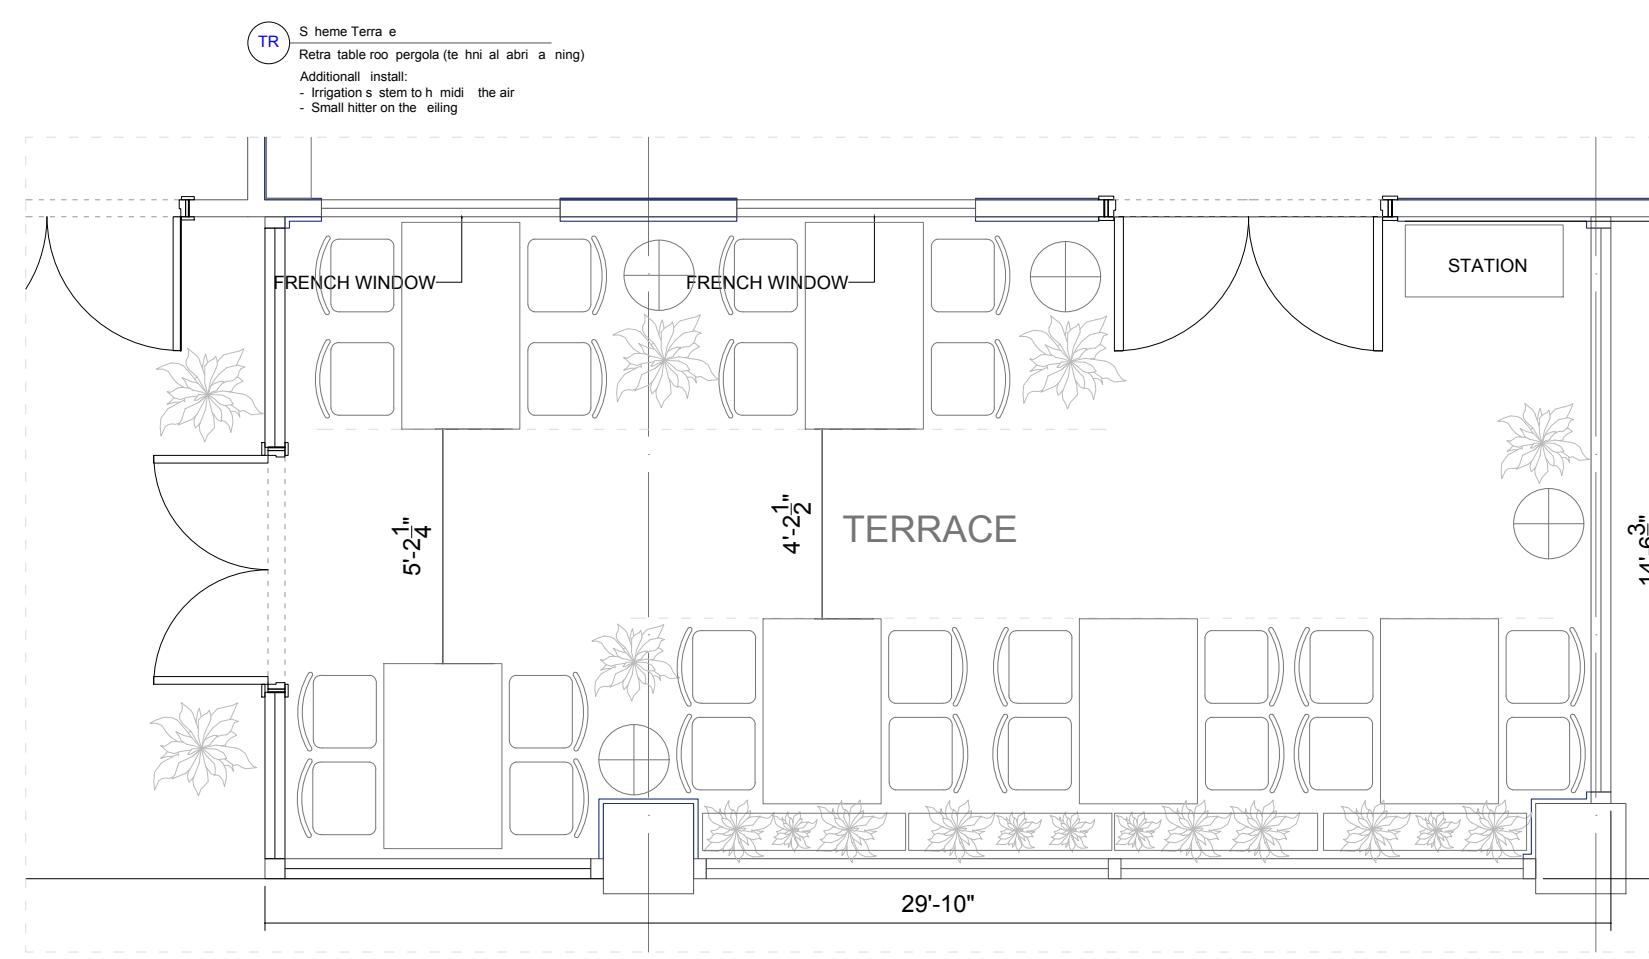

**RESTAURANT
OWL'S NEST**

DRAWING TITLE:
TERRACE

DRAWN BY: KEIDUNOV IRINA

SCALE: 1/2"=1'-0"

DATE: 03.21.2022

SHEET : 6.16

GENERAL NOTES:
1. ELEVATIONS DEPICTING CABINETS IN DESIGNERS DOCUMENTATION IS FOR DESIGN PURPOSES ONLY;
2. DESIGNER DOES NOT ASSUME THE RESPONSIBILITY OF ANY STRUCTURAL OR FIELD DIMENSIONS/CONDITIONS;

FURNITURE, LIGHTNING AND PLANTS



RESTAURANT OWL'S NEST

DRAWING TITLE:
FURNITURE LAYOUT

DRAWN BY: KEIDUNOV IRINA

SCALE: 1/4"=1'-0"

DATE: 05.27.2022

SHEET : 7.1

GENERAL NOTES:
 1. ELEVATIONS DEPICTING CABINETS IN DESIGNERS DOCUMENTATION IS FOR DESIGN PURPOSES ONLY;
 2. DESIGNER DOES NOT ASSUME THE RESPONSIBILITY OF ANY STRUCTURAL OR FIELD DIMENSIONS/CONDITIONS;

A1

FURNITURE:

	<u>Code</u>	<u>Name</u>	<u>Pi t re</u>	<u>N mber</u>	<u>Pri e</u>	<u>Total</u>
1	M-3	Crate Barrel Edge Brass Ar h Floor Mirror 32"Wx1"Dx76"H		2	499.00	998.00
2	M-4	Crate Barrel Stilt Floor Mirror. 44"Wx3"Dx81"H		1	1,299.00	1,299.00
3	Frpl	ECOSMART FIRE BIOETHANOL 32" FLEX SERIES - Single Sided		1	4,395.00	4,395.00

DECOR:

	<u>Code</u>	<u>Name</u>	<u>Pi t re</u>	<u>N mber</u>	<u>Pri e</u>	<u>Total</u>
4		b2 DRIZZLE BLACK UMBRELLA STAND		3	99.95	299.85
5	Crt	Crateandbarrel Ro nd Matte Bla k End Cap Finial and 1" C rtain Rod Set 28"-48"		1	99.95	99.95
6	Crt	Matte Bla k C rtain Rings, Set o 7		1	24.95	24.95
7	Crt	Br shed Ni kel C rtain Tieba ks, Set o 2		1	24.95	24.95

CHAIRS:

	<u>Code</u>	<u>Name</u>	<u>Pi t re</u>	<u>N mber</u>	<u>Pri e</u>	<u>Total</u>
8	Ch-1	Calligaris Holl - Bar Height Frame P29L MATT BRONZE Metal Seat SLR MUD BROWN		6	833	4,998
9	Ch-2	Calligaris Atollo stools Frame P175 POLISHED BRASS Metal Seat SOC EBONY Vintage (S ntheti Material)		3	774	2,322
10	Ch-5	VARIANT 01 CHAIRS ON TERRACE RH MALTA TEAK DINING SIDE CHAIR Weathered Teak/P mi e Fabri - White		24	Frame starting at 1175 Reg lar 881 Member	28,200 <u>21,144</u>
		OR VARIANT 02 CHAIRS ON TERRACE RH VERO LEATHER DINING SIDE CHAIR Bla k Leather/ Bla k Oak Dri ted		24	Starting at 860 Reg lar 645 Member	20,640 <u>15,480</u>

RESTAURANT
OWL'S NEST

DRAWING TITLE:
FURNITURE

DRAWN BY: KEIDUNOV IRINA

SCALE: 1/2"=1'-0"

DATE: 05.27.2022

SHEET : 7.2

CHAIRS:

	<u>Code</u>	<u>Name</u>	<u>Pi t re</u>	<u>N mber</u>	<u>Pri e</u>	<u>Total</u>	
Variant 1							
7	Ch-3	Calligaris Gala - Chair SeatS0F SAND Veni e (Fabri) FrameP15 MATT BLACK Metal		24	694	16,656	26,460
8	Ch-4	Calligaris Gala - Arm hair SeatS0F SAND Veni e (Fabri) FrameP15 MATT BLACK Metal		12	817	9,804	
OR Variant 2							
7	Ch-3	Calligaris Holl - Chair Frame P29L MATT BRONZE Metal Seat S0Y BLACK Veni e (Fabri)		24	621	14,904	25,644
8	Ch-4	Calligaris Fo er - Arm hair Frame P15 MATT BLACK Metal Seat S2N SOIL BROWN Bergen (Fabri)		12	895	10,740	
OR Variant 3							
7	Ch-3	CB2 RAKE BRASS CHAIR Width: 18" Depth: 23.5" Height: 32.25"		24	429.00	10,296	15,684
8	Ch-4	CB2 HIDE FAUX LEATHER BLACK DINING CHAIR Width: 18" Depth: 23.5" Height: 32.25"		12	449.00	5,388	

RESTAURANT
OWL'S NEST

DRAWING TITLE:
FURNITURE


DRAWN BY: KEIDUNOV IRINA

SCALE: 1/2"=1'-0"

DATE: 05.27.2022

SHEET : 7.3

RESTAURANT OWL'S NEST

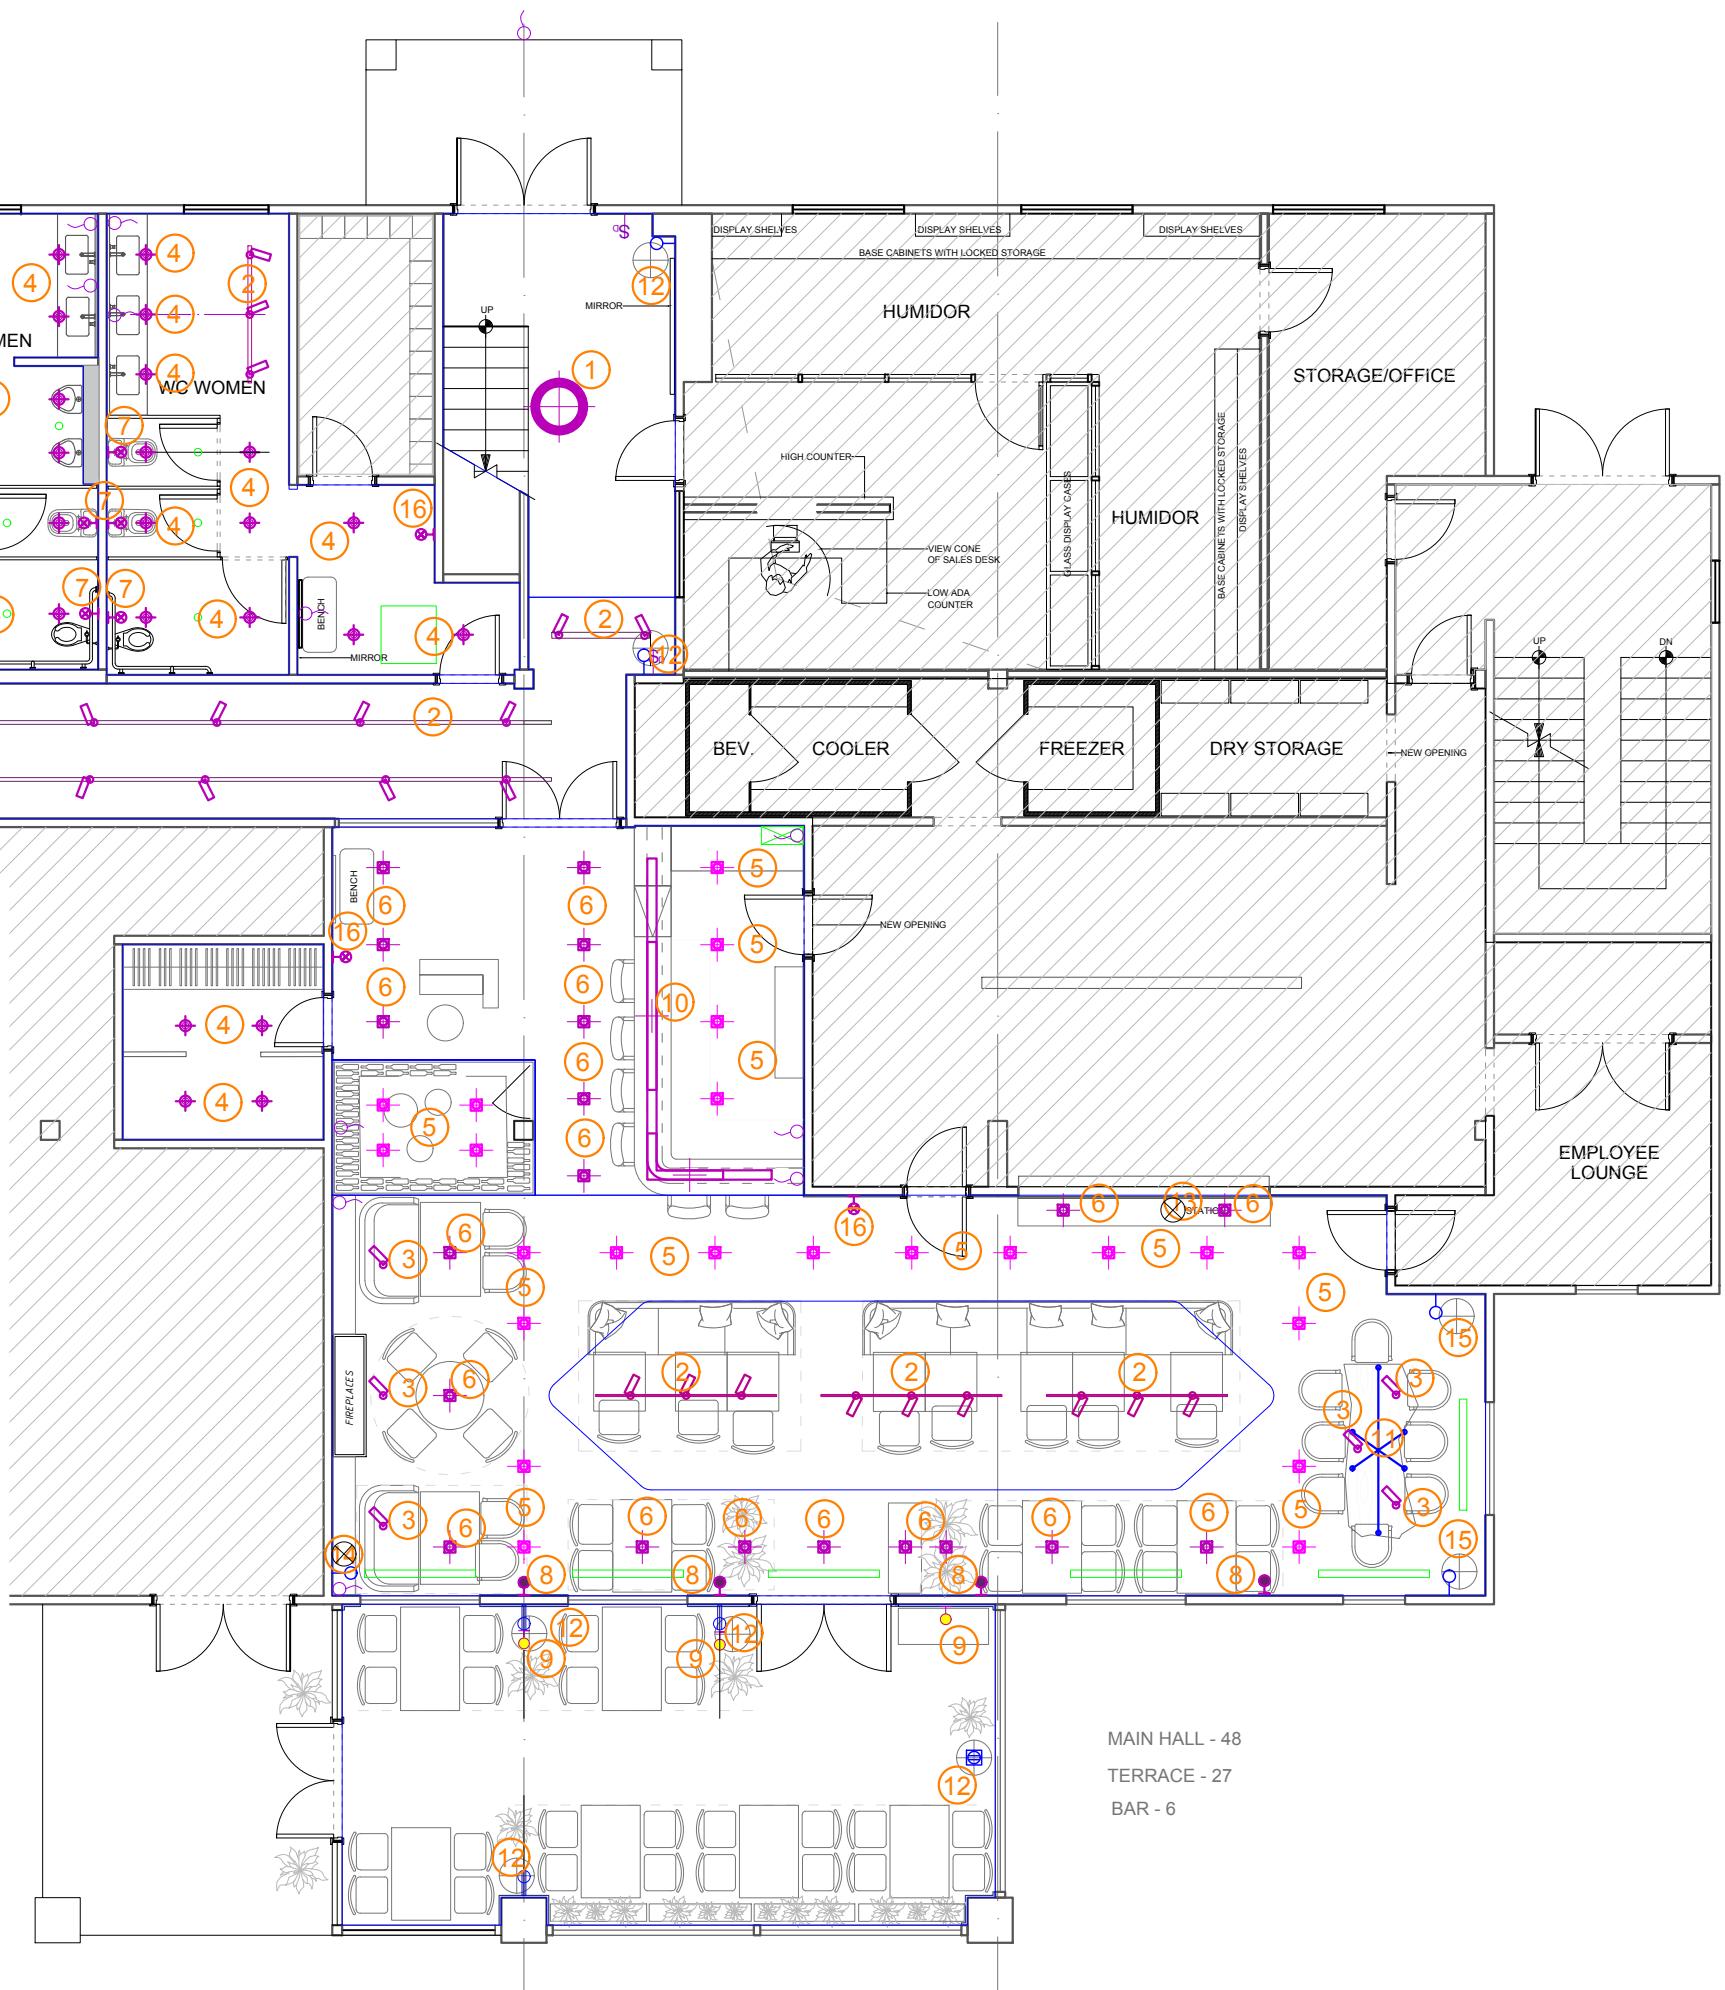

GENERAL NOTES:
 1. ELEVATIONS DEPICTING CABINERY IN DESIGNERS DOCUMENTATION IS FOR DESIGN PURPOSES ONLY;
 2. DESIGNER DOES NOT ASSUME THE RESPONSIBILITY OF ANY STRUCTURAL OR FIELD DIMENSIONS/CONDITIONS;

A1

DRAWING TITLE:
LIGHTING LAYOUT

DRAWN BY: KEIDUNOV IRINA

SCALE: 1/4"=1'-0"

DATE: 05.27.2022

SHEET : 7.4

LIGHTING:

<u>—</u>	<u>Code</u>	<u>Name</u>	<u>Pi t re</u>	<u>N mber</u>	<u>Pri e</u>	<u>Total</u>	<u>—</u>	<u>Code</u>	<u>Name</u>	<u>Pi t re</u>	<u>N mber</u>	<u>Pri e</u>	<u>Total</u>
1	1	Roll and Hill Oval Pendant (Br shed brass) Halo Oval Pendant Dimensions: L 47in/120 m x W 28in/71 m x H 12in/30 m		1	9,470	9,470	7	7	Kell Wearstler Axis Medi m S on e BURNISHED BRASS		5	669.00	3,345
2	2	WAC Lighting LED2020 Silo X20 Beamshi t Tra k Head Finish: Bla k Color Temperat re: 2700 Contin o sl Ad stable Beam angles rom 15 Spot to 50 Flood		30	161.95	4,858.5	8	8	Kell Wearstler Melange Elongated S on e BRASS W/ ALABASTER		4	879.00	3,516
3	3	WAC Lighting Silo X20 LED Monopoint Finish: Bla k Color Temperat re: 2700 Contin o sl Ad stable Beam angles rom 15 Spot to 50 Flood		6	179.95	1079.7	9	9	Kell Wearstler Esker Single Fold S on e Color: BRASS		3	579.00	1,737
4	4	WAC Lighting O l x 3.5-In h LED Ro nd Open Re le tor Trim Finish: White Color Temperat re: 2700 Beam Spread: Narro Flood		29	92.95	2695.55	10	11	Kell Wearstler Utopia Large Linear Pendant GILD WITH FROSTED ACRYLIC h = 54.6" (hang 54.6" rom eiling)		1	2,309.00	2,309.00
5	5	WAC Lighting Volta 2in LED Ro nd Shallo Regressed Trim ith Light Engine Finish: Bla k Color Temperat re: 2700 Beam Spread: Flood CRI: 90		23	269.95	6208.85	11	12	Crate and Barrel Isla Brass Triangle Floor COLOR:Brass		6	399.00	2,394
6	6	WAC Lighting Volta 2in LED Ro nd Shallo Regressed Trim ith Light Engine Finish: Bla k Color Temperat re: 2700 Beam Spread: Spot CRI: 90		20	269.95	5399	12	13	CRATE BARREL Zain Brass Table Lamp 13.75"Wx13.75"Dx18"H		1	199.00	199.00

RESTAURANT
OWL'S NEST


DRAWING TITLE:
LIGHTING

DRAWN BY: KEIDUNOV IRINA


SCALE: 1/2"=1'-0"

DATE: 05.27.2022

SHEET : 7.5

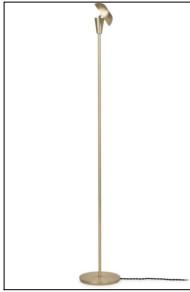	<u>Code</u>	<u>Name</u>	<u>Pi t re</u>	<u>N mber</u>	<u>Pri e</u>	<u>Total</u>
10	(10)	Roll and Hill Mini Endless C ston Pie es (hang 22.6" rom eiling)		1	-	-
14	(14)	Ma s H dson Canal The Table Lamp		1	79.00	79.00
15	(15)	Tin Floor Lamp 124,2x12 m, Brass Coated Iron Brand - Ferm Living		2	379	758
17	(16)	Kell Wearstler Ro ssea Small Bath S on e BURNISHED BRASS WITH ETCHED CRYSTAL		4	589.00	2,356
18		Meridian Table Lamp, Cashmere Brand - Ferm Living		1	197	197
19		b Men Col mn LED Table Lamp, Portable 12 m, Bronze		6	249.95	1499.7

Total rnit re: 48,101.3

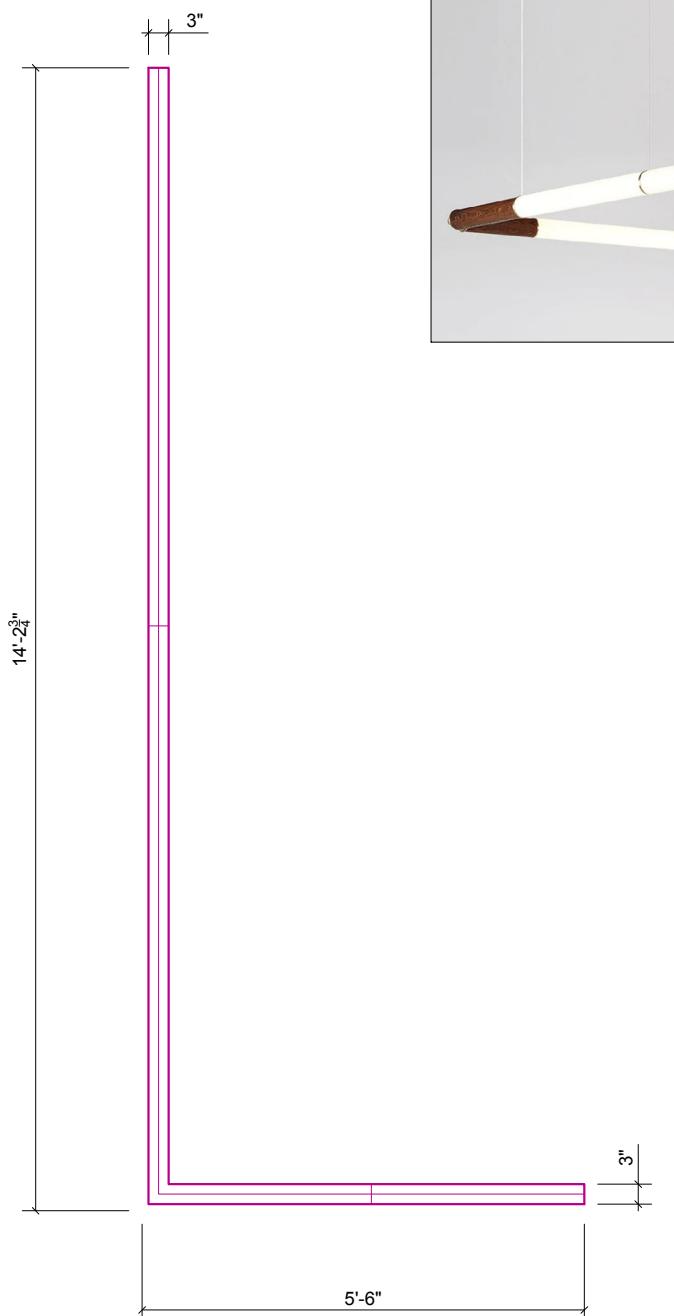

RESTAURANT OWL'S NEST

DRAWING TITLE:
LIGHTING


DRAWN BY: KEIDUNOV IRINA

SCALE: 1/2"=1'-0"

DATE: 05.27.2022

SHEET : 7.6

lighting options:

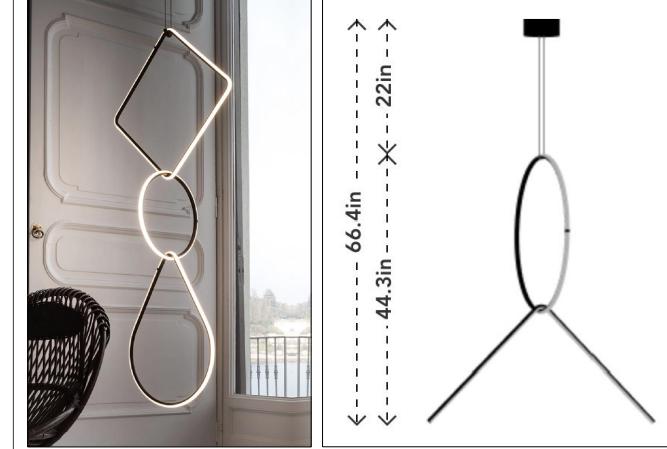	<u>Code</u>	<u>Name</u>	<u>Pi t re</u>	<u>N mber</u>	<u>Pri e</u>
1	1	Roll and Hill Oval Pendant (Br shed brass) Halo Oval Pendant Dimensions: L 47in/120 m x W 28in/71 m x H 12in/30 m		1	9,470
2		FLOS Arrangements - Dimmable Modular Pendant Light		1	2,935
3		FLOS No tamb le ith Bo l Shade LED Dimmable Pendant Light 2 Lo C linders Bo l		1	5,545
4		FLOS Overlap - Dimmable Pendant Lamp S2 - Large		1	4,060

RESTAURANT
OWL'S NEST

DRAWING TITLE:
LIGHTING


DRAWN BY: KEIDUNOV IRINA

SCALE: 1/2"=1'-0"

DATE: 05.27.2022

SHEET : 7.6.1

RESTROOM:

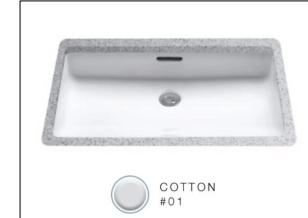	<u>Code</u>	<u>Name</u>	<u>Pi t re</u>	<u>N mber</u>	<u>Pri e</u>	<u>Total</u>
1		TOTO 20-1/2" Undermount Bathroom Sink with Overflow and CeFiONte ^t Ceramic Glaze	 COTTON #01	5	295.40	1,477
2		Delta Trinsic 1-Handle Wall Mount Bathroom faucet Trim Kit in Champagne Bronze		5	310.56	1,552.8
3		Bathroom faucet Trap Brass from the Trimscape Collection		5	346.26	1,731.3
4		Fermliving Basho Wall Hanger Brass		10	29.00	290.00
5		Fermliving Cravatre Hooks - Set of 3 Brass		2	45.00	90.00
6		Fermliving Cravatre Toilet Paper Holder Brass		5	65.00	325.00
7		Signature Hardware Ke West 1.28 GPF Two Piece Elongated Skirted Chair Height Toilet - Seat Included		5	469	2345

RESTAURANT
OWL'S NEST

DRAWING TITLE:
RESTROOM

DRAWN BY: KEIDUNOV IRINA


SCALE: 1/2"=1'-0"

DATE: 05.27.2022

SHEET : 7.7

**RESTAURANT
OWL'S NEST**

PLAN VARIANT 5

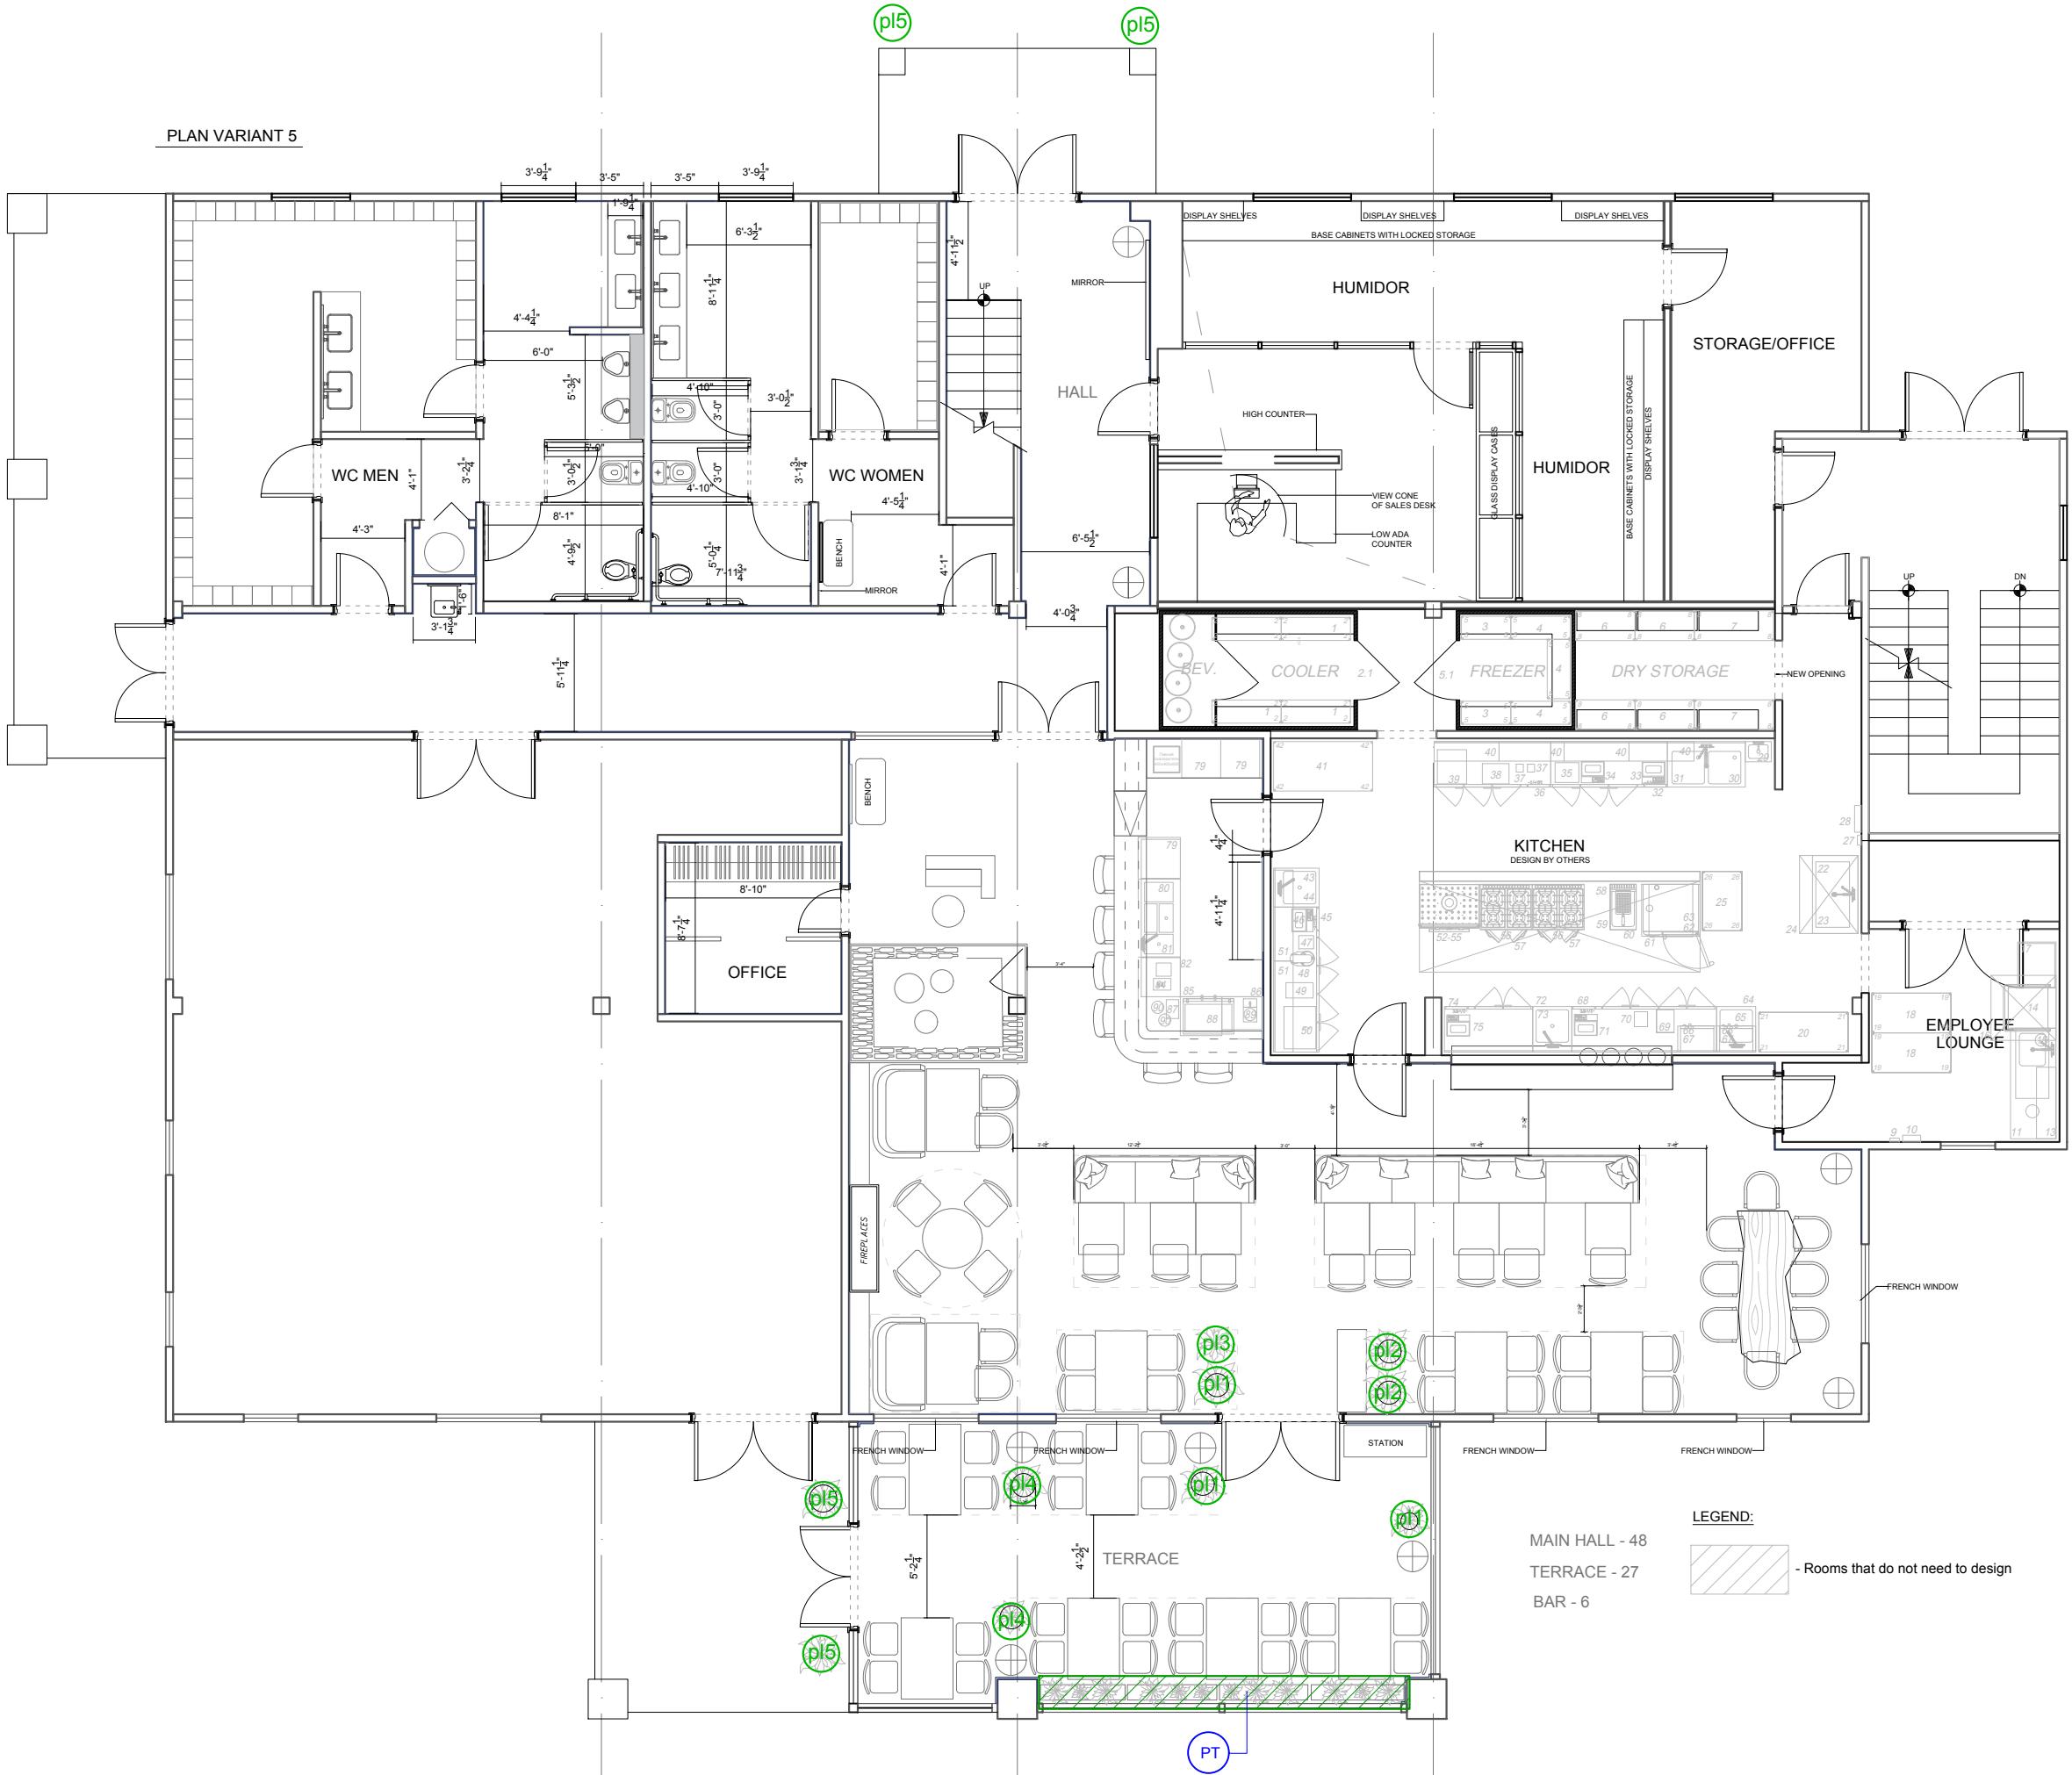

DRAWING TITLE:
PLANTS

DRAWN BY: KEIDUNOV IRINA

SCALE: 1/2"=1'-0"



DATE: 05.27.2022

SHEET : 7.8

PLANTER:

	<u>Code</u>	<u>Name</u>	<u>Pi t re</u>	<u>N mber</u>	<u>Pri e</u>	<u>Total</u>
1	p1	CB2 CLEMENTE FOOTED CLAY INDOOR/OUTDOOR PLANTER 20" Height: 22" Diameter: 14"		3	249.00	747
2	p2	CRATE BARREL D ndee Bronze Floor Indoor/O tdoor Planter ith Tall Stand Overall Dimensions: Height: 31" Diameter: 11"		2	109	218
3	p3	CRATE BARREL D ndee Indoor/O tdoor Bronze Lo Planter ith Stand Overall Dimensions: Height: 16" Diameter: 15.25"		1	109	109
4	p4	CRATE BARREL D ndee Bronze Floor Indoor/O tdoor Planter ith Short Stand Overall Dimensions: Height: 26" Diameter: 11"		2	109	218
5	p5	CB2 SEMINYAK BLACK INDOOR/OUTDOOR CEMENT PLANTER 14.5" 16.5"DIA.X14.5"H		4	119	476

PLANT POTS (4):

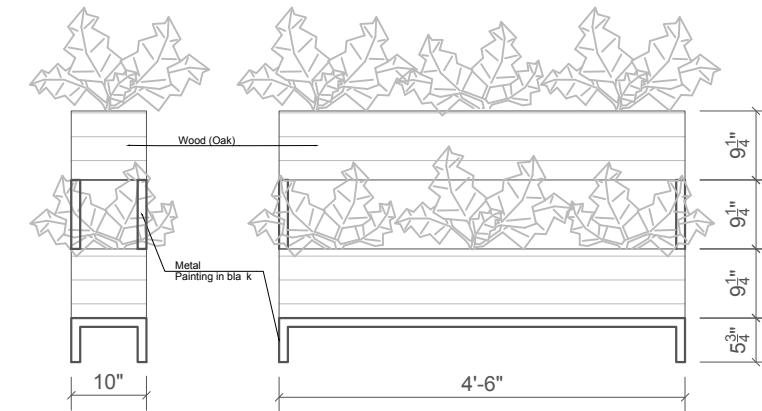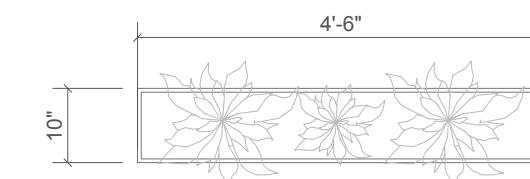

RESTAURANT
OWL'S NEST

DRAWING TITLE:
PLANTS

DRAWN BY: KEIDUNOV IRINA


SCALE: -

DATE: 05.27.2022



SHEET : 7.9

DECOR

RESTAURANT
OWL'S NEST

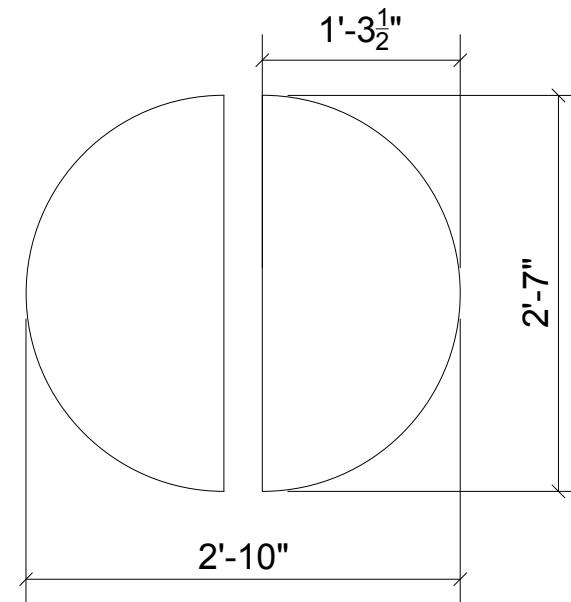

WALL MOUNTED DECOR FROM WOOD

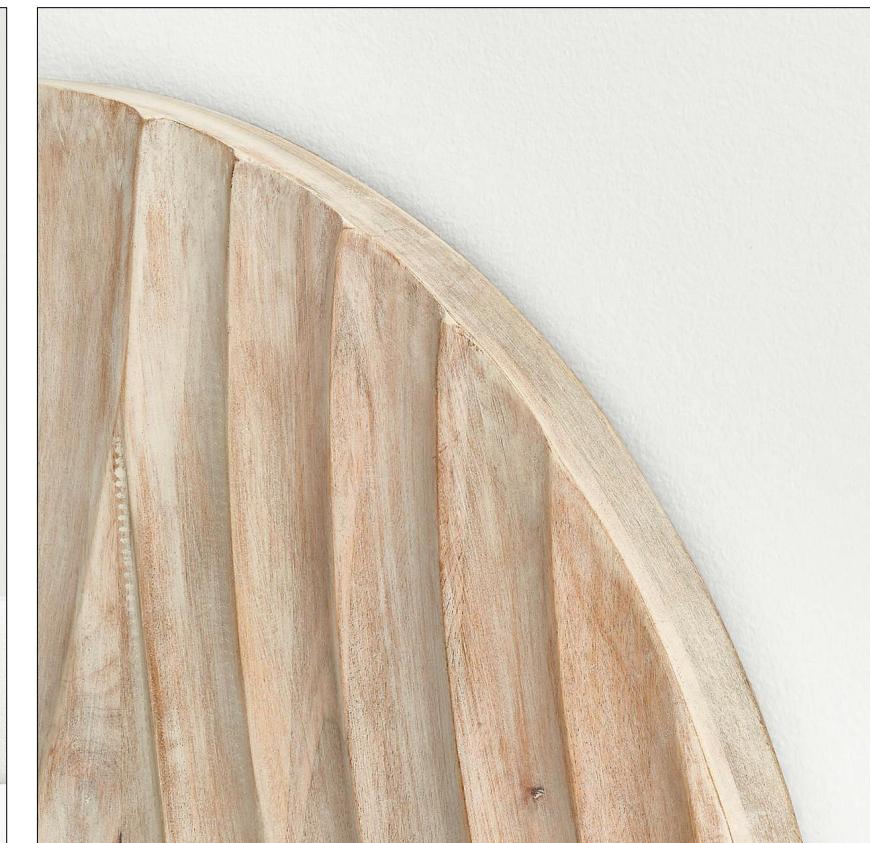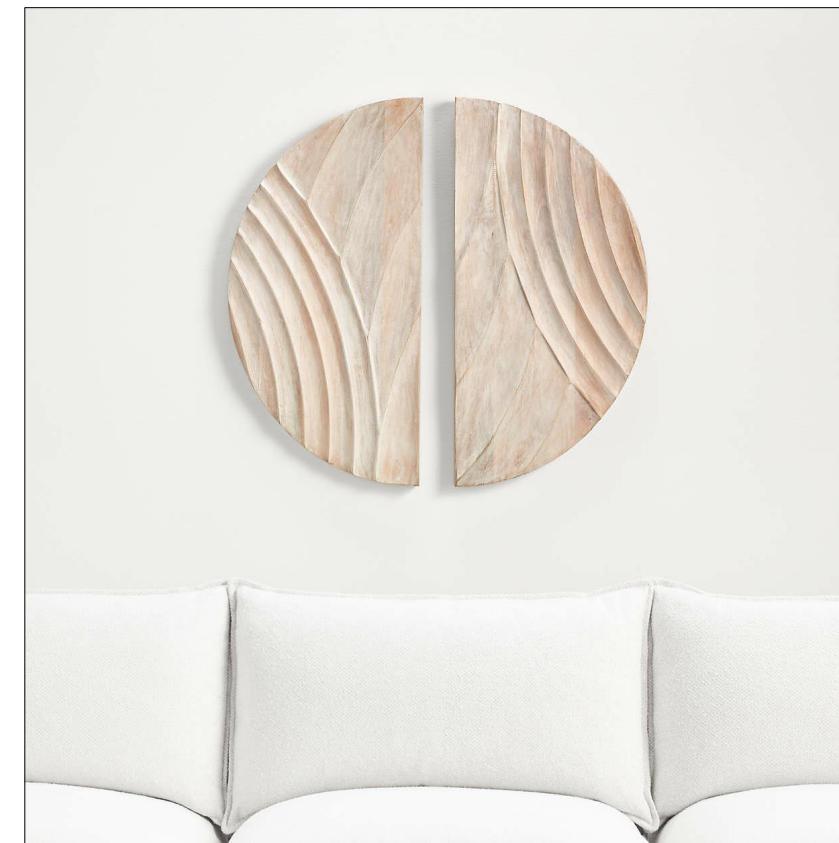

DRAWING TITLE:
LIGHTING





DRAWN BY: KEIDUNOV IRINA

SCALE: -

DATE: 05.27.2022

SHEET : 8.1

CONCEPT RESTROOM SIGN

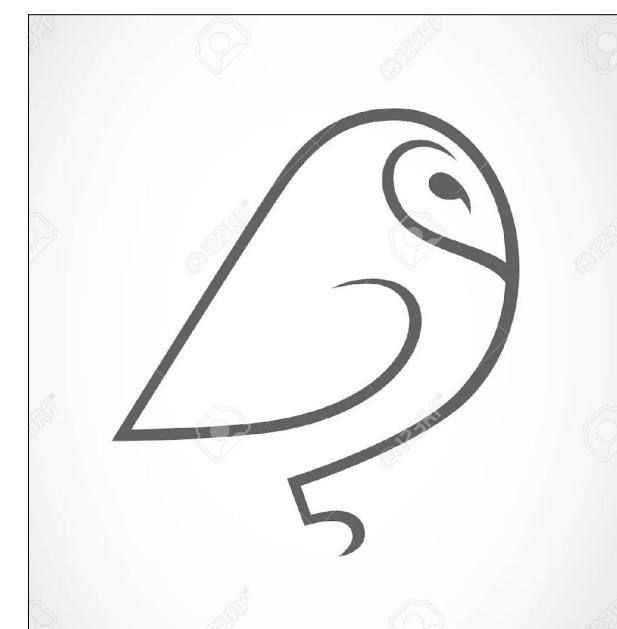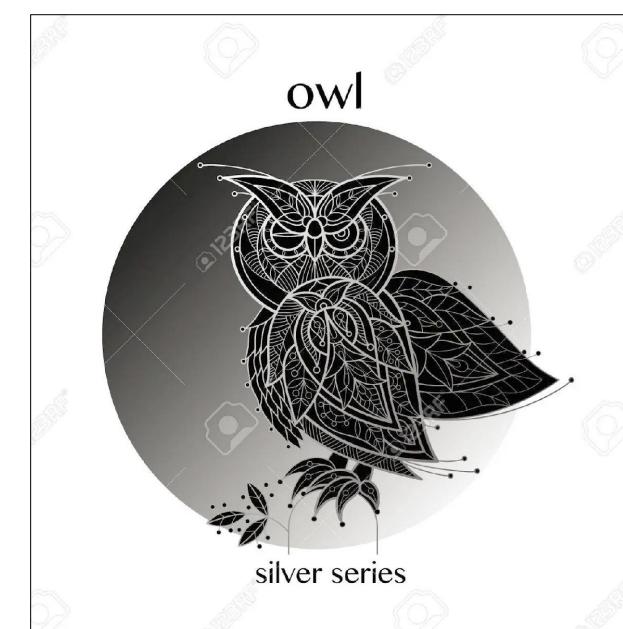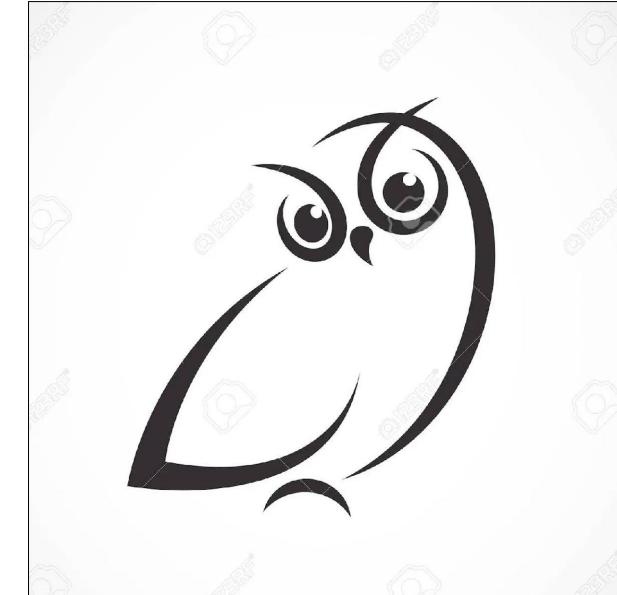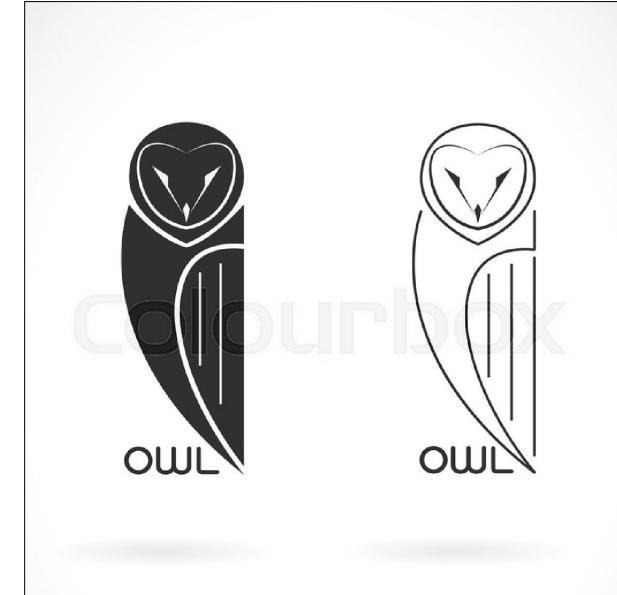

RESTAURANT
OWL'S NEST

DRAWING TITLE:
DECOR

DRAWN BY: KEIDUNOV IRINA

SCALE: -

DATE: 05.27.2022

SHEET : 8.2

A3

CONCEPT FOR OUTDOOR SIGN



RESTAURANT
OWL'S NEST



DRAWING TITLE:
DECOR

DRAWN BY: KEIDUNOV IRINA

SCALE: -

DATE: 05.27.2022

SHEET : 8.3